# 河沿要（仮称）新築計画

基本計画図　／　2026-10-03　／　設計検討（仮）

## 計画概要

| 項目 | 内容 |
|---|---|
| 建設地 | 東京都八王子市大和田町7丁目 |
| 主要用途 | 一戸建ての住宅 |
| 用途地域 | 準工業地域（推定・要確認） |
| 敷地面積 | 2,629.64 ㎡（推定・要測量） |
| 建築面積 | 333.06 ㎡（建ぺい率 12.67%） |
| 延べ面積 | 666.12 ㎡（容積率 25.33%） |
| 構造・階数 | 壁式鉄筋コンクリート造 地上2階 |
| 高さ | 最高高さ 8.50m（設計GL基準） |
| 階高・床高 | 1FL GL+1,500／階高 3,200×2 |
| 地盤 | 設計GL＝南側道路 TP+109.0／FGL GL+450（現況維持） |
| 外構 | RC塀 H2.0m（止水構造）・Dotcon+ 透水舗装・雨水貯留浸透 |
| 根拠資料 | docs/kawazanyo_design_brief_v3.md、国土地理院 基盤地図情報・DEM5A |

## 図面リスト

| 図番 | 図面名称 | 縮尺 |
|---|---|---|
| A-00 | 表紙・図面リスト・計画概要 | — |
| A-01 | 配置図・求積図 | 1:500 |
| A-02 | 外構・雨水排水計画図 | 1:400 |
| A-02D | 門まわり詳細図（ゴミ収集ボックス） | 1:100 |
| A-03 | 1階平面図 | 1:100 |
| A-04 | 2階平面図 | 1:100 |
| A-05 | 屋根伏図 | 1:100 |
| A-06 | 立面図 | 1:200 |
| A-07 | 断面図（建物） | 1:100 |
| A-08 | 敷地断面図（地形・浸水） | 1:300 |
| A-09 | 建具表 | 1:50・1:100 |
| A-10 | 開口部仕様・排煙計画 | — |
| A-11 | 法規チェックリスト（1/3） | — |
| A-12 | 法規チェックリスト（2/3） | — |
| A-13 | 法規チェックリスト（3/3） | — |
| S-01 | 基礎伏図・耐力壁配置図 | 1:100 |
| S-02 | RC塀・止水・透水舗装 詳細図 | 1:30 |
| S-03 | 耐震検討（壁式RC・概算） | — |
| S-04 | 防犯計画（強盗対策） | 1:500 |
| M-01 | 室内環境・冷暖房負荷・必要発電量（概算） | — |
| M-02 | 建物の向きと日射取得 | — |
| M-03 | 窓仕様・紫外線対策 | — |
| M-04 | 暮らし方への対応（睡眠・空気・水・菜園） | — |
| I-01 | 内装設計方針（安全・清掃性） | — |
| I-02 | 内装仕上表 | — |
| I-03 | 1階 家具配置図（仮置き） | 1:100 |
| I-04 | 2階 家具配置図（仮置き） | 1:100 |
| I-05 | 家具表・内装色彩計画（仮置き） | — |
| E-01 | Wi-Fi 電波計画 | 1:200 |
| E-02 | 制御・分電盤・情報コンセント計画 | — |
| E-03 | 外構照明・防虫計画図 | 1:500 |
| E-04 | 照明配置図（1階） | 1:100 |
| E-05 | 照明配置図（2階） | 1:100 |
| E-06 | 照明器具表・照度計算・制御 | — |

| | | | |
|---|---|---|---|
| 工事名称 | 河沿要（仮称）新築計画 | | |
| 図面名称 | 表紙・図面リスト・計画概要 | 図番 | A-00 |
| 縮尺 | A3　— | 日付　2026-10-03 | 設計　設計検討（仮） |
| 段階 | 基本計画 | ／ 本図は建築基準法令に基づく計画段階の検討図であり、確認申請・構造計算・関係機関協議により確定する | |

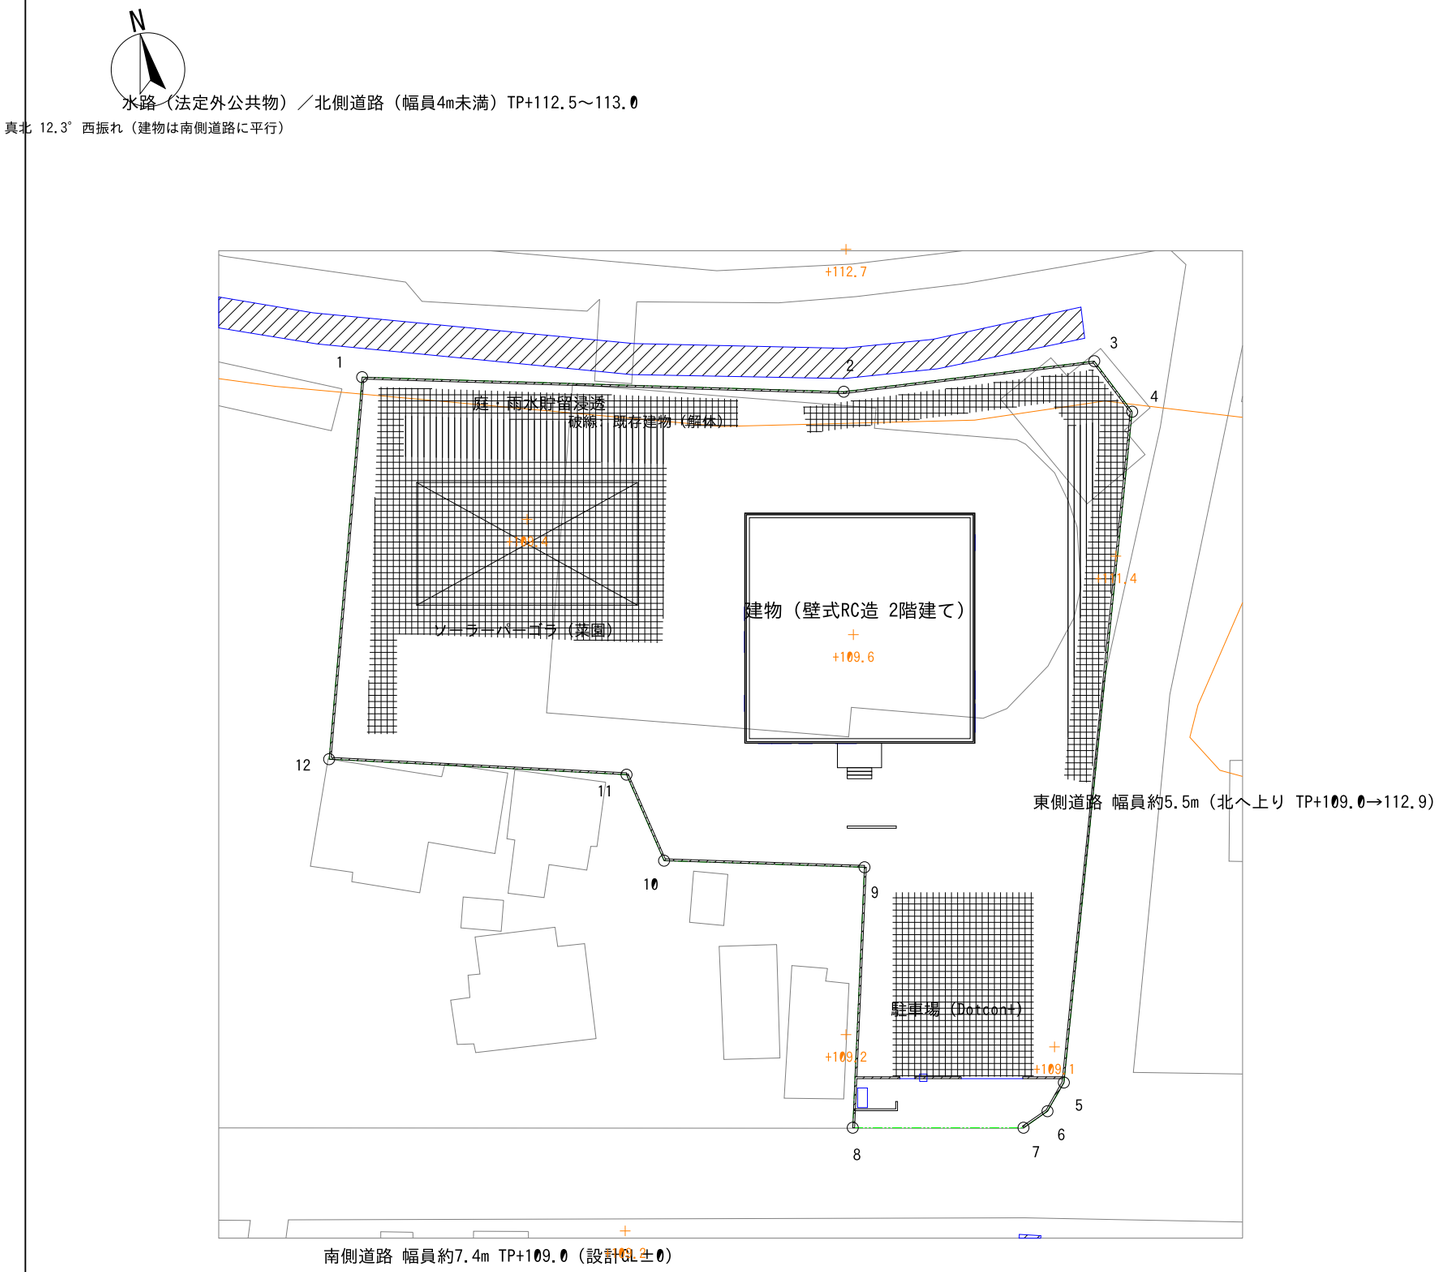


## 座標求積表（建物 X1・Y1 壁芯交点を原点、m）

| 点 | X(m) | Y(m) | Xn(Yn+1−Yn−1) |
|---|---|---|---|
| 1 | −31.44 | 29.59 | −941.73 |
| 2 | 7.82 | 28.40 | 10.20 |
| 3 | 28.24 | 30.89 | −46.03 |
| 4 | 31.33 | 26.77 | −1842.02 |
| 5 | 25.76 | −27.90 | −1468.64 |
| 6 | 24.43 | −30.24 | −90.00 |
| 7 | 22.47 | −31.59 | −30.27 |
| 8 | 8.55 | −31.59 | 181.52 |
| 9 | 9.51 | −10.36 | 206.95 |
| 10 | −6.83 | −9.82 | −51.55 |
| 11 | −9.89 | −2.81 | −81.83 |
| 12 | −34.13 | −1.55 | −1105.87 |
| | | 倍面積 | 5259.27 |
| | | 面積 | 2629.64 m² |

| 項目 | 面積・比率 |
|---|---|
| 敷地面積（推定） | 2,629.64 m²（795.5坪） |
| 建築面積（壁芯） | 333.06 m² |
| 延べ面積 | 666.12 m² |
| 建ぺい率 | 12.67%（≦60%） |
| 容積率 | 25.33%（≦200%） |

※ 西側境界は標高109.6の点を通り駐車場白線に平行な直線（ご指定）。13〜15は隣接建物からの推定（要測量）。

## 配置図 S=1:500

敷地境界・道路縁・水路・隣接建物・等高線：国土地理院 基盤地図情報／標高：DEM5A（TP m）

| | | | | |
|---|---|---|---|---|
| 工事名称 | 河沿要（仮称）新築計画 | | | |
| 図面名称 | 配置図・求積図 | | | 図番 A-01 |
| 縮尺 | A3 1:500 | 日付 2026-10-03 | 設計 設計検討（仮） | |
| 段階 | 基本計画 ／ 本図は建築基準法令に基づく計画段階の検討図であり、確認申請・構造計算・関係機関協議により確定する | | | |

## 内水対策

1. RC塀の基礎～FGL+600を止水構造。門扉には着脱式止水板 H600
2. Dotcon+ 約838m²（駐車場・アプローチ 213m²＋菜園・北・東の帯 625m²）× 13L/m² ≒ 10.9m³ の一時貯留
3. 地下貯留槽 25m³（菜園の散水に利用）。菜園まわりの透水設備は浸透トレンチに代えて全て Dotcon+（透水係数は地盤調査で確認）
4. 塀の低い位置にフラップ弁付き排水口（道路側溝からの逆流防止）
5. 建物：1FL=GL+1,500、床下は設備ピット、逆流防止弁・排水ポンプ（非常電源）

参考：時間雨量50mmで敷地全体の流出量は約131m³/h。貯留・浸透は初期雨水の抑制が主目的で、超過分は止水と排水ポンプで対応

## 防犯

RC塀 H2.0m（東側の坂道沿いは道路面+1.2m以上）。上部に侵入防止金物、センサーライト・防犯カメラ、門扉は塀と同じ高さ

N

真北 12.3° 西振れ（建物は南側道路に平行）

外構・雨水排水計画図 S=1:400

| | | | | |
|---|---|---|---|---|
| 工事名称 | 河沿要（仮称）新築計画 | | | |
| 図面名称 | 外構・雨水排水計画図 | | | 図番 A-02 |
| 縮尺 | A3　1:400 | 日付　2026-10-03 | 設計　設計検討（仮） | |
| 段階 | 基本計画　／　本図は建築基準法令に基づく計画段階の検討図であり、確認申請・構造計算・関係機関協議により確定する | | | |

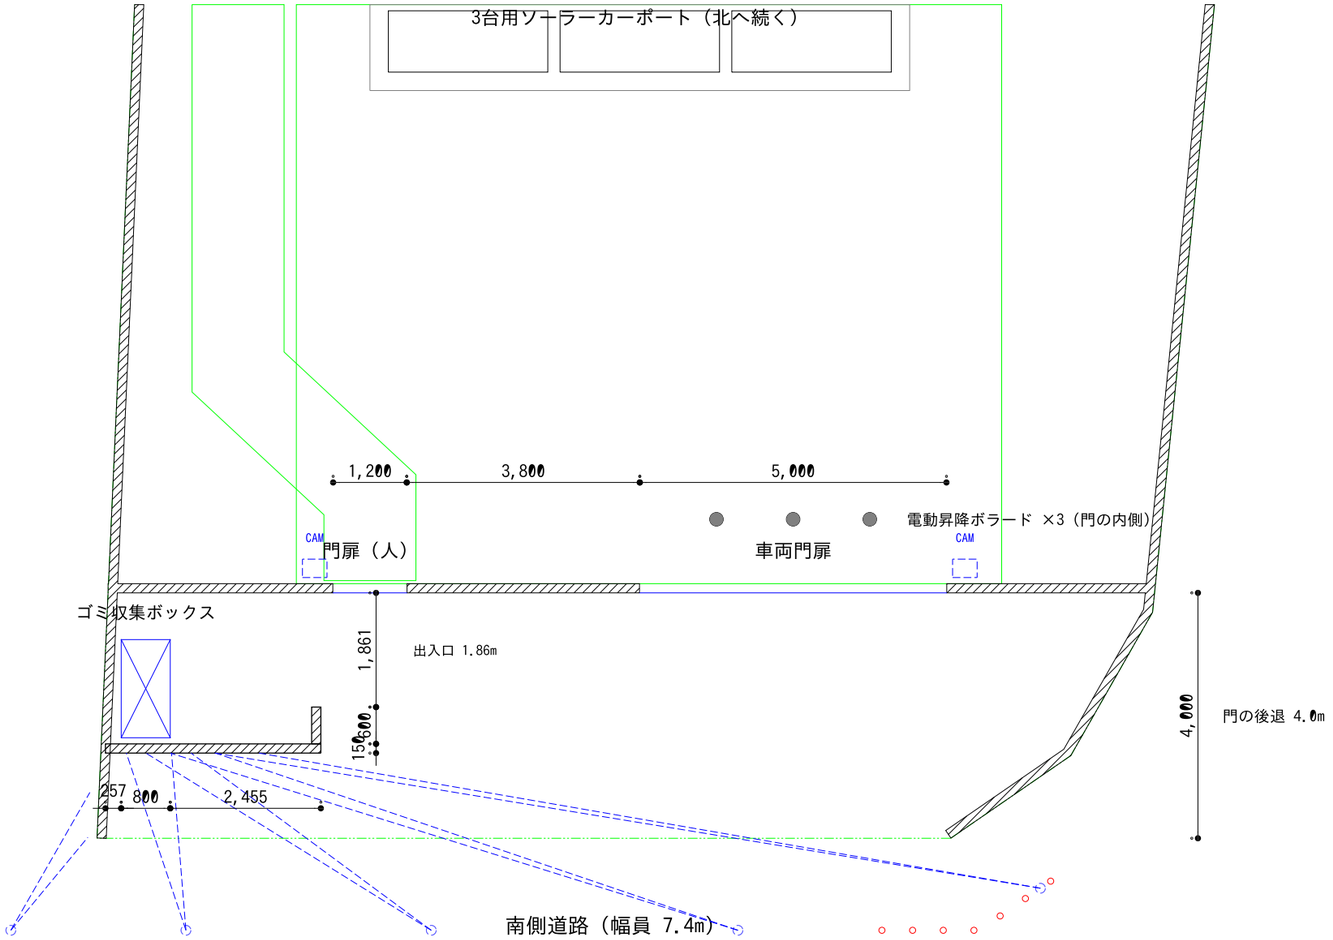


視線（目の高さ1.5m）：道路から 158地点で判定 → ボックスの一部が見える地点 7（南東の角から斜めに・判定点16のうち最大5点）

## 門まわり平面詳細図 S=1:100

## 計画の考え方

南側の門（人用・車両）を道路境界から 4.0m 後退させ、門の前を車1台分の待避・ゴミ出しのスペースとする（門を開ける間、車が道路に止まらない）

ゴミ収集ボックス W800×D1,600×H1,200 を門の外・西の角に、西の塀に沿わせ南の目隠し壁に寄せて置く（壁から100）。扉は東向き。収集作業者は門を通らずに出し入れできる

ボックスの南に自立目隠し壁（西の塀から X12.2m まで）H1.8m、東端に北へ 0.6m の短い袖壁。袖壁と門の塀の間（約1.86m）から出し入れする

正面（南側道路）からは壁しか見えない。南東の角（東側道路の南端付近）から斜めに見ると、袖壁の脇からボックスの一部がわずかに見える（施主了承）

壁は RC（独立基礎）で門・塀と同じ仕上げ。ボックスは金属製の置き型（基礎に固定しない＝建築物に当たらない想定）。中は臭気がこもらないよう上部に通気

防虫：ボックスは密閉型・蓋付き、近くに照明を置かない（収集は日中）

人用門扉は東へ移し（X12.4〜13.6m）、アプローチは門を入ってすぐ西へ寄せ、西の塀沿いを北へ進む

## 車両盗難対策

門：電動スライド門扉 H2,000（目隠し・施錠・開閉センサー・こじ開け検知、停電時は内側からのみ手動解錠）

電動昇降ボラード 3本（φ220・地上高800）を車両門扉の内側に設け、夜間・不在時は上げる。門扉を壊されても車を出せない

駐車：前向き駐車（車の前面＝CAN 配線の多いヘッドライト側を敷地の奥へ）

鍵：電波遮断キーボックス（玄関ホールの収納内、外壁から5m 以上・RC 壁の内側）（リレーアタック対策）

監視：赤外線カメラ（940nm・不可視光、虫を寄せない）門・カーポート各2台、録画は機械室・異常時は bot へ通知。塀の内側に赤外線ビームセンサー、門・ボラードの状態を制御基盤に集約。勝手口は廃止し、出入口は南の2か所に限る

| | | | | |
|---|---|---|---|---|
| 工事名称 | 河沿要（仮称）新築計画 | | | |
| 図面名称 | 門まわり詳細図（ゴミ収集ボックス） | | | 図番 A-02D |
| 縮尺 | A3　1:100 | 日付　2026-10-03 | 設計　設計検討（仮） | |
| 段階 | 基本計画　／　本図は建築基準法令に基づく計画段階の検討図であり、確認申請・構造計算・関係機関協議により確定する | | | |

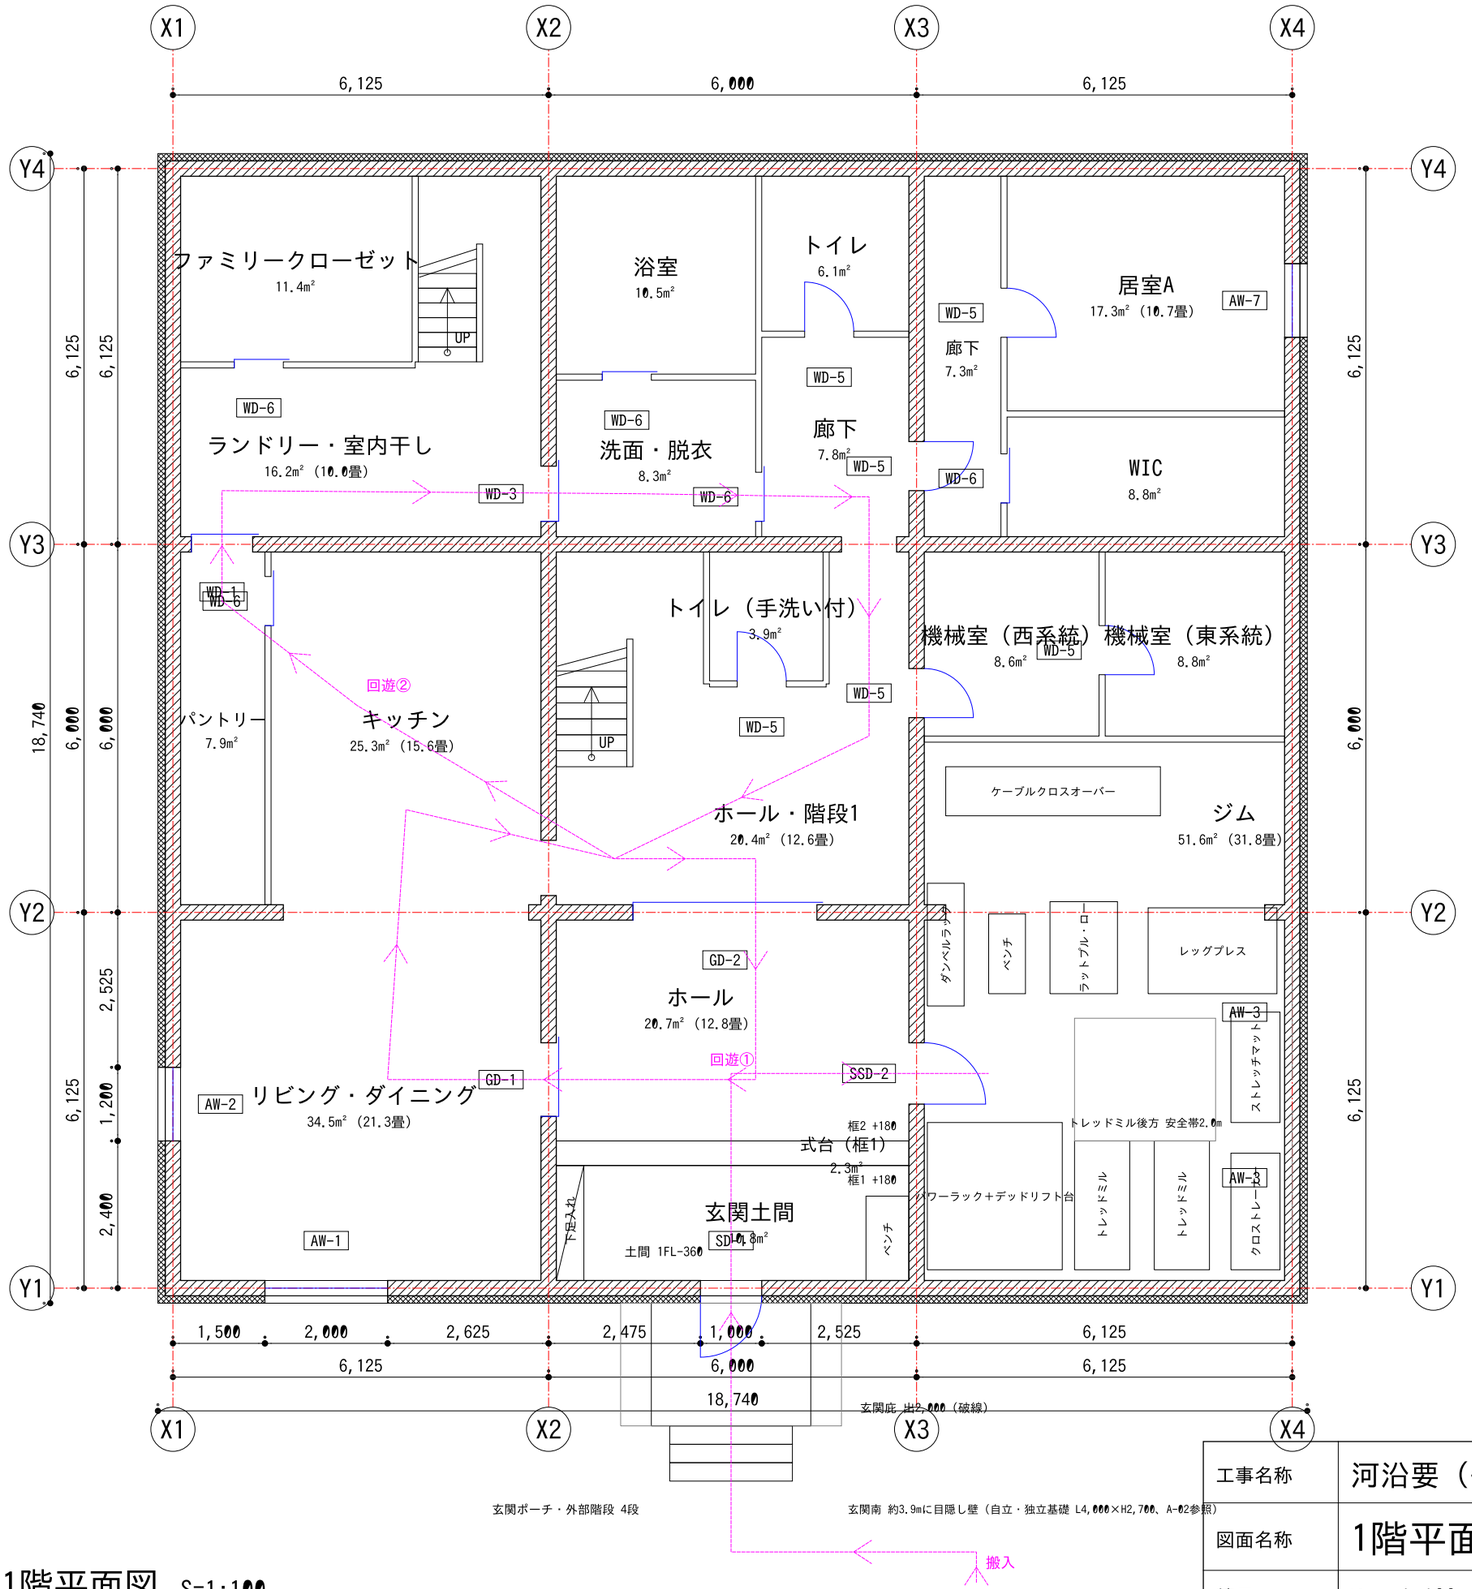


## 凡例

- RC壁 t=250（耐力壁）
- 外断熱100＋外装20
- 乾式間仕切（LGS）t=100
- 通り芯（壁芯）
- 動線（回遊・家事・搬入）

N

真北 12.3° 西振れ（建物は南側道路に平行）

## 計画の考え方（v4・B案 内寸18.0m角）

回遊①（家族）：玄関ホール→LDK→キッチン→ホール→玄関。行き止まりのない一周動線

回遊②（家事）：キッチン→パントリー→ランドリー→洗面脱衣→廊下→ホール→キッチン

洗う→干す→しまう：ランドリー・室内干し → 隣のファミリークローゼット／階段2で2階ファミクロへ直行

ジム 51.6m²（当初34.5m²の1.49倍）。機器はエニタイムフィットネス等の商業ジム相当（10品目を配置）。搬入：外部階段 → 玄関 W1,000×H2,300 → 土間 → 二重框 → ホールで右折 → 遮音ドア W1,000 → ジム

玄関：SICなし（土間に下足入れ・ベンチ）。二重框：土間 1FL-360 → 式台 1FL-180 → ホール 1FL。中央スパン6.0mで土間幅5.75m

階段1：有効幅1,150・蹴上177.8・踏面260。中央のトイレは手洗い付き 3.9m²

ジム床：積載荷重 5,000N/m²（提案）・浮き床。天井は直天井（CH 約2,900）を推奨

ジムの窓：外部扉を廃止し、窓は天井際の FIX 高窓（窓台 FL+2,000、防犯合わせガラス・トリプル Low-E）に集約

防音：ジムは浮き床＋遮音ドア Ts-35、機械室・WIC を緩衝帯として居室Aと分離。真上は2階シアター（騒音ゾーンを上下に集約）

排煙：LDK・ジム・居室Aは機械排煙（令126条の3）。窓は全窓 FIX の樹脂サッシ・Low-E トリプル（UVカット防犯合わせ CP、全窓）。南・東・西は外付け電動スクリーン（M-03）

寸法：mm、面積：壁芯内法の概算

## 1階平面図 S=1:100

1FL = 設計GL+1,500（TP+110.50）／天井高 CH=2,600

| | | | | |
|---|---|---|---|---|
| 工事名称 | 河沿要（仮称）新築計画 | | | |
| 図面名称 | 1階平面図 | | | 図番 A-03 |
| 縮尺 | A3 1:100 | 日付 2026-10-03 | 設計 設計検討（仮） | |
| 段階 | 基本計画 ／ 本図は建築基準法令に基づく計画段階の検討図であり、確認申請・構造計算・関係機関協議により確定する | | | |

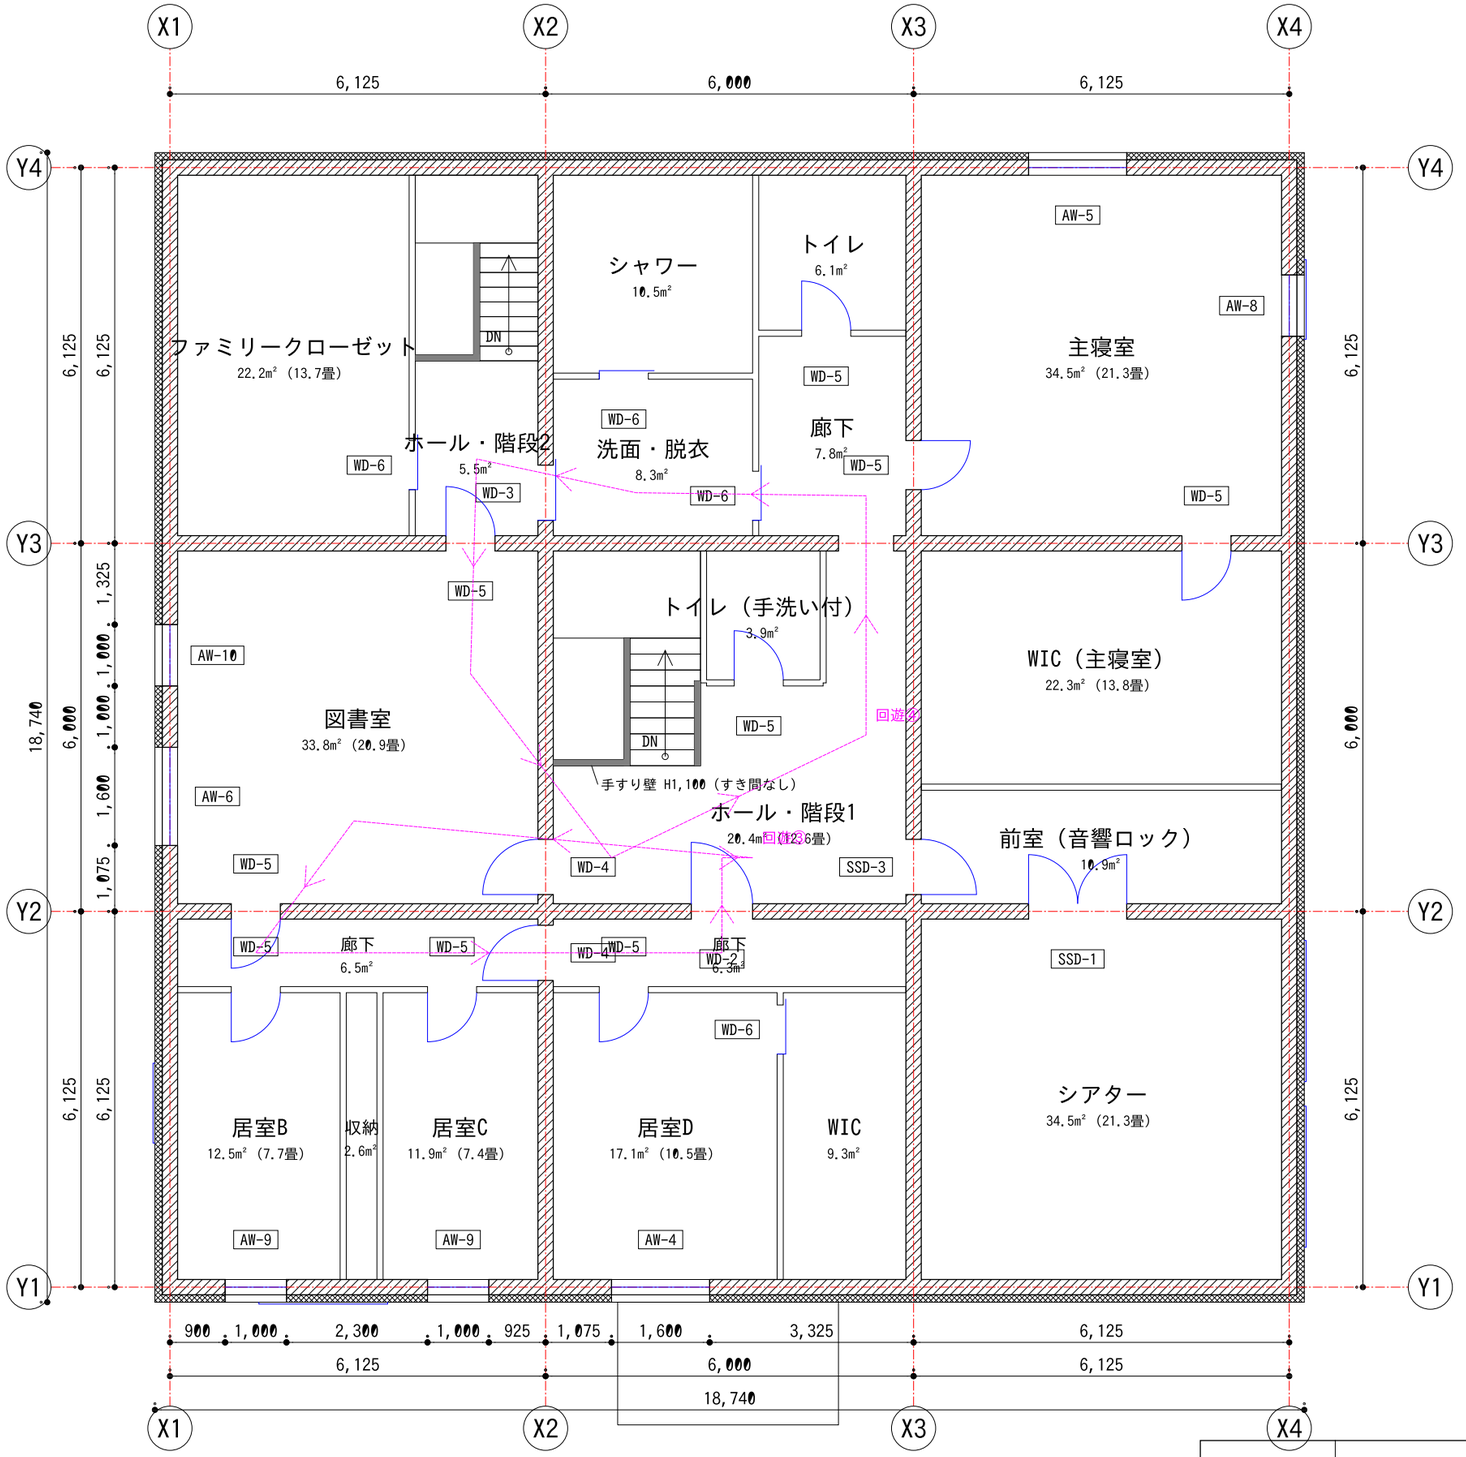


## 凡例

- RC壁 t=250（耐力壁）
- 外断熱100＋外装20
- 乾式間仕切（LGS）t=100
- 通り芯（壁芯）
- 動線（回遊・家事・搬入）

N

真北 12.3° 西振れ（建物は南側道路に平行）

## 計画の考え方（v4・B案 内寸18.0m角）

回遊③：ホール→図書室→南廊下→ホール。回遊④：ホール→洗面→階段2ホール→図書室→ホール

窓：全窓 FIX（樹脂サッシ・Low-E トリプル・UVカット合わせガラス、Uw≦0.90）。南・東・西は外付け電動スクリーン（M-03）。排煙は各居室の天井排煙口による機械排煙（A-10 参照）

防音：シアターは前室（音響ロック）＋両開き遮音扉 Ts-40。主寝室とは前室・WIC の2層で分離

居室B・C・D は収納・WIC を間に挟んで隣室と分離（戸境に収納）

ファミリークローゼット：1階ランドリーから階段2で直結

寸法：mm、面積：壁芯内法の概算

## 2階平面図 S=1:100

2FL = 設計GL+4,700（TP+113.70）／天井高 CH=2,600

| | | | | |
|---|---|---|---|---|
| 工事名称 | 河沿要（仮称）新築計画 | | | |
| 図面名称 | 2階平面図 | | | 図番 A-04 |
| 縮尺 | A3 1:100 | 日付 2026-10-03 | 設計 設計検討（仮） | |
| 段階 | 基本計画 ／ 本図は建築基準法令に基づく計画段階の検討図であり、確認申請・構造計算・関係機関協議により確定する | | | |

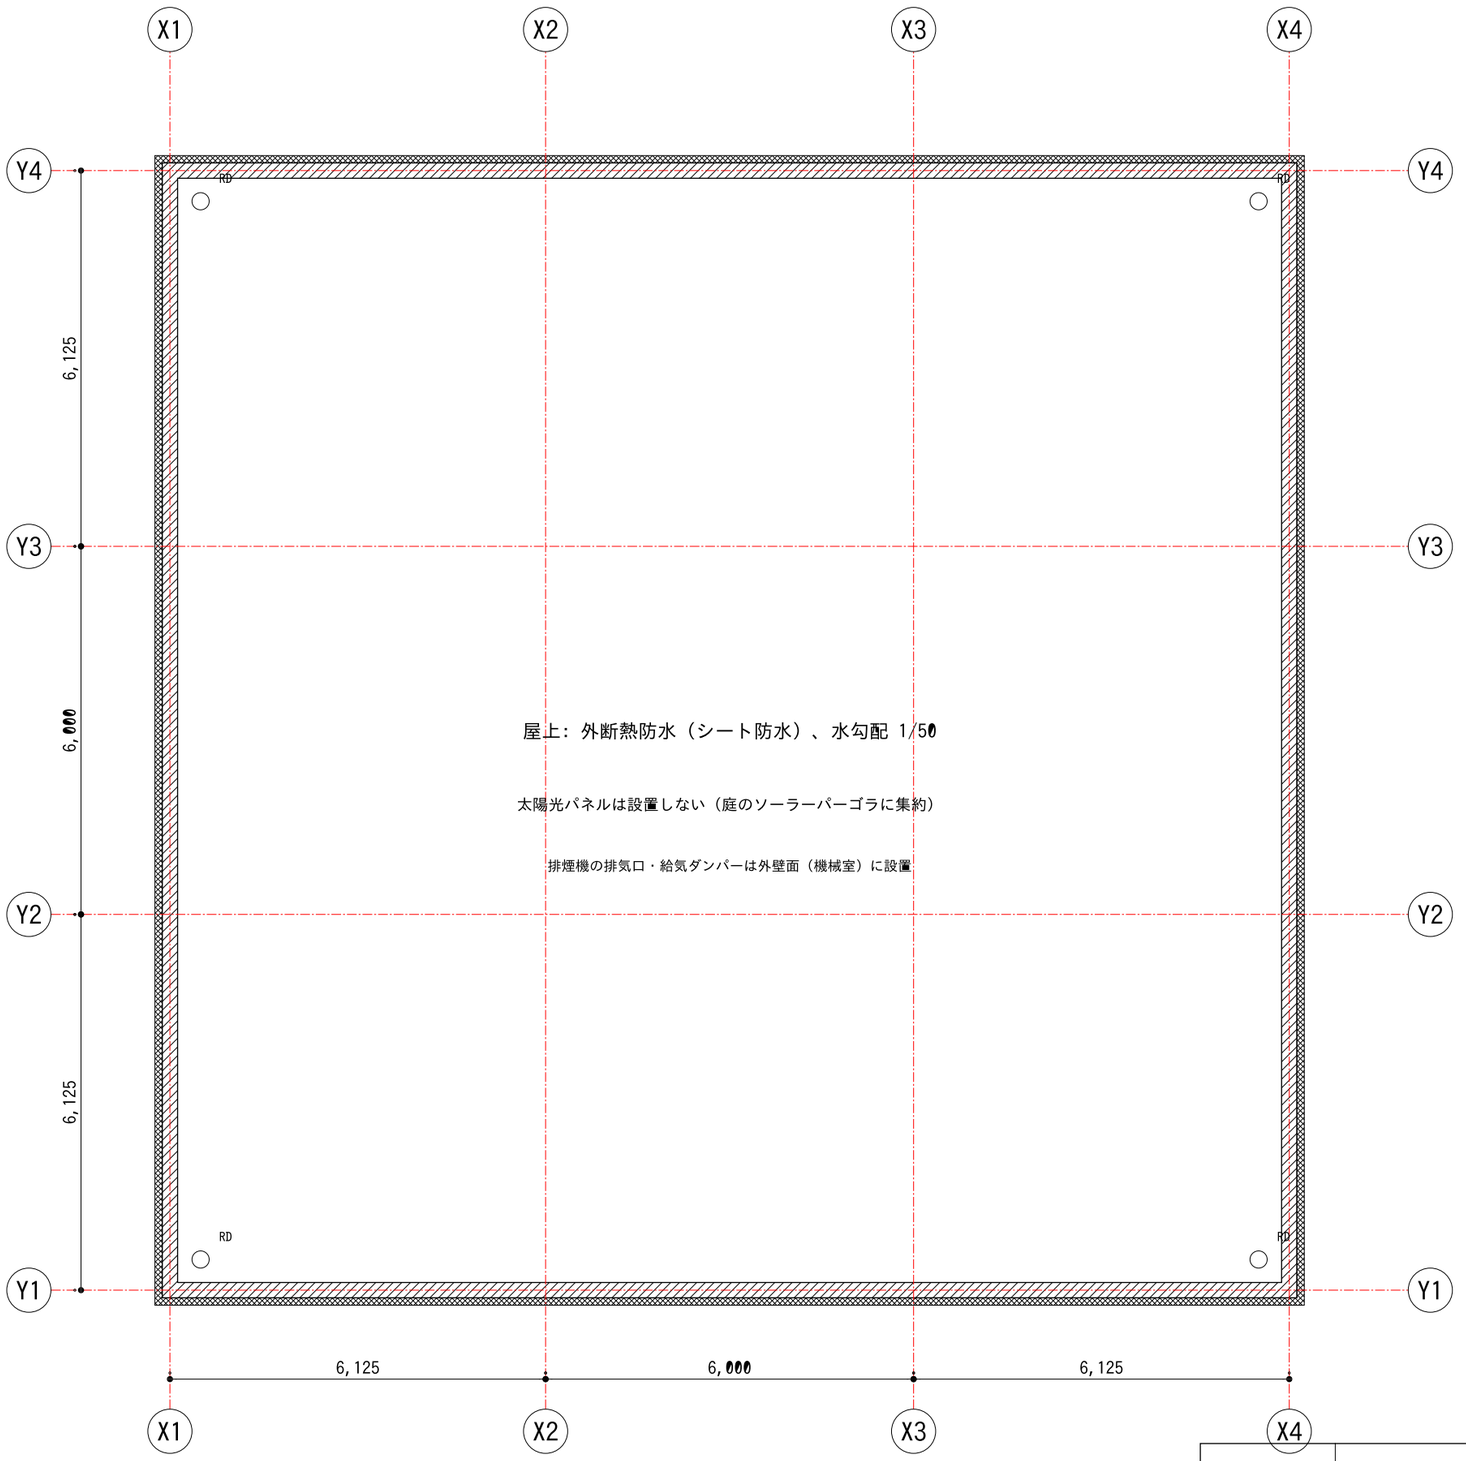


N

真北 12.3° 西振れ（建物は南側道路に平行）

## 屋根伏図 S=1:100

RFL = 設計GL+7,900／パラペット天端 GL+8,500

| | | | | |
|---|---|---|---|---|
| 工事名称 | 河沿要（仮称）新築計画 | | | |
| 図面名称 | 屋根伏図 | | | 図番 A-05 |
| 縮尺 | A3 1:100 | 日付 2026-10-03 | 設計 設計検討（仮） | |
| 段階 | 基本計画 ／ 本図は建築基準法令に基づく計画段階の検討図であり、確認申請・構造計算・関係機関協議により確定する | | | |

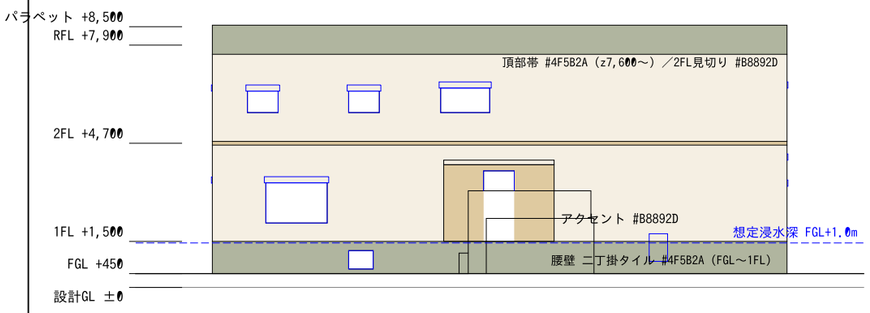


南立面図（南から12.3° 西回りの面）

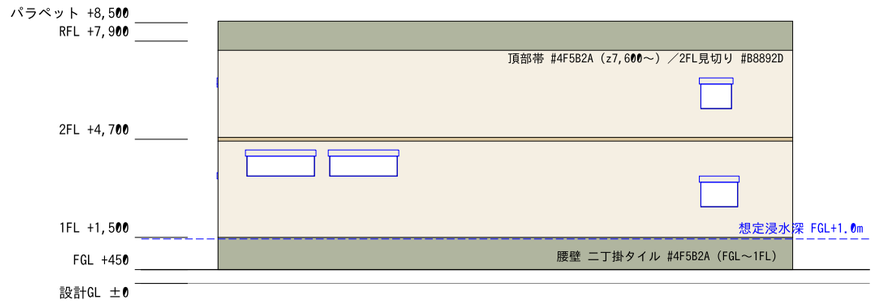


東立面図（東から12.3° 西回りの面）

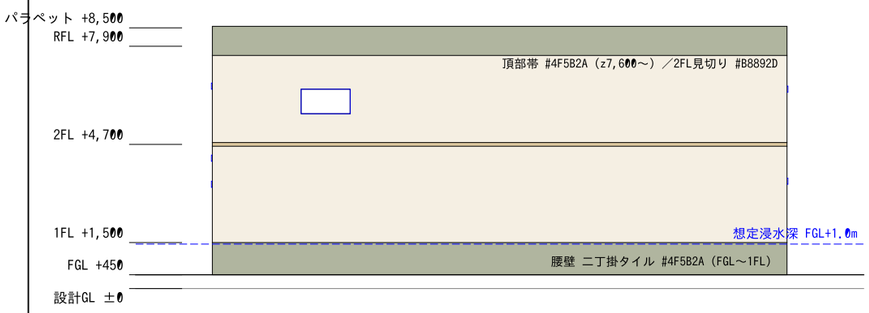


北立面図（北から12.3° 西回りの面）

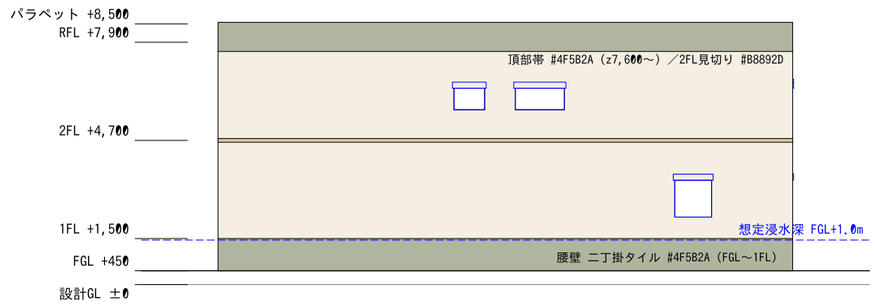


西立面図（西から12.3° 西回りの面）

外壁: 外断熱100＋外装塗装（ベース #F5EFE3、頂部帯 #4F5B2A）、
腰壁 FGL～1FL（GL+1,500）は二丁掛タイル #4F5B2A、玄関まわり・2FL見切り #B8892D（色はいずれも仮定）

窓: 全窓 FIX 樹脂サッシ・Low-E トリプル（UVカット合わせ）。南・東・西の窓上の箱は外付け電動スクリーンのボックス（M-03）

| | | | | |
|---|---|---|---|---|
| 工事名称 | 河沿要（仮称）新築計画 | | | |
| 図面名称 | 立面図 | | | 図番 A-06 |
| 縮尺 | A3 1:200 | 日付 2026-10-03 | 設計 設計検討（仮） | |
| 段階 | 基本計画 ／ 本図は建築基準法令に基づく計画段階の検討図であり、確認申請・構造計算・関係機関協議により確定する | | | |

## 断面図 A-A（X2-X3間、階段1を通る南北断面）

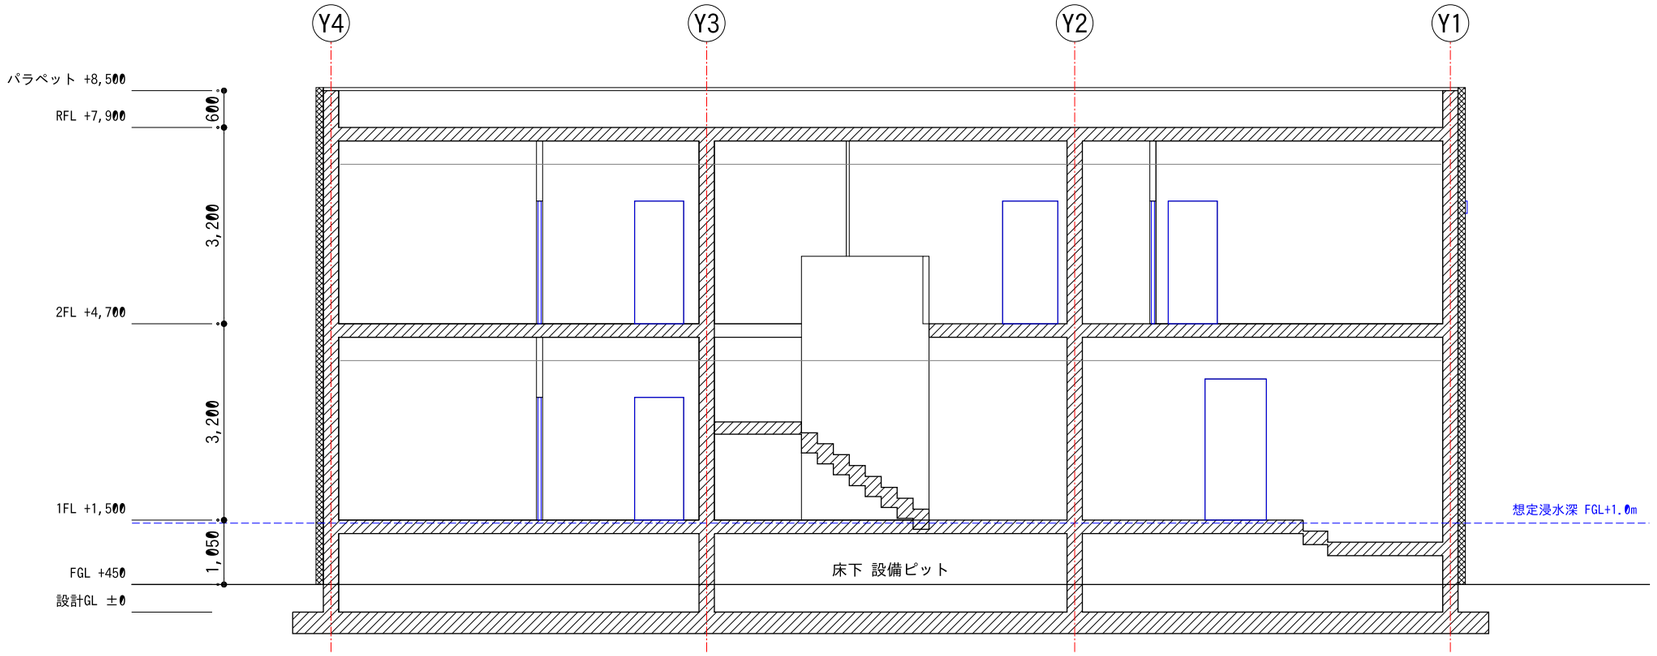


## 断面図 B-B（Y1-Y2間、LDK・玄関土間・ジム搬入扉を通る東西断面）

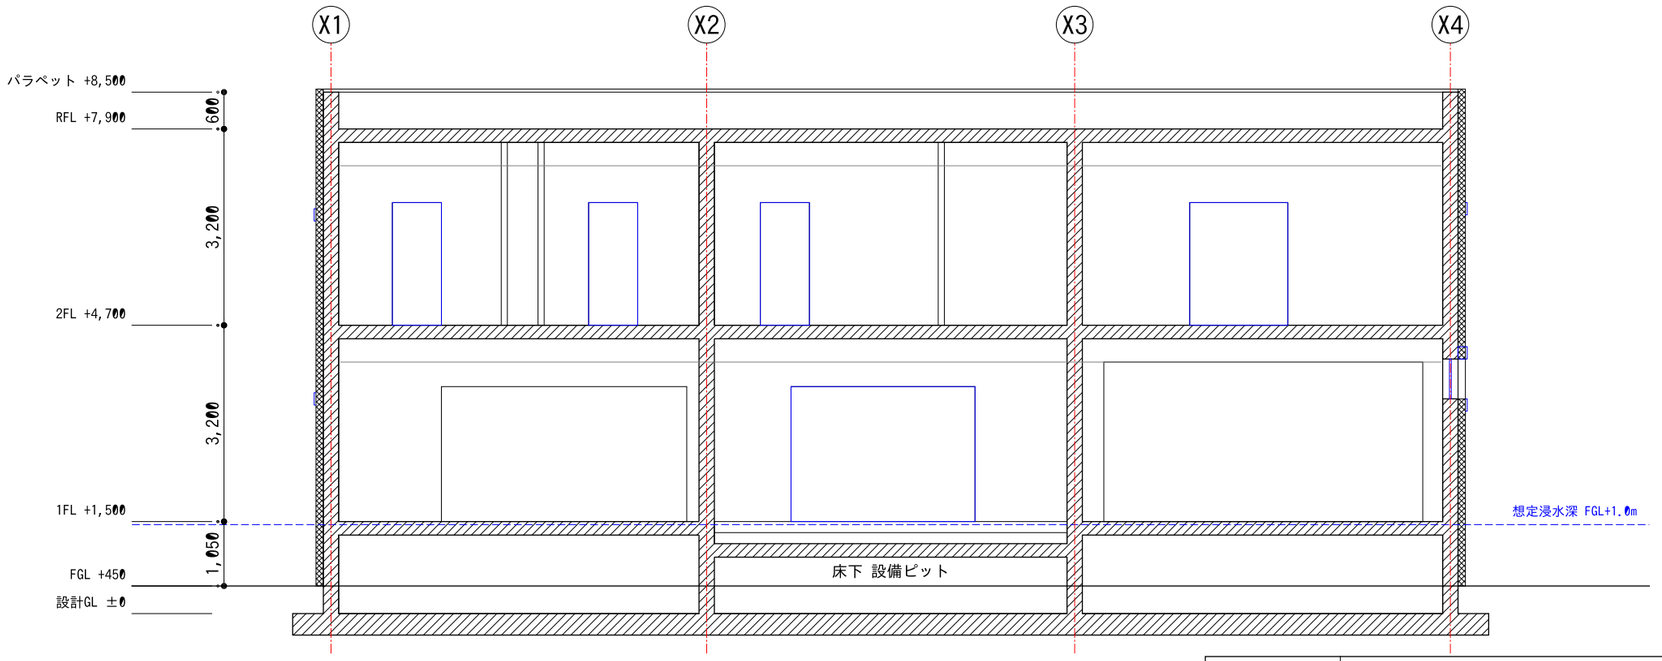


## 特記

階高 3,200×2／スラブ t=220／壁 RC t=250

天井高 CH=2,600（破線）。天井懐にダクト・浮き床

1FL=GL+1,500: 想定浸水深(FGL+1.0m)より上

基礎: べた基礎 t=350＋地中梁（RC壁を基礎まで連続）

階段: 蹴上 177.8 × 18段、踏面 240、有効幅 950（令23条 住宅）

| | | | | |
|---|---|---|---|---|
| 工事名称 | 河沿要（仮称）新築計画 | | | |
| 図面名称 | 断面図（建物） | | | 図番 A-07 |
| 縮尺 | A3　1:100 | 日付　2026-10-03 | 設計　設計検討（仮） | |
| 段階 | 基本計画　／　本図は建築基準法令に基づく計画段階の検討図であり、確認申請・構造計算・関係機関協議により確定する | | | |

## 地形（DEM5A）

敷地 TP+109.3〜109.6（ほぼ平坦）

北側道路 TP+112.5〜113.0（敷地より約3.2m高い）

東側道路 TP+109.0→112.9（北へ上り）

→ 敷地は北・東からの表流水が集まる低い側。RC塀下部の止水と排水で対応

がけ（高さ2m超）からの離れ：北 約11.1m ≧ 2H=6.4m、東 約9.4m ≧ 2H=6.6m（東京都建築安全条例6条）

## 南北断面（建物中央 X2-X3間）（縦横同縮尺）

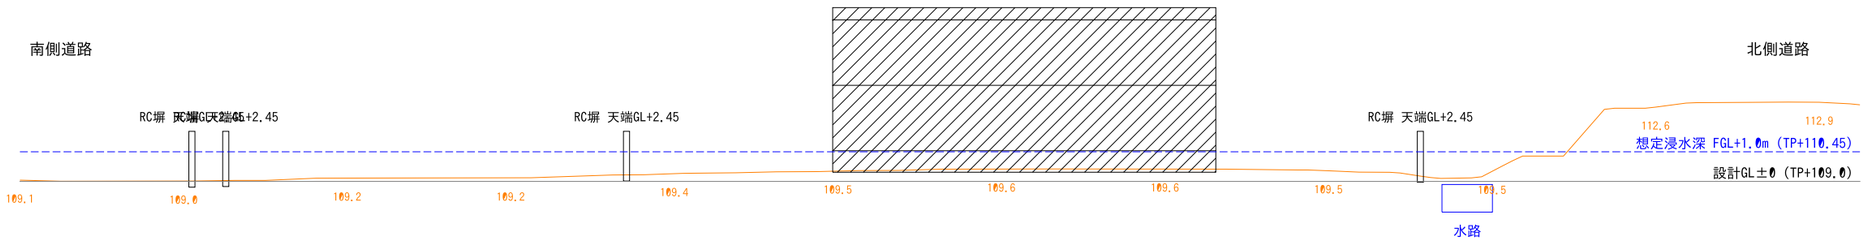


## 東西断面（建物中央 Y2-Y3間）（縦横同縮尺）

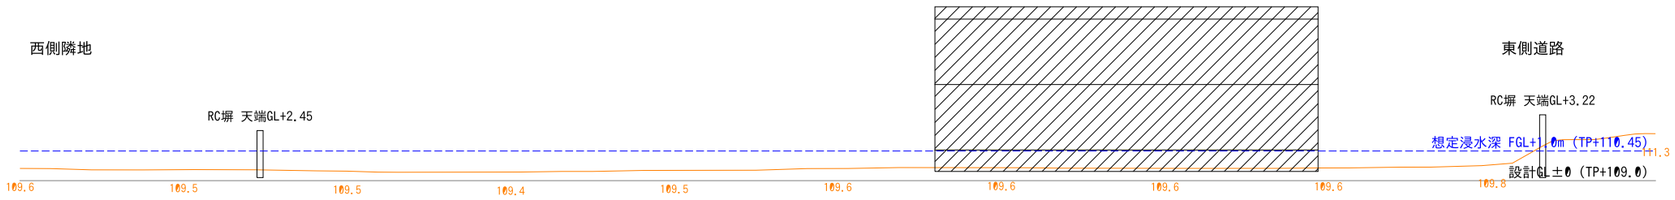


| | | | | |
|---|---|---|---|---|
| 工事名称 | 河沿要（仮称）新築計画 | | | |
| 図面名称 | 敷地断面図（地形・浸水） | | | 図番 A-08 |
| 縮尺 | A3　1:300 | 日付　2026-10-03 | 設計　設計検討（仮） | |
| 段階 | 基本計画　／　本図は建築基準法令に基づく計画段階の検討図であり、確認申請・構造計算・関係機関協議により確定する | | | |

## AW-1

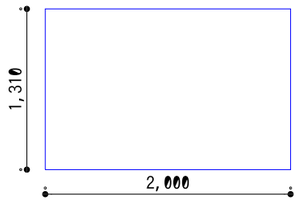


名称：FIX窓（LDK）
材質：樹脂（アルミ樹脂複合）
W2,000×H1,310
数量：1か所（1F）
ガラス：Low-E トリプル＋UVカット防犯合わせ（CP）・FIX

## AW-2

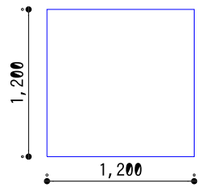


名称：FIX窓（LDK）
材質：樹脂（アルミ樹脂複合）
W1,200×H1,200
数量：1か所（1F）
ガラス：Low-E トリプル＋UVカット防犯合わせ（CP）・FIX

## AW-3

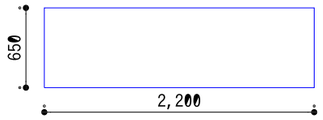


名称：FIX高窓（ジム）
材質：樹脂（アルミ樹脂複合）
W2,200×H650
数量：2か所（1F）
ガラス：Low-E トリプル＋UVカット防犯合わせ（CP）・FIX

## AW-4

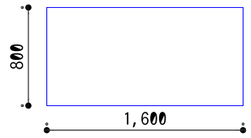


名称：FIX窓（居室）
材質：樹脂（アルミ樹脂複合）
W1,600×H800
数量：1か所（2F）
ガラス：Low-E トリプル＋UVカット防犯合わせ（CP）・FIX

## AW-5

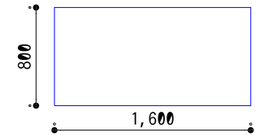


名称：FIX窓（主寝室）
材質：樹脂（アルミ樹脂複合）
W1,600×H800
数量：1か所（2F）
ガラス：Low-E トリプル＋UVカット防犯合わせ（CP）・FIX

## AW-6

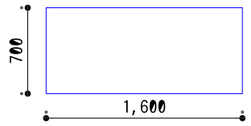


名称：FIX窓（図書室）
材質：樹脂（アルミ樹脂複合）
W1,600×H700
数量：1か所（2F）
ガラス：Low-E トリプル＋UVカット防犯合わせ（CP）・FIX

## AW-7

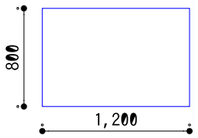


名称：FIX窓（居室）
材質：樹脂（アルミ樹脂複合）
W1,200×H800
数量：1か所（1F）
ガラス：Low-E トリプル＋UVカット防犯合わせ（CP）・FIX

## AW-8

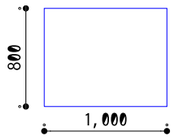


名称：FIX窓（主寝室）
材質：樹脂（アルミ樹脂複合）
W1,000×H800
数量：1か所（2F）
ガラス：Low-E トリプル＋UVカット防犯合わせ（CP）・FIX

## AW-9

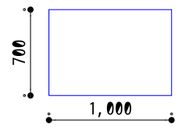


名称：FIX窓（居室）
材質：樹脂（アルミ樹脂複合）
W1,000×H700
数量：2か所（2F）
ガラス：Low-E トリプル＋UVカット防犯合わせ（CP）・FIX

## AW-10

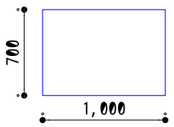


名称：FIX窓（図書室）
材質：樹脂（アルミ樹脂複合）
W1,000×H700
数量：1か所（2F）
ガラス：Low-E トリプル＋UVカット防犯合わせ（CP）・FIX

## GD-1

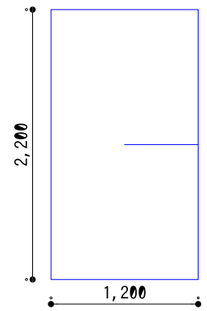


名称：ガラス上吊り引戸（合わせ強化）
材質：アルミ框・合わせ強化ガラス
W1,200×H2,200
数量：1か所（1F）
ガラス：合わせ強化（強化5＋5、衝突防止の乳白帯2本）

## GD-2

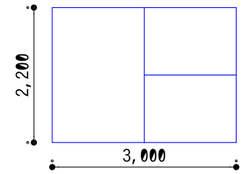


名称：ガラスFIX＋上吊り引戸（合わせ強化）
材質：アルミ框・合わせ強化ガラス
W3,000×H2,200
数量：1か所（1F）
ガラス：合わせ強化（強化5＋5、衝突防止の乳白帯2本）

姿図は W2,600 を超えるものを 1:100、その他を 1:50 で表示

## SD-1

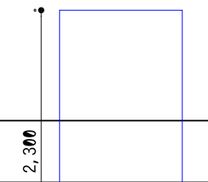


## SD-2

## SSD-1

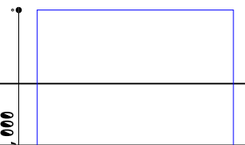


## SSD-2

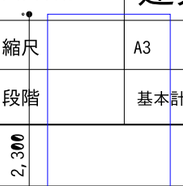


## SSD-3

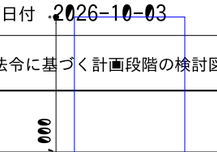


## WD-1

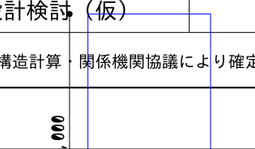


| | | | | |
|---|---|---|---|---|
| 工事名称 | 河沿要（仮称）新築計画 | | | |
| 図面名称 | 建具表 | | | 図番 A-09 |
| 縮尺 | A3 1:50・1:100 | 日付 2026-10-03 | 設計 設計検討（仮） | |
| 段階 | 基本計画 ／ 本図は建築基準法令に基づく計画段階の検討図であり、確認申請・構造計算・関係機関協議により確定する | | | |

# 開口部仕様・排煙計画（2階の窓仕様と排煙方式の検討、ジム開口部の改善）

## (1) 居室の窓と採光（㎡）

| 階 | 居室 | 床面積 | 必要 15.29% | ガラス | 有効(K3.0) | 余裕 |
|---|---|---|---|---|---|---|
| 1F | LDK（キッチン含む） | 59.8 | 9.15 | 4.06 | 12.18 | 1.33倍 |
| 1F | ジム | 51.6 | 7.88 | 2.86 | 8.58 | 1.09倍 |
| 1F | 居室A | 17.3 | 2.65 | 0.96 | 2.88 | 1.09倍 |
| 2F | 居室B | 12.5 | 1.91 | 0.70 | 2.10 | 1.10倍 |
| 2F | 居室C | 11.9 | 1.82 | 0.70 | 2.10 | 1.15倍 |
| 2F | 居室D | 17.1 | 2.61 | 1.28 | 3.84 | 1.47倍 |
| 2F | 図書室 | 33.8 | 5.17 | 1.82 | 5.46 | 1.06倍 |
| 2F | 主寝室 | 34.5 | 5.28 | 2.08 | 6.24 | 1.18倍 |

## (2) 排煙計画（令126条の2・3）

| 階 | 防煙区画（居室） | 面積 | 方式 | 系統 | 排煙口→最遠 | 参考:自然排煙の必要開放 |
|---|---|---|---|---|---|---|
| 1F | LDK（キッチン含む） | 59.8 | 機械排煙 | 西系統 | 4.2m | 1.20㎡ |
| 1F | ジム | 51.6 | 機械排煙 | 東系統 | 5.3m | 1.03㎡ |
| 1F | 居室A | 17.3 | 機械排煙 | 東系統 | 3.0m | 0.35㎡ |
| 2F | 居室B | 12.5 | 機械排煙 | 西系統 | 2.7m | 0.25㎡ |
| 2F | 居室C | 11.9 | 機械排煙 | 西系統 | 2.7m | 0.24㎡ |
| 2F | 居室D | 17.1 | 機械排煙 | 西系統 | 3.0m | 0.34㎡ |
| 2F | 図書室 | 33.8 | 機械排煙 | 西系統 | 4.1m | 0.68㎡ |
| 2F | 主寝室 | 34.5 | 機械排煙 | 東系統 | 4.2m | 0.69㎡ |

| 系統 | 区画数 | 最大区画 | 必要能力 | 計画 |
|---|---|---|---|---|
| 東系統 | 3 | 51.6㎡ | 120㎥/分 | 120㎥/分×1台 |
| 西系統 | 5 | 59.8㎡ | 120㎥/分 | 120㎥/分×1台 |

## (3) 2階の排煙方式の比較

| 比較項目 | A 機械排煙（採用） | B 自然排煙（高窓の一部を開閉式） |
|---|---|---|
| 窓 | 全室 FIX のまま | 各室に内倒し窓（天井下80cm以内、床面積1/50以上） |
| 防犯 | 開閉部なし（侵入経路にならない） | 開閉部が増え、2階でも足場があれば弱点 |
| 気密・断熱 | サッシ開閉部の隙間なし | 開閉部の気密・熱貫流が劣る（Uw 約+0.2） |
| 設備 | 排煙機・ダクト・予備電源（1階と共用） | 手動開放装置のみ（設備は少ない） |
| 維持管理 | 年1回の作動点検 | 開閉装置の点検・雨仕舞 |
| 判定 | 防犯・断熱・FIX方針と整合 → 採用 | 不採用 |

## (4) ジム開口部の改善（防犯・熱貫流）

| 項目 | 改善前（v3.1） | 改善後（v3.2） |
|---|---|---|
| 窓 | 腰高窓 1.5×1.0m ×2（窓台 FL+1,000） | FIX 高窓 2.1×0.6m ×2（窓台 FL+2,000） |
| 外部扉 | 南面 両開き搬入扉 1.8×2.4m | 廃止（搬入は玄関から） |
| 開口面積 | 7.32 ㎡ | 2.86 ㎡ |
| 開口まわり熱損失 | 9.2 W/K | 3.6 W/K（61%減） |
| 防犯 | 外部から手の届く窓・扉 | 窓下端 地盤+3.05m・防犯合わせガラス（CP、耐貫通5分以上）・開閉部なし |
| 採光 | 9.00 ㎡（有効） | 8.58 ㎡（必要 7.88） |

## 窓の仕様（全窓 FIX）

枠: 樹脂サッシ、ガラス: 全窓 Low-E トリプル（アルゴン）＋室外側 UVカット合わせガラス（紫外線約99%カット）、Uw≦0.90 W/㎡K。南・東・西は外付け電動スクリーン（M-03）

全窓（1・2階）: 外側を防犯合わせガラス（CP 認定品）。窓台: 居室 FL+1,000、ジム FL+2,000

換気は全館空調・全熱交換（窓に依存しない）。排煙時は機械室の給気ダンパーが連動して開く

玄関ホールの透明扉 GD-1・GD-2（合わせ強化ガラス上吊り引戸）の上、およびキッチン⇔ホールの開口の上に不燃の欄間パネル100（FL+2,100〜2,200）を足し、防煙垂れ壁500を確保する（要確認）

排煙機: 西・東系統の各機械室に 120㎥/分×1台。排煙口は各居室の天井、手動開放装置は床から0.8〜1.5m。予備電源は蓄電池（駐車場PV と連携、30分以上）

| | | | | |
|---|---|---|---|---|
| 工事名称 | 河沿要（仮称）新築計画 | | | |
| 図面名称 | 開口部仕様・排煙計画 | | | 図番 A-10 |
| 縮尺 | A3 ー | 日付 2026-10-03 | 設計 設計検討（仮） | |
| 段階 | 基本計画 ／ 本図は建築基準法令に基づく計画段階の検討図であり、確認申請・構造計算・関係機関協議により確定する | | | |

# 法規チェックリスト（建築基準法・同施行令・関連法令／設計仕様書）

| 区分 | 項目 | 根拠条文 | 規定・要求 | 計画 | 判定 |
|---|---|---|---|---|---|
| ブリーフ | 敷地面積 | ブリーフv3 1章 | 地図・航空写真・DEMによる推定 | 2,629.64㎡（推定誤差 ±5%程度） | 要確認 |
| ブリーフ | 建物外寸・グリッド | ブリーフv3 5章 | 内寸17.0m角、6.0/5.0/6.0、RC250＋外断熱120 | 壁芯 18.250m角、外寸 18.74m角 | 適合 |
| ブリーフ | 1階床高 | ブリーフv3 3章 | 想定浸水深（FGL+1.0m）より上 | 1FL GL+1,500（FGL+1,050） | 適合 |
| ブリーフ | ジムの広さ | 施主指示（v3.1） | 従前 34.5㎡ の1.3倍 | 51.6㎡（1.49倍） | 適合 |
| ブリーフ | ジムの搬入 | 施主指示（v3.3） | 玄関から搬入、框を上がって右折でジム | 外部階段（4段）→玄関 W1,000×H2,300→土間→二重框→ホールで右折→遮音ドア W1,000×H2,300→ジム。幅1m超の機器は分解して搬入 | 適合 |
| 構造 | ジム床の積載荷重 | 令85条（実況による） | 商業ジム相当の機器＋利用者 | 機器 計2,545kg（平均 484N/㎡）→ 設計用 5,000N/㎡（提案）・浮き床・落下エリア補強 | 要確認 |
| ブリーフ | ジム開口部の防犯・断熱 | 施主指示（v3.2） | 腰高窓・外部扉を弱点として改善 | 外部扉を廃止、窓は FIX 高窓（窓台FL+2,000）防犯合わせガラス。開口 7.3→2.9㎡、開口まわりの熱損失 9.2→3.6 W/K | 適合 |
| ブリーフ | 太陽光発電（本館と分離した屋根付き設備） | 施主指示（v4.1・v4.2） | 年間電力需要 約200,859kWh ×1.2 を賄う → 23.8kWp | ソーラーパーゴラ 27.1kWp＋3台用カーポート 10.2kWp（影損失込み）→ 年 約38,805kWh | 適合 |
| ブリーフ | 玄関の目隠し | 施主指示（v4.3） | 南側道路から目視で玄関ドアが見えない | 南側道路沿い17地点から判定: 壁なし 7地点で見える → 自立壁 L4.0m×H2.7m で 0地点（目線1.5m）／17地点（4.5m） | 適合 |
| ブリーフ | 室内環境目標 | 施主指示（v4.1） | 全室 通年 湿度55〜60%、夏25〜26℃、冬20〜21℃ | 全館空調2系統＋全熱交換＋デシカント調湿。暖房 9.0kW・冷房 11.7kW・除湿 74L/日・加湿 63L/日 | 適合 |
| 集団規定 | 建ぺい率（パーゴラ・カーポート含む） | 法53条・法2条1号 | 屋根と柱をもつ架台は建築物として扱う見込み | (333.06+パーゴラ180+カーポート54)/2,629.64 = 21.55% | 適合 |
| ブリーフ | 蓄電池 | ブリーフv3 7章 | 排煙機30分＋排水ポンプ6時間＋最低限の生活24時間 | 必要 約15.7kWh → 16kWh 級 | 適合 |
| ブリーフ | 駐車台数 | ブリーフv3 2章 | 3台 | 3台（屋根なし・Dotcon+） | 適合 |
| ブリーフ | RC塀 | ブリーフv3 4章 | H2,000（防犯） | 全周 H2.0m 以上（東側坂道沿いは道路面+1.2m以上） | 適合 |
| ブリーフ | 透水性舗装 | ブリーフv3 3.1・施主指示（v4.9・v4.14） | Dotcon+ を施主の再配置図の位置に | 駐車場・アプローチ 約213㎡＋パーゴラ下・北・西・東の帯・日なたの菜園 約625㎡ = 約838㎡（一時貯留 約10.9㎥） | 適合 |
| ブリーフ | 建物の向き | 施主指示（v4.4） | 南側道路に対して平行・直交 | 建物・外構を道路境界線に合わせて 12.3° 回転（南面は真南から西向き） | 適合 |
| ブリーフ | 窓の仕様 | 施主指示（v4.5） | 全窓 Low-E ガラスのトリプルサッシ | 全12か所 樹脂サッシ（トリプルガラス対応・FIX）・Low-E トリプル（Ar・Low-E 2面）、Uw≦0.90。南北 日射取得型・東西 遮熱型 | 適合 |
| ブリーフ | インテリアの一貫方針 | 施主指示（v4.6） | 安全なデザイン、清掃・メンテナンスが簡易 | 危険10項目・手入れ9項目の対策を全室に適用（I-01）、仕上げを室の種類ごとに統一（I-02） | 適合 |
| 安全 | 階段1 の寸法 | 品確法 評価方法基準（高齢者等配慮 等級5相当） | 勾配≦6/7、550≦2R+T≦650、蹴込み≦30 | R177.8・T260・勾配0.68・2R+T=616、蹴込み板あり | 適合 |
| 安全 | 階段2 の寸法 | 品確法 評価方法基準（高齢者等配慮 等級5相当） | 勾配≦6/7、550≦2R+T≦650、蹴込み≦30 | R177.8・T240・勾配0.74・2R+T=596、蹴込み板あり | 適合 |
| 安全 | 階段開口の手すり壁（頭部・指の挟み込み） | 施主指示（v4.6） | H1,100以上、100〜230mm・8〜25mm のすき間なし | 手すり壁3か所 H1,100（パネル・手すり子なし）、端部は壁に接する。階段の間の壁は 2FL+1,100 まで連続 | 適合 |
| ブリーフ | 敷地境界・塀の再配置 | 施主指示（v4.14） | 北（水路の溝）と東（東側道路）から塀を内側へ寄せ、北東の角を除外 | 敷地 約2,630㎡（再配置前 2,772㎡）。塀は新しい境界の内側に沿わせる | 要確認 |
| ブリーフ | 門の後退・ゴミ収集ボックス | 施主指示（v4.8・v4.10） | 南側の門を約4m 後退。門の外にゴミ収集ボックス（西の角）、道路から見えない | 門の線を道路境界から4.0m 後退。ボックス W800×D1,600×H1,200 を門の外・西の角に置き、南に自立壁（X12.2m まで）＋袖壁0.6m（H1,800）。南側・東側道路 158地点（目の高さ1.5m・門扉閉）のうち、南東の角の7地点から一部（判定点16のうち最大5点）が見える（施主了承: わずかに見える分は可） | 適合 |
| ブリーフ | 勝手口 | 施主指示（v4.10） | 防犯性能を下げるため廃止 | 出入口は南の人用門扉・車両門扉の2か所のみ（門扉 2か所） | 適合 |
| ブリーフ | 車両盗難対策 | 施主指示（v4.10） | 車両の盗難を防ぐ | 電動スライド門扉（施錠・こじ開け検知）＋内側の電動昇降ボラード3本、前向き駐車、電波遮断キーボックス（リレーアタック対策）、赤外線カメラ・ビームセンサー → bot 通知 | 適合 |
| ブリーフ | 寝室の空気（1部屋1人） | 施主指示（v4.13） | 就寝中の CO2 800ppm 以下 | 居室A 800ppm・居室B 800ppm・居室C 800ppm・居室D 800ppm・主寝室 732ppm（CO2 センサーで換気量を自動調整、冷暖房増 年約149kWh） | 適合 |
| ブリーフ | 菜園（プランター） | 施主指示（v4.13） | 家庭菜園で育つ野菜をプランターで。床（基礎）の劣化を抑える | 日なたのプランター菜園 植付21.6㎡（影損失 年2.1%）を Dotcon+ の上に脚付きで設置。パーゴラ下は半日陰の作物 | 適合 |
| ブリーフ | 強盗（闇バイト型）対策 | 施主指示（v4.12） | 侵入・押し入り強盗への対策強化 | 手口9項目を評価し対策を追加（S-04）: 門のインターホンと貫通型宅配ボックス、忍び返し、全窓 CP 防犯合わせ、玄関 CP 防犯扉・2ロック、非常ボタン・機械警備・LTE 予備回線、2階 WIC（主寝室） を避難室に | 適合 |
| ブリーフ | 駐車場の位置 | 施主指示（v4.8） | 約8m 北へ | カーポートを 8.0m 北へ（建物南面から 13.1m、門から 8.2m の前面通路）。アプローチはカーポートの西を通す | 適合 |
| ブリーフ | 家具の転倒防止 | 施主指示（v4.7） | RC 壁に固定しない。突っ張り・家具の構造で耐震・転倒耐性 | 背の高い収納・本棚は床・天井の突っ張り（天井下地補強）＋幅広の脚・背面連結・低重心・耐震ラッチ。ジム機器は自重・広い脚で安定 | 適合 |
| ブリーフ | 床清掃（掃除ロボット） | 施主指示（v4.7） | 床清掃は可能な限りロボット（レールは可） | 1F 247㎡・2F 276㎡、段差5mm以下、各階にドック（自動ゴミ収集・給排水直結） | 適合 |

判定: 適合／要確認（条例・関係機関協議・別途計算による）／対象外。数値はすべて建物モデルから自動算定。

| | | | | |
|---|---|---|---|---|
| 工事名称 | 河沿要（仮称）新築計画 | | | |
| 図面名称 | 法規チェックリスト（1/3） | | | 図番 A-11 |
| 縮尺 | A3 ー | 日付 2026-10-03 | 設計 設計検討（仮） | |
| 段階 | 基本計画 ／ 本図は建築基準法令に基づく計画段階の検討図であり、確認申請・構造計算・関係機関協議により確定する | | | |

# 法規チェックリスト（建築基準法・同施行令・関連法令／設計仕様書）

| 区分 | 項目 | 根拠条文 | 規定・要求 | 計画 | 判定 |
|---|---|---|---|---|---|
| ブリーフ | 便器 | 施主指示（v4.7） | タンクレスにしない | 全トイレ タンク式便器（フチなし・防汚） | 適合 |
| ブリーフ | スクリーンの bot 制御 | 施主指示（v4.7） | 全館のスクリーンを bot から操作できる | 全11台 KNX/Matter 対応モーター→ゲートウェイのローカル API（認証付き）。強風・凍結時の安全動作が優先 | 適合 |
| ブリーフ | 照明（時刻で変化） | 施主指示（v4.7） | 時刻に応じて色温度と明るさが変わる LED | 全室 調光・調色 LED（2200〜5000K・10〜100%）を時刻スケジュールで制御（E-02） | 適合 |
| ブリーフ | Wi-Fi（1F） | 施主指示（v4.7） | 5GHz 受信 -67dBm 以上を床面の98%以上 | 天井 AP 6台（PoE 有線）→ 100%（概算、竣工時に実測） | 適合 |
| ブリーフ | Wi-Fi（2F） | 施主指示（v4.7） | 5GHz 受信 -67dBm 以上を床面の98%以上 | 天井 AP 6台（PoE 有線）→ 99%（概算、竣工時に実測） | 適合 |
| ブリーフ | 外構の防虫 | 施主指示（v4.7） | 敷地内で虫が発生・集中しない工夫 | 外構照明 12台を 2200K・下向き・人感センサー、日没後はスクリーンで光漏れ防止、たまり水をつくらない ほか9項目（E-03） | 適合 |
| ブリーフ | 紫外線対策 | 施主指示（v4.5） | 日照による紫外線をカットする設備 | 全窓 UVカット合わせガラス（紫外線透過率1%以下）＋南・東・西の窓11か所に外付け電動スクリーン（5〜9月 自動）→ 室内に入る紫外線 約0.6%（M-03） | 適合 |
| 集団規定 | 用途地域の制限 | 法48条・別表第2 | 準工業地域（推定・要確認）：住宅は建築可 | 一戸建ての住宅 | 要確認 |
| 集団規定 | 接道 | 法43条 | 道路に2m以上接する | 南側道路 約13.9m・東側道路 約81.8m | 適合 |
| 集団規定 | 建ぺい率 | 法53条 | 60%以下（角地緩和は不使用） | 333.06/2,629.64 = 12.67% | 適合 |
| 集団規定 | 容積率 | 法52条 | min(指定200%, 道路7.4m×0.6=444%) | 666.12/2,629.64 = 25.33% | 適合 |
| 集団規定 | 道路斜線（南） | 法56条1項1号・2項 | 勾配1.5、後退距離 31.3m による緩和 | 建物南面で許容 105.1m ≧ 高さ 8.50m | 適合 |
| 集団規定 | 道路斜線（東） | 法56条1項1号・2項 | 後退距離 10.0m（道路高さが敷地より高い区間は緩和あり） | 許容 38.3m ≧ 8.50m | 適合 |
| 集団規定 | 隣地斜線 | 法56条1項2号 | 31m＋2.5×L | 最高高さ 8.50m ＜ 31m | 適合 |
| 集団規定 | 北側斜線 | 法56条1項3号 | 低層・中高層住居専用地域等 | 準工業地域（推定） | 対象外 |
| 集団規定 | 日影規制 | 法56条の2・都条例 | 準工業：高さ10m超が対象（指定時） | 高さ 8.50m ≦ 10m | 適合 |
| 集団規定 | 防火地域等 | 法61条 | 指定未確認（耐火建築物で計画） | 壁式RC造（耐火構造）で計画 | 要確認 |
| 都条例 | がけ（北側） | 東京都建築安全条例6条 | 高さ2m超のがけ：下端から2H=6.4m 以上離す | 水路（がけ下端）まで 9.9m | 適合 |
| 都条例 | がけ（東側） | 東京都建築安全条例6条 | 道路との高低差 最大3.3m：2H=6.6m | 東側道路境界まで 10.0m | 適合 |
| 都条例 | 角敷地の隅切り | 東京都建築安全条例2条 | 幅員がいずれも6m未満の道路の角敷地 | 南側道路 約7.4m（6m以上） | 対象外 |
| 都条例 | 敷地と道路（大規模建築物） | 東京都建築安全条例4条 | 延べ1,000㎡超は接道長さの割増し | 延べ 666㎡ | 対象外 |
| 単体規定 | 採光 1F LDK（キッチン含む） | 法28条1項・令19条・20条 | 床面積 59.8㎡ × 15.29% = 9.15㎡（法定 1/7 = 8.55） | ガラス 4.06㎡ × K3.0 = 12.18㎡ | 適合 |
| 単体規定 | 採光 1F ジム | 法28条1項・令19条・20条 | 床面積 51.6㎡ × 15.29% = 7.88㎡（法定 1/7 = 7.36） | ガラス 2.86㎡ × K3.0 = 8.58㎡ | 適合 |
| 単体規定 | 採光 1F 居室A | 法28条1項・令19条・20条 | 床面積 17.3㎡ × 15.29% = 2.65㎡（法定 1/7 = 2.47） | ガラス 0.96㎡ × K3.0 = 2.88㎡ | 適合 |
| 単体規定 | 採光 2F 居室B | 法28条1項・令19条・20条 | 床面積 12.5㎡ × 15.29% = 1.91㎡（法定 1/7 = 1.79） | ガラス 0.70㎡ × K3.0 = 2.10㎡ | 適合 |
| 単体規定 | 採光 2F 居室C | 法28条1項・令19条・20条 | 床面積 11.9㎡ × 15.29% = 1.82㎡（法定 1/7 = 1.70） | ガラス 0.70㎡ × K3.0 = 2.10㎡ | 適合 |
| 単体規定 | 採光 2F 居室D | 法28条1項・令19条・20条 | 床面積 17.1㎡ × 15.29% = 2.61㎡（法定 1/7 = 2.44） | ガラス 1.28㎡ × K3.0 = 3.84㎡ | 適合 |
| 単体規定 | 採光 2F 図書室 | 法28条1項・令19条・20条 | 床面積 33.8㎡ × 15.29% = 5.17㎡（法定 1/7 = 4.83） | ガラス 1.82㎡ × K3.0 = 5.46㎡ | 適合 |
| 単体規定 | 採光 2F 主寝室 | 法28条1項・令19条・20条 | 床面積 34.5㎡ × 15.29% = 5.28㎡（法定 1/7 = 4.93） | ガラス 2.08㎡ × K3.0 = 6.24㎡ | 適合 |
| 単体規定 | 採光補正係数 | 令20条 | 準工業：K = 8d/h − 1（上限3.0） | 隣地・道路まで十分な距離 → 3.0（要確認） | 要確認 |
| 単体規定 | 換気 | 法28条2項・令20条の2 | 窓（1/20）または機械換気設備 | 全館空調・全熱交換換気（FIX窓に依存しない） | 適合 |
| 単体規定 | シックハウス（24時間換気） | 法28条の2・令20条の8 | 0.5回/h 以上 | 全熱交換換気で常時換気 | 適合 |
| 単体規定 | 居室の天井高 | 令21条 | 2.1m以上 | CH 2,600mm | 適合 |
| 単体規定 | 階段（住宅） | 令23条1項ただし書 | 幅750以上・蹴上230以下・踏面150以上 | 幅1150・蹴上177.8・踏面260（2か所） | 適合 |
| 単体規定 | 踊場・手すり | 令24条・25条 | 高さ4m以内ごとに踊場、手すり設置 | 中間踊場（高さ 1.6m）・手すり設置 | 適合 |

判定：適合／要確認（条例・関係機関協議・別途計算による）／対象外。数値はすべて建物モデルから自動算定。

| | | | | |
|---|---|---|---|---|
| 工事名称 | 河沿要（仮称）新築計画 | | | |
| 図面名称 | 法規チェックリスト（2/3） | | | 図番 A-12 |
| 縮尺 | A3 ー | 日付 2026-10-03 | 設計 設計検討（仮） | |
| 段階 | 基本計画 ／ 本図は建築基準法令に基づく計画段階の検討図であり、確認申請・構造計算・関係機関協議により確定する | | | |

# 法規チェックリスト（建築基準法・同施行令・関連法令／設計仕様書）

| 区分 | 項目 | 根拠条文 | 規定・要求 | 計画 | 判定 |
|---|---|---|---|---|---|
| 単体規定 | 排煙（1階） | 令126条の2・3 | FIX窓の居室は「排煙上の無窓居室」→ 排煙設備 | LDK・ジム・居室A: 機械排煙（機械室の排煙機） | 適合 |
| 単体規定 | 排煙（2階） | 令126条の2・3 | 2階居室も FIX 窓 → 排煙上の無窓居室 | 居室B・C・D・図書室・主寝室: 機械排煙（1階と同じ方式） | 適合 |
| 単体規定 | 排煙機 能力（東系統） | 令126条の3第1項9号 | 120m³/分以上かつ 最大区画 51.6m²×2 = 103m³/分以上（3区画） | 排煙機 120m³/分（機械室） | 適合 |
| 単体規定 | 排煙機 能力（西系統） | 令126条の3第1項9号 | 120m³/分以上かつ 最大区画 59.8m²×2 = 120m³/分以上（5区画） | 排煙機 120m³/分（機械室） | 適合 |
| 単体規定 | 排煙口の位置 | 令126条の3第1項3号 | 防煙区画の各部分から水平距離30m以下・天井から80cm以内 | 各室の天井に排煙口、最遠 約5.3m | 適合 |
| 単体規定 | 防煙垂れ壁（LDK⇔ホール・キッチン⇔ホール） | 令126条の2第1項 | 防煙壁: 間仕切壁または天井から50cm以上下方に突き出した不燃の垂れ壁 | 開口 H2,200（天井2,600）のため垂れ壁400 → 開口上に不燃の欄間パネル100を足して垂れ壁500を確保（透明扉は防煙壁に数えない）。審査機関に確認 | 要確認 |
| 単体規定 | 排煙の予備電源・手動開放 | 令126条の3第1項5号・11号 | 手動開放装置（床から0.8〜1.5m）・予備電源 | 各室に手動開放装置、蓄電池（駐車場PV と連携）を予備電源に兼用 | 適合 |
| 単体規定 | 内装制限（火気使用室） | 法35条の2・令128条の4第4項 | 2階建て住宅の1階で火気を使う室 | IHクッキングヒーターなら対象外。ガス採用時は準不燃 | 要確認 |
| 単体規定 | 非常用の照明 | 令126条の4 | 一戸建ての住宅は除外 | — | 対象外 |
| 構造 | 壁量 1F X方向 | 平13国交告1026号 第5 | 12cm/m²以上（地上2階建て） | 耐力壁 55.4m / 床 333.1m² = 16.6cm/m² | 適合 |
| 構造 | 壁量 1F Y方向 | 平13国交告1026号 第5 | 12cm/m²以上（地上2階建て） | 耐力壁 59.6m / 床 333.1m² = 17.9cm/m² | 適合 |
| 構造 | 壁量 2F X方向 | 平13国交告1026号 第5 | 12cm/m²以上（地上2階建て） | 耐力壁 61.9m / 床 333.1m² = 18.6cm/m² | 適合 |
| 構造 | 壁量 2F Y方向 | 平13国交告1026号 第5 | 12cm/m²以上（地上2階建て） | 耐力壁 63.5m / 床 333.1m² = 19.1cm/m² | 適合 |
| 構造 | 耐力壁の厚さ | 平13国交告1026号 第5 | 2階建て 15cm以上 | 25cm | 適合 |
| 構造 | 耐力壁で囲まれた面積 | 平13国交告1026号 第5 | 60m²以下 | 最大 37.5m² | 適合 |
| 構造 | 階高・軒高・階数 | 平13国交告1026号 第1 | 階高3.5m以下・軒高20m以下・階数5以下 | 階高3.2m・軒高7.9m・2階 | 適合 |
| 構造 | コンクリート強度 | 平13国交告1026号 第2・令74条 | Fc18以上 | Fc24 | 適合 |
| 構造 | 床版の厚さ | 令77条の2・告示1026号 | 8cm以上かつ短辺内法/40 = 147mm | t=220（短辺 内法 5.88m） | 適合 |
| 構造 | 床版のたわみ（ジム床含む） | 日本建築学会 RC規準（参考） | 必要厚 最大 193mm（ジム床 積載5kN/m²） | t=220 | 適合 |
| 構造 | 地震力に対する壁のせん断（概算） | 令88条・告示1026号（参考） | Co=0.2（等級3: 0.3）、短期許容せん断 1.09N/mm² | 最小余裕 1F X方向: τ=0.20N/mm²（等級3）→ 5.5倍 | 適合 |
| 構造 | 偏心率 | 令82条の6（参考） | 0.15以下 | 最大 0.105（1階 ジムの開口による） | 適合 |
| 構造 | 保有水平耐力（目安） | 令82条の3（参考） | Qu ≧ Qun（Ds=0.55） | 最小 Qu/Qun = 5.5 | 適合 |
| 構造 | 地盤の接地圧（長期） | 令93条 | 長期許容支持力度 150kN/m²（要地盤調査） | 41.8kN/m² | 適合 |
| 構造 | かぶり厚さ | 令79条 | 壁・床20（耐力壁30）／土に接する40／基礎60 | 設計かぶり 壁40・床30・土に接する50・基礎70 | 適合 |
| 構造 | 構造計算 | 法20条1項3号 | 壁式RC 2階建て（延べ200m²超）→ 構造計算（許容応力度等） | 別途 構造計算書 | 要確認 |
| 構造 | 地盤・基礎 | 令38条 | 地盤調査に基づく基礎 | べた基礎（杭の要否は調査後） | 要確認 |
| 外構 | RC塀 | 令62条の8（補強CB造） | RC塀は対象外 → 構造計算で同等以上の安全確認 | H2.0m t=150 基礎1,200×400 | 要確認 |
| 外構 | 擁壁を兼ねる塀 | 法88条・令138条 | 高さ2m超の擁壁は工作物確認申請 | 東側坂道沿いで道路との段差を受ける区間が該当する可能性 | 要確認 |
| 外構 | 水路の占用・境界 | 法定外公共物管理条例（八王子市） | 境界確定・占用協議 | 北側の塀・排水口の位置を協議 | 要確認 |
| 関連法令 | 建築物省エネ法 | 建築物省エネ法 10条（住宅の適合義務） | 地域区分6: 外皮 UA 0.87以下 ほか | UA 0.25〜0.29（ブリーフ） | 適合 |
| 関連法令 | 宅地造成・盛土等規制法 | 同法 | 規制区域内の切土・盛土 | 切土・盛土なし（現況地盤を維持） | 適合 |
| 関連法令 | 雨水浸透 | 八王子市 雨水浸透施設の指導・助成 | 設置基準・補助の確認 | 貯留槽25m³・Dotcon+ 透水舗装・浸透桝 | 要確認 |

判定: 適合／要確認（条例・関係機関協議・別途計算による）／対象外。数値はすべて建物モデルから自動算定。

| | | | | |
|---|---|---|---|---|
| 工事名称 | 河沿要（仮称）新築計画 | | | |
| 図面名称 | 法規チェックリスト（3/3） | | | 図番 A-13 |
| 縮尺 | A3 ー | 日付 2026-10-03 | 設計 設計検討（仮） | |
| 段階 | 基本計画 ／ 本図は建築基準法令に基づく計画段階の検討図であり、確認申請・構造計算・関係機関協議により確定する | | | |

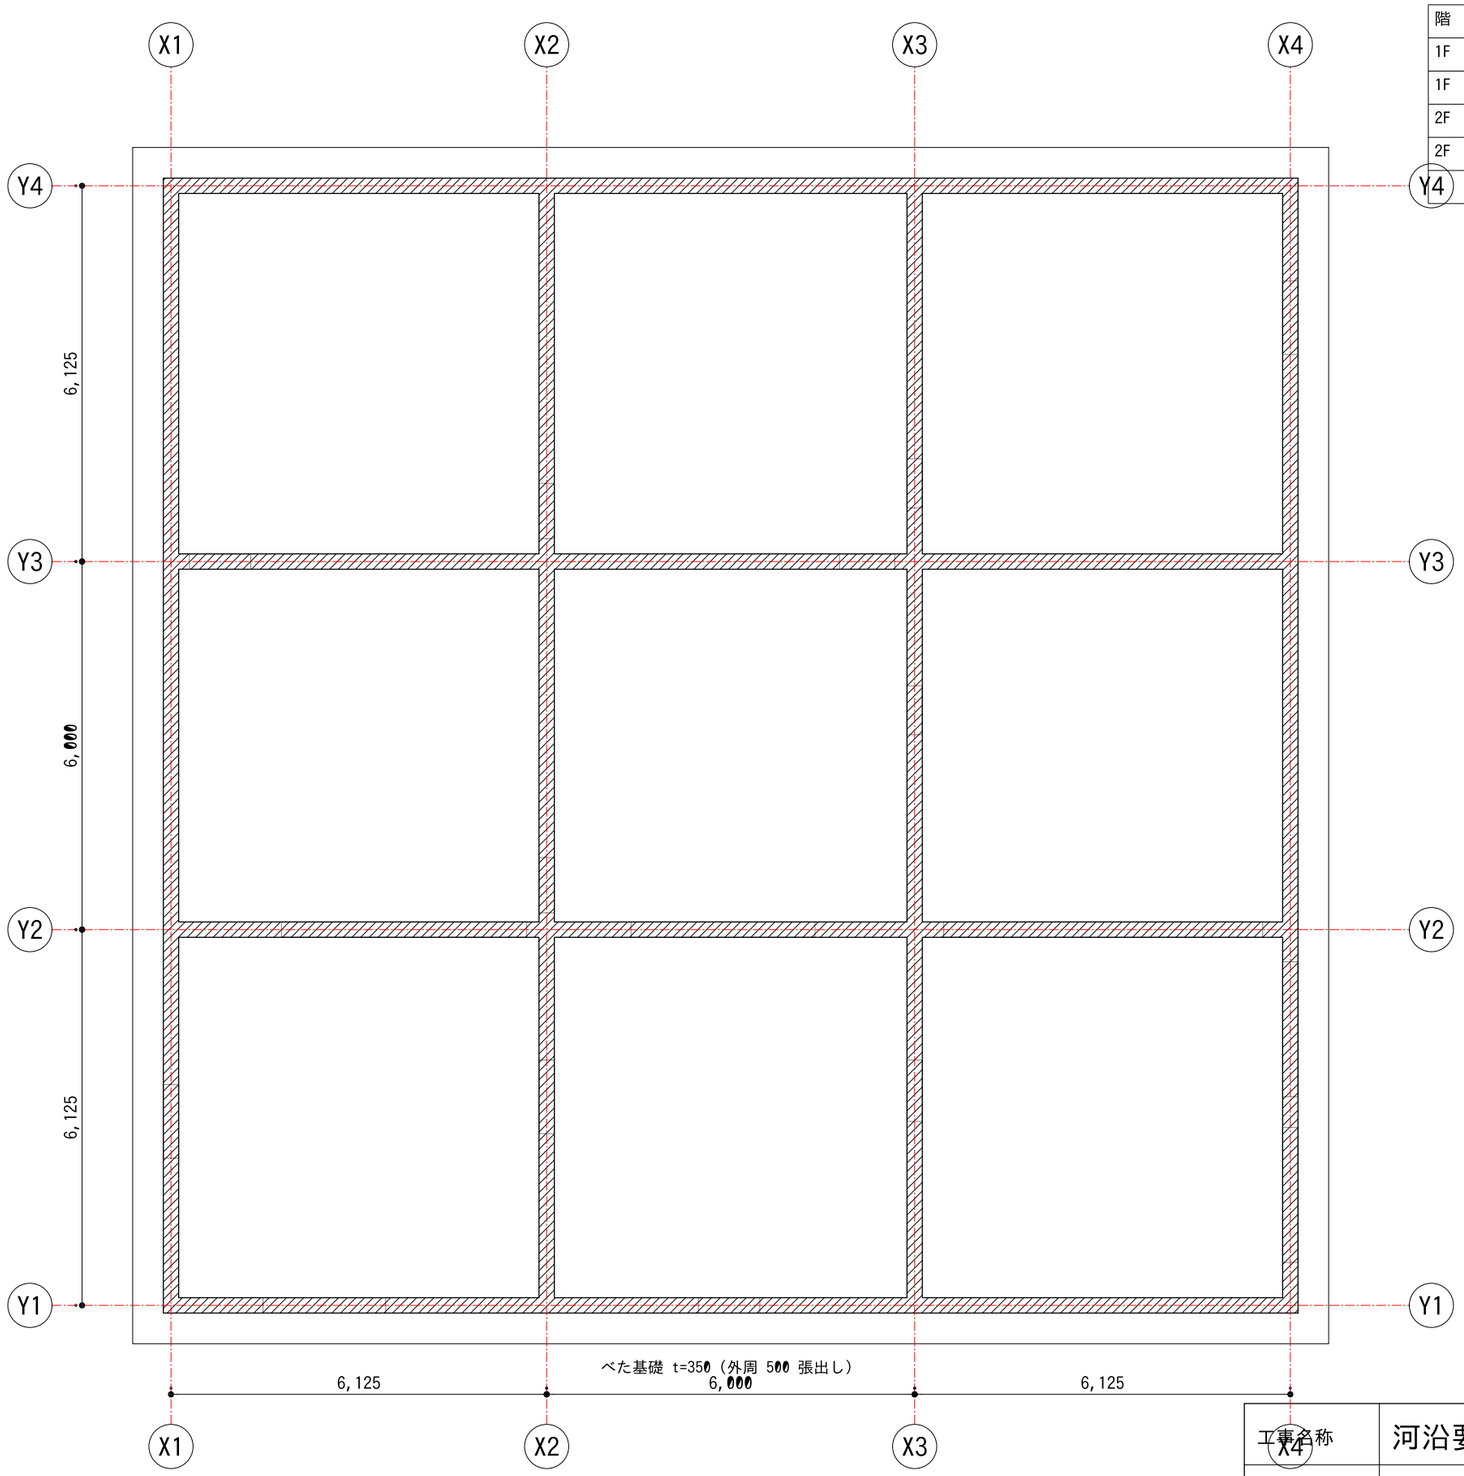


## 基礎伏図・耐力壁配置図（1階） S=1:100

網掛け=RC耐力壁 t=250（1・2階 同位置）、破線=開口

### 壁量・壁式構造の規定（平13国交告1026号）

| 階 | 方向 | 耐力壁長さ | 壁量 | 判定 |
|---|---|---|---|---|
| 1F | X方向 | 55.4 m | 16.6 cm/m² | ≧12 適合 |
| 1F | Y方向 | 59.6 m | 17.9 cm/m² | ≧12 適合 |
| 2F | X方向 | 61.9 m | 18.6 cm/m² | ≧12 適合 |
| 2F | Y方向 | 63.5 m | 19.1 cm/m² | ≧12 適合 |
| | | 壁厚 | 25 cm | ≧15 適合 |

| | | | | |
|---|---|---|---|---|
| 工事名称 | 河沿要（仮称）新築計画 | | | |
| 図面名称 | 基礎伏図・耐力壁配置図 | | | 図番 S-01 |
| 縮尺 | A3 1:100 | 日付 2026-10-03 | 設計 設計検討（仮） | |
| 段階 | 基本計画 ／ 本図は建築基準法令に基づく計画段階の検討図であり、確認申請・構造計算・関係機関協議により確定する | | | |

## (4) 車両門扉部 着脱式止水板 H600（立面）S=1:30

車両門扉 W5,000・人用 W1,200（勝手口なし）。止水板は門扉の近くに保管

## 特記

RC塀は令62条の8（補強コンクリートブロック造の塀）の対象外。風圧力・地震力に対する構造計算で安全を確認する

東側の坂道沿いで塀が道路との高低差（2m超）を受ける区間は、擁壁として工作物確認申請の対象（令138条）

塀は境界の内側に設置。北側は水路の管理境界との協議に従う

玄関前の目隠し壁（L4.4m・H2.7m・t180）は(1)と同じ断面の自立壁とし、本館・ポーチとは基礎から縁を切る（離隔1.5m以上）。単体で補修・更新・撤去ができる

雨水浸透施設は、地盤調査（透水係数・地下水位）と八王子市の指導・助成制度を確認して決定

## (1) RC塀 断面 S=1:30

壁 t=150 縦横 D10@200 ダブル／基礎 1,200×400・根入れ 900
天端に笠木・侵入防止金物、打継ぎ部に止水板

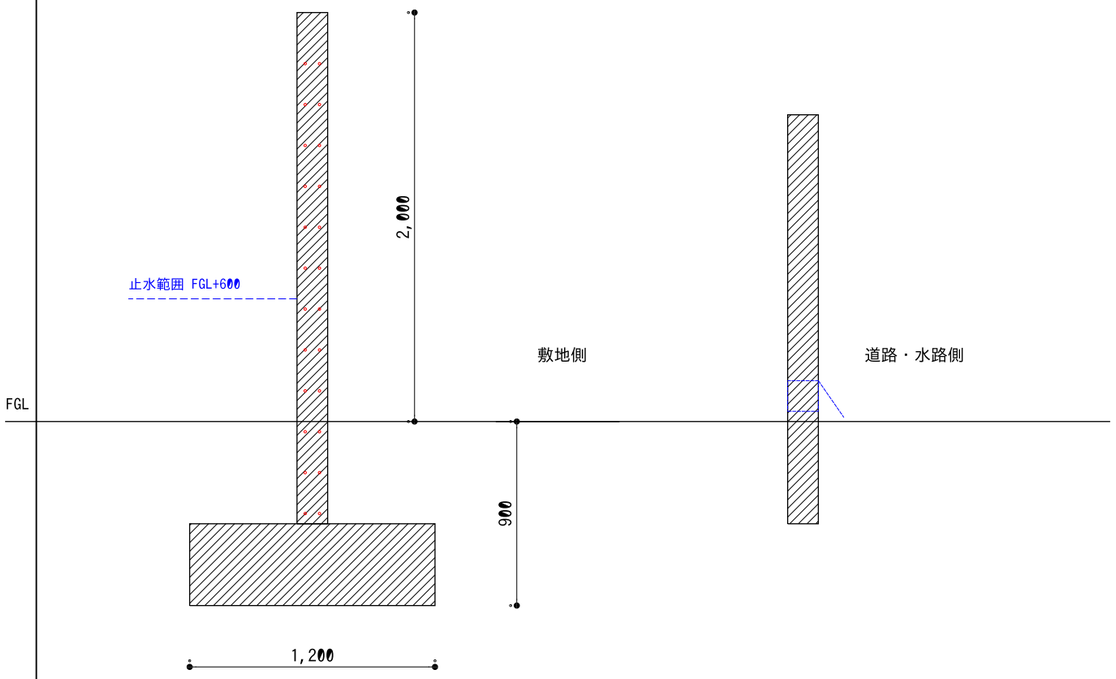


## (2) 排水口 □150＋フラップ弁 S=1:30

外側からの逆流を防ぐ。点検・清掃が可能な位置に設置

## (3) 透水舗装（駐車場）断面 S=1:30

一時貯留 約13L/m²。車両荷重に応じた製品仕様を確認

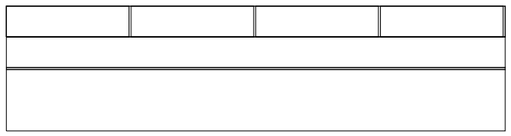

Dotcon+ 600角 t=150（目地10mm から浸透）
砕石路盤 t=150（単粒度砕石）
透水シート
路床（現況土・透水試験で確認）

| | | | | |
|---|---|---|---|---|
| 工事名称 | 河沿要（仮称）新築計画 | | | |
| 図面名称 | RC塀・止水・透水舗装 詳細図 | | | 図番 S-02 |
| 縮尺 | A3　1:30 | 日付　2026-10-03 | 設計　設計検討（仮） | |
| 段階 | 基本計画　／　本図は建築基準法令に基づく計画段階の検討図であり、確認申請・構造計算・関係機関協議により確定する | | | |

# 耐震検討（壁式鉄筋コンクリート造・概算）— B案 構造グリッド 6.125 / 6.0 / 6.125

## (1) 地震力の算定

| 項目 | 値 |
|---|---|
| R階 重量 W2 | 3,939 kN |
| 2階 重量 W1 | 5,245 kN |
| 建物重量 ΣW | 9,184 kN（単位床面積あたり 13.8 kN/m²） |
| 固有周期 T | 0.128 s（Rt=1.0、Z=1.0） |
| 2階の Ai | 1.203（α=0.429） |
| 短期許容せん断応力度 fs | 1.09 N/mm²（Fc24） |
| 接地圧（長期） | 41.8 kN/m²（基礎面積 380m²、許容150） |

## (2) 層せん断力と壁のせん断応力度

| 階・方向 | 壁長 m | 壁量 cm/m² | Q（Co0.2）kN | τ N/mm² | 余裕 | Q（等級3）kN | τ | 余裕 | Qu/Qun | 偏心率 |
|---|---|---|---|---|---|---|---|---|---|---|
| 1F X方向 | 55.4 | 16.6 | 1,837 | 0.133 | 8.3 | 2,755 | 0.199 | 5.5 | 5.5 | 0.105 |
| 1F Y方向 | 59.6 | 17.9 | 1,837 | 0.123 | 8.9 | 2,755 | 0.185 | 5.9 | 5.9 | 0.067 |
| 2F X方向 | 61.9 | 18.6 | 948 | 0.061 | 17.9 | 1,422 | 0.092 | 11.9 | 11.9 | 0.035 |
| 2F Y方向 | 63.5 | 19.1 | 948 | 0.060 | 18.3 | 1,422 | 0.090 | 12.2 | 12.2 | 0.031 |

## (3) 床スラブ（日本建築学会 RC規準の床厚算定式）

| 区画（壁芯 m） | 短辺内法 | 積載＋仕上 | 必要厚 | 計画 |
|---|---|---|---|---|
| 0.00-6.12×0.00-6.12 | 5.88m | 2.8kN/m² | 165mm | 220mm |
| 0.00-6.12×6.12-12.12 | 5.75m | 2.8kN/m² | 163mm | 220mm |
| 0.00-6.12×12.12-18.25 | 5.88m | 2.8kN/m² | 165mm | 220mm |
| 6.12-12.12×0.00-6.12 | 5.75m | 2.8kN/m² | 163mm | 220mm |
| 6.12-12.12×6.12-12.12 | 5.75m | 2.8kN/m² | 160mm | 220mm |
| 6.12-12.12×12.12-18.25 | 5.75m | 2.8kN/m² | 163mm | 220mm |
| 12.12-18.25×0.00-6.12（ジム） | 5.88m | 6.0kN/m² | 193mm | 220mm |
| 12.12-18.25×6.12-12.12（ジム） | 5.75m | 6.0kN/m² | 191mm | 220mm |
| 12.12-18.25×12.12-18.25 | 5.88m | 2.8kN/m² | 165mm | 220mm |

## 評価

B案で中央スパンを5.0→6.0mにしても、耐力壁で囲まれた面積は最大37.5m²（告示上限60m²）、壁量は16.6〜19.1cm/m²（基準12）で、壁式構造の規定を満たす

地震力に対する壁のせん断応力度は、耐震等級3相当（Co=0.3）でも短期許容値の5倍以上の余裕がある。壁式RCは壁量が多く、地震に対して非常に強い構造である

偏心率が最も大きいのは1階X方向（0.105）。Y2通りのジムの開口（幅5.2m）で北側に剛性が偏るためで、0.15以下に収まる。開口上部の2階の壁は壁梁として設計する

床スラブ t=220 は全区画で必要厚を満たす。ジム床（積載5kN/m²）の必要厚は約193mm

接地圧は約42kN/m²で小さいが、河川近接のため地盤調査（液状化・地下水位）で基礎形式を確定する

## 前提・注意

地盤種別は第2種（Rt=1.0）を仮定。重量はモデルの躯体体積×24kN/m³＋仕上・積載。壁の終局せん断強度は2.0N/mm²、Ds=0.55 の目安で、構造計算（許容応力度計算ルート1）で確定する

耐震等級3を取得する場合は、品確法の評価（壁量・偏心・床倍率に相当する検討）を別途行う

| | | | | |
|---|---|---|---|---|
| 工事名称 | 河沿要（仮称）新築計画 | | | |
| 図面名称 | 耐震検討（壁式RC・概算） | | | 図番 S-03 |
| 縮尺 | A3　— | 日付 2026-10-03 | 設計 設計検討（仮） | |
| 段階 | 基本計画　／　本図は建築基準法令に基づく計画段階の検討図であり、確認申請・構造計算・関係機関協議により確定する | | | |

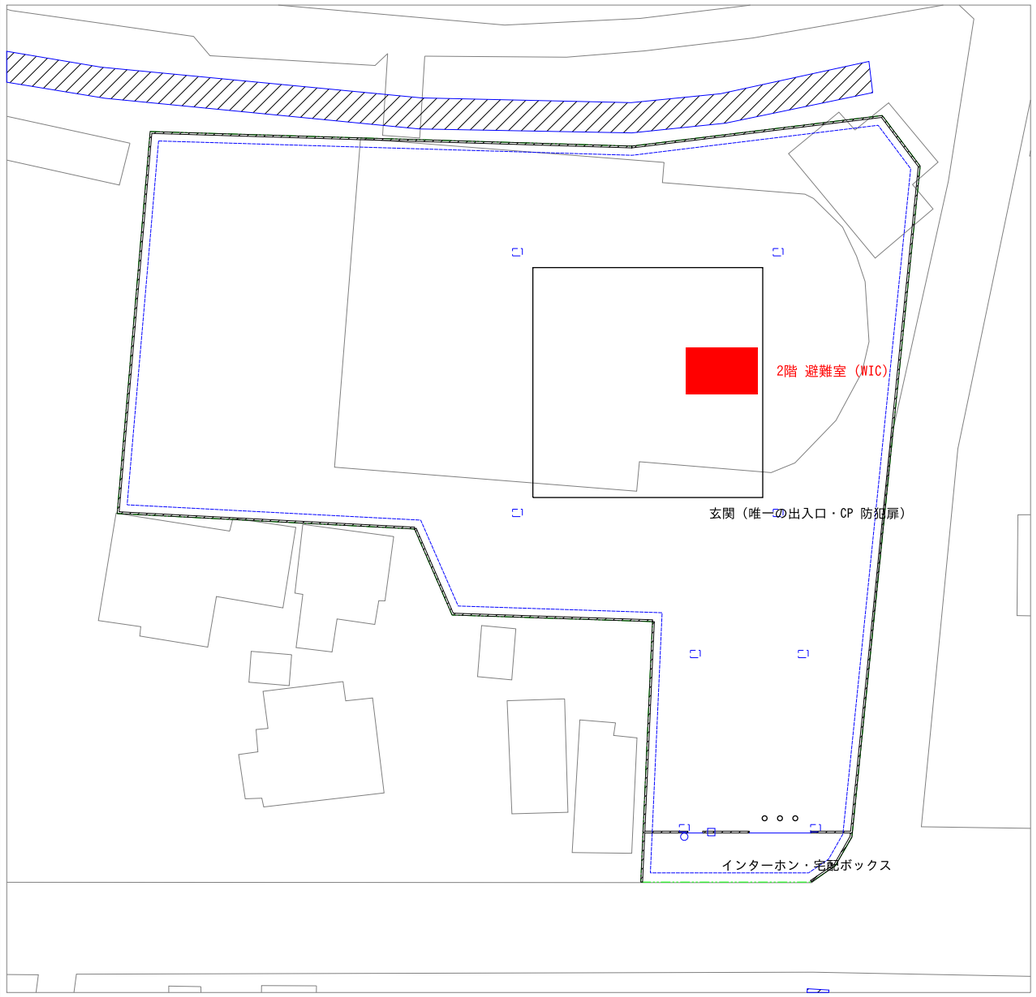


赤外線カメラ
赤外線ビームセンサー（塀の内側）
避難室

防犯計画図 S=1:500

真北 12.3° 西振れ（建物は南側道路に平行）

## (1) 防御の層 ― 見せて諦めさせる → 入らせない → 時間をかけさせる → 知らせる → 逃げ込む

| 層 | 対策 |
|---|---|
| ① 敷地 | RC 塀 H2.0m＋忍び返し、門を道路から4m 後退、赤外線カメラ、勝手口なし |
| ② 門 | 電動スライド門扉（施錠・こじ開け検知）、昇降ボラード、カメラ付きインターホン、貫通型宅配ボックス |
| ③ 建物外皮 | 壁式 RC、窓は全て FIX の CP 防犯合わせガラス、出入口は玄関のみ（CP 防犯扉・2ロック） |
| ④ 知らせる | 塀内の赤外線ビーム、ガラス破壊センサー、非常ボタン、機械警備（警備会社へ自動通報・LTE 予備回線） |
| ⑤ 逃げ込む | 2階 WIC（主寝室）を避難室に。鋼製防犯扉・内締り・非常ボタン・予備電源付き通信 |

## (2) 手口ごとの評価（これまでの構成で十分か）

| 手口 | これまでの構成 | 追加する対策 | 判定 |
|---|---|---|---|
| 宅配・点検業者を装い玄関を開けさせる | 玄関は道路から見えないが、インターホンの位置は未定 | 応対は門のカメラ付きインターホンのみ（玄関まで来させない）。荷物は門の塀の貫通型宅配ボックスで受け取り、門も開けない | 追加で対応 |
| 塀を乗り越える | RC 塀 H2.0m、ビームセンサー | 塀・門扉の天端に忍び返し。ゴミ置きの目隠し壁・ボックスなど足がかりになる物の上にも忍び返し。塀ぎわに木・物置を置かない | 追加で対応 |
| 窓ガラスを割って侵入 | 1階は CP 防犯合わせ、2階は一般の合わせ | 2階も CP 防犯合わせガラスに統一。全窓 FIX（開かない）にガラス破壊センサー。外付けスクリーンは夜間に下ろし、ガラスを見せない | 追加で対応 |
| 玄関ドアをこじ開ける・バールで破る | 未定 | 玄関ドアは CP 防犯扉（こじ開け5分以上）、主錠＋補助錠の2ロック・電気錠、ガードアーム。ドアの開閉・こじ開けをセンサーで検知 | 追加で対応 |
| 屋上・雨どいから侵入 | パラペット H0.6m | 雨どいは外壁内に納め（足がかりにしない）、屋上の点検口は内側から施錠。外に梯子を置かない | 追加で対応 |
| 在宅中に押し入り、住人を拘束する | なし | 寝室・LDK・避難室に非常ボタン（警備会社へ無音通報）。2階 WIC（主寝室）を避難室にし、鋼製防犯扉・内締り・予備通信で警察到着まで籠城できる | 追加で対応 |
| 通信・電源を切る | 蓄電池 16kWh | 警備・カメラ・インターホンは蓄電池から給電、通報は有線＋LTE の2回線。屋外の引込線・分電盤は塀の内側 | 追加で対応 |
| 下見（留守・家族構成を探る） | 門は後退、玄関は道路から見えない | カメラの存在を表示して抑止。録画はクラウドにも保存。アポ電・不審な訪問は bot が記録・通知 | 追加で対応 |
| 車で乗り付け、車ごと逃走 | 門の後退・昇降ボラード | 門前4m は道路から見通せる位置。カメラでナンバーを記録（門・カーポート） | 対応済み |

## 住まい方（設備だけでは防げない部分）

現金・貴金属は自宅に多く置かない（置く場合は避難室の床に固定した耐火金庫）
知らない訪問者には門のインターホン越しに応対し、門も玄関も開けない
警備会社と契約し、在宅時も夜間は外周の警戒（在宅警備モード）を入れる
家族の予定・在宅状況・高額品を SNS に載せない。不審な電話（アポ電）は録音・通知

| | | | | |
|---|---|---|---|---|
| 工事名称 | 河沿要（仮称）新築計画 | | | |
| 図面名称 | 防犯計画（強盗対策） | | | 図番 S-04 |
| 縮尺 | A3 1:500 | 日付 2026-10-03 | 設計 設計検討（仮） | |
| 段階 | 基本計画 ／ 本図は建築基準法令に基づく計画段階の検討図であり、確認申請・構造計算・関係機関協議により確定する | | | |

# 室内環境目標・冷暖房負荷・年間電力需要・必要発電量（概算）― 内寸18.0m角

## (1) 室内環境目標

| 室内環境目標（全室・通年） | 温度 | 湿度 | 絶対湿度 | 露点 |
|---|---|---|---|---|
| 夏（冷房・除湿） | 25〜26℃ | 55〜60% | 10.9〜12.6g/kg | 15.3〜17.6℃ |
| 冬（暖房・加湿） | 20〜21℃ | 55〜60% | 8.0〜9.3g/kg | 10.7〜12.9℃ |

## (2) 冷暖房負荷（旧目標 冬22℃/60%・夏26℃/45% との比較）

| 項目 | 旧目標 | 新目標 | 増減 |
|---|---|---|---|
| 暖房 設計負荷 kW（冬 上限21℃） | 9.40 | 9.04 | -3.8% |
| 冷房 顕熱 kW（夏 下限25℃） | 9.27 | 9.63 | +3.9% |
| 冷房 潜熱（除湿）kW | 2.41 | 2.10 | -13.1% |
| 除湿量 L/日（ピーク） | 85 | 74 | -13.1% |
| 加湿量 L/日（ピーク） | 69 | 63 | -9.4% |
| 年間 暖房熱量 kWh | 19,016 | 17,714 | -6.8% |
| 年間 冷房・除湿熱量 kWh | 8,098 | 8,705 | +7.5% |
| 年間 加湿熱量 kWh | 7,041 | 6,382 | -9.4% |

## (3) 空調機の容量（2系統）

| 系統 | 暖房 | 冷房（顕熱＋潜熱） | 機器選定（提案） |
|---|---|---|---|
| 西系統（X1-X3） | 4.5kW | 5.3kW | 全館空調 5.6kW級＋デシカント調湿 |
| 東系統（X3-X4・ジム/シアター） | 4.5kW | 6.4kW | 全館空調 7.1kW級＋デシカント調湿 |

湿度55〜60%を通年保つため、夏は除湿（露点 約15℃まで）、冬は加湿が主な負荷。湿度幅は狭いので、全熱交換＋デシカント（調湿）を各系統に設け、室ごとの湿度センサーで制御する

結露：冬（外気-4.0℃）の窓の室内表面温度は約18.1℃で、室内露点 12.9℃を上回る。外断熱のため躯体の熱橋も小さい

条件：八王子（地域区分6）、外気 冬-4.0℃・夏34.0℃（19.5g/kg）、換気 0.5回/h（全熱交換 70%回収）、HDD 2150・CDD 430

## (4) 年間電力需要

| 用途 | 年間電力 kWh |
|---|---|
| 暖房（ヒートポンプ SCOP 3.5） | 5,061 |
| 冷房・除湿（SEER 4.0） | 2,176 |
| 加湿（ヒートポンプ式 COP 3.0） | 2,127 |
| 全熱交換換気 2系統（120W×2・常時） | 2,102 |
| 給湯（ヒートポンプ給湯機・4人） | 1,300 |
| 照明（LED 2W/m²・1日4時間） | 1,945 |
| 家電・調理（IH） | 3,000 |
| ジム機器（トレッドミル2台ほか） | 1,395 |
| シアター | 876 |
| 排水ポンプ待機・防犯設備（常時100W） | 876 |
| 合計 | 20,859 |

## (5) 必要発電量 ― 日よけ付き菜園（ソーラーパーゴラ）＋3台用ソーラーカーポート

| 項目 | 値 |
|---|---|
| 必要容量（需要÷1050kWh/kWp） | 19.9 kWp |
| 必要容量（余裕20%・劣化/天候） | 23.8 kWp |
| 必要な架台面積（被覆率70%） | 158 m² |
| ソーラーパーゴラ（菜園） | 18×10m・パネル126m² → 27.1kWp・影損失0.7% → 28,212kWh |
| 3台用ソーラーカーポート | 54m² → 10.2kWp・影損失1.0% → 10,592kWh |
| パーゴラの損失（被覆率70%＋影） | 全面被覆に対し 約12,382kWh → カーポートで86%を補う |
| 合計 年間発電量 | 37.3kWp・38,805 kWh（需要の 186%） |
| 蓄電池（停電時） | 排煙1.6＋排水ポンプ4.5＋生活9.6 ≒ 15.7 kWh → 16kWh級 |

本館とは構造的に分離した独立架台（鉄骨・軒高2.8m・南向き10°）。パネルを列状にすき間をあけて並べ（被覆率70%）、光と雨を下の菜園・庭に落とす。営農型太陽光（ソーラーシェアリング）やソーラーパーゴラとして実例がある

下は半日陰を好む作物（葉物・ハーブ・ミョウガ・シソ・ベリー類）向き。パネルの雨水は雨どいで地下貯留槽へ集め、散水に使う（内水対策と兼用）

影損失は各月21日・30分ごとの太陽位置で本館・塀・隣家（高さ6.5m仮定）の影を追跡して算定。パーゴラは本館の西9mで、冬の朝に一部が影に入る（12月 直達の約5%）

パーゴラ・カーポートとも屋根と柱をもつため建築物として扱われる見込み（建築面積に算入・確認申請が必要）。余剰電力は売電または将来のEV充電に充てる

実施設計で、発電量シミュレーション（建物・塀の影）と住宅の一次エネルギー計算で確定する

| | | | | |
|---|---|---|---|---|
| 工事名称 | 河沿要（仮称）新築計画 | | | |
| 図面名称 | 室内環境・冷暖房負荷・必要発電量（概算） | | | 図番 M-01 |
| 縮尺 | A3 ― | 日付 2026-10-03 | 設計 設計検討（仮） | |
| 段階 | 基本計画 ／ 本図は建築基準法令に基づく計画段階の検討図であり、確認申請・構造計算・関係機関協議により確定する | | | |

# 建物の向きと日射取得 ― 南側道路に平行・直交（南面は真南から 12.3°　西向き）

## (1) 窓からの日射取得（Low-E 南北 g0.45・東西 g0.28、外付けスクリーン 5〜9月、日照率 45%）

| 外壁面 | 窓ガラス ㎡ | 向き（真北基準→道路基準） | 暖房期 取得 kWh | 冷房期 取得 kWh |
|---|---|---|---|---|
| 南面 | 5.30 | +0° → +12.3°（真南から西回り） | 676 → 665 | 64 → 65 |
| 東面 | 4.62 | -90° → -77.7°（真南から西回り） | 197 → 227 | 41 → 42 |
| 北面 | 1.28 | +180° → +192.3°（真南から西回り） | 42 → 42 | 64 → 67 |
| 西面 | 3.26 | +90° → +102.3°（真南から西回り） | 139 → 119 | 29 → 28 |
| 合計 | 14.46 | | 1,054 → 1,053 | 197 → 201 |

## (2) 冷暖房負荷・発電量への影響

| 項目 | 真北基準（回転前） | 南側道路基準（計画） | 差 |
|---|---|---|---|
| 冷房ピークの窓日射取得 kW | 0.30 | 0.29 | -5 W |
| 冷房 顕熱 設計負荷 kW | 9.63 | 9.63 | -5 W |
| 年間 暖房熱量 kWh（日射取得控除後） | 17,714 | 17,714 | +0 |
| 年間 冷房・除湿熱量 kWh | 8,709 | 8,705 | -4 |
| パーゴラ（傾斜10°）の年間日射 kWh/㎡ | 968 | 966 | -0.14% |
| カーポート（傾斜3°）の年間日射 kWh/㎡ | 934 | 934 | -0.05% |
| 影損失（パーゴラ／カーポート） | ― | 0.67%／1.04% | |
| 年間発電量 kWh | ― | 38,805（需要 20,859 の 186%） | |

## 評価

建物・ソーラーパーゴラ・カーポート・目隠し壁を、南側道路の道路境界線（真東西から12.3° 傾く）に平行・直交させた。南面は真南から12.3° 西を向く

窓の日射取得は、東面が冬に少し増え、西面が冬・夏とも少し減る。合計ではほぼ変わらない（窓が小さい FIX 窓中心の外皮のため、方位の影響は小さい）

太陽光は真南から12° 程度の振れでは年間日射の減少が 0.2%未満で、発電量への影響は無視できる

敷地との関係では、建物と道路・塀が平行になり、南側の駐車場・アプローチの配置に無駄がなくなる。北側水路から11.0m、東側道路から10.0m、隣地から9.8m（いずれも がけ条例の2H 以上）

| | | | | |
|---|---|---|---|---|
| 工事名称 | 河沿要（仮称）新築計画 | | | |
| 図面名称 | 建物の向きと日射取得 | | | 図番 M-02 |
| 縮尺 | A3　― | 日付　2026-10-03 | 設計　設計検討（仮） | |
| 段階 | 基本計画　／　本図は建築基準法令に基づく計画段階の検討図であり、確認申請・構造計算・関係機関協議により確定する | | | |

# 窓仕様・紫外線対策 ― 全窓 樹脂サッシ＋Low-E トリプルガラス、UVカット合わせガラス＋外付け電動スクリーン

## (1) 窓の一覧（全12か所・すべて FIX）

| 記号 | 階 | 名称 | 方位 | W×H | Low-E の種類 | g | 外付けスクリーン |
|---|---|---|---|---|---|---|---|
| AW-1 | 1F | FIX 窓（LDK） | 南 | 2,000×1,310 | 日射取得型 | 0.45 | あり（電動） |
| AW-3 | 1F | FIX 高窓（ジム） | 東 | 2,200×650 | 遮熱型 | 0.28 | あり（電動） |
| AW-3 | 1F | FIX 高窓（ジム） | 東 | 2,200×650 | 遮熱型 | 0.28 | あり（電動） |
| AW-7 | 1F | FIX 窓（居室） | 東 | 1,200×800 | 遮熱型 | 0.28 | あり（電動） |
| AW-2 | 1F | FIX 窓（LDK） | 西 | 1,200×1,200 | 遮熱型 | 0.28 | あり（電動） |
| AW-9 | 2F | FIX 窓（居室） | 南 | 1,000×700 | 日射取得型 | 0.45 | あり（電動） |
| AW-9 | 2F | FIX 窓（居室） | 南 | 1,000×700 | 日射取得型 | 0.45 | あり（電動） |
| AW-4 | 2F | FIX 窓（居室） | 南 | 1,600×800 | 日射取得型 | 0.45 | あり（電動） |
| AW-8 | 2F | FIX 窓（主寝室） | 東 | 1,000×800 | 遮熱型 | 0.28 | あり（電動） |
| AW-6 | 2F | FIX 窓（図書室） | 西 | 1,600×700 | 遮熱型 | 0.28 | あり（電動） |
| AW-10 | 2F | FIX 窓（図書室） | 西 | 1,000×700 | 遮熱型 | 0.28 | あり（電動） |
| AW-5 | 2F | FIX 窓（主寝室） | 北 | 1,600×800 | 日射取得型 | 0.45 | ― |

## (2) 窓の仕様（全窓共通）

| 項目 | 仕様 |
|---|---|
| サッシ | 樹脂サッシ（トリプルガラス対応・FIX）、Uw≦0.90 W/m²K |
| ガラス（1階） | 外 防犯合わせ（CP・UVカット中間膜 60mil）8.8 + Ar16 + 4 + Ar16 + Low-E 5 |
| ガラス（2階） | 外 防犯合わせ（CP・UVカット中間膜 60mil）8.8 + Ar16 + 4 + Ar16 + Low-E 5 |
| Low-E | 膜 2面、Ug 0.60 W/m²K。南・北は日射取得型（冬の日射を取り込む）、東・西は遮熱型（朝夕の低い日射を防ぐ） |
| 紫外線 | 室外側の合わせガラス中間膜で紫外線を約99%カット（透過率 1%以下）。全窓共通 |
| 外付けスクリーン | 外付け電動スクリーン（ZIP型・両側レールで生地を保持・日射/風センサー連動、寝室は完全遮光の生地）。南・東・西面の窓 11か所、5〜9月は日射センサーで自動降下（遮蔽係数 0.15） |

## (3) 紫外線のカット効果（窓面に当たる紫外線 年 379.4 kWh = 日射の5%）

| ガラスの種類 | 紫外線透過率 | 室内に入る紫外線 kWh/年 | カット率 |
|---|---|---|---|
| 透明単板ガラス（参考） | 65.0% | 246.61 | 35.0% |
| 透明複層ガラス（参考） | 45.0% | 170.73 | 55.0% |
| Low-E トリプル（合わせなし） | 15.0% | 56.91 | 85.0% |
| 本計画: UVカット合わせ Low-E トリプル | 1.0% | 3.79 | 99.0% |
| 本計画＋外付けスクリーン（5〜9月 S・E・W） | 0.6% | 2.40 | 99.4% |

## (4) 冷暖房負荷への影響

| 項目 | 旧（全窓 遮熱型・スクリーンなし） | Low-E 使い分けのみ | 本計画（＋外付けスクリーン） |
|---|---|---|---|
| 冷房ピークの窓日射取得 kW | 1.25 | 1.54 | 0.29 |
| 冷房 顕熱 設計負荷 kW | 10.59 | 10.88 | 9.63 |
| 暖房期の窓日射取得 kWh | 842 | 1,053 | 1,053 |
| 冷房期の窓日射取得 kWh | 829 | 963 | 201 |
| 年間 暖房熱量 kWh | 17,904 | 17,714 | 17,714 |
| 年間 冷房・除湿熱量 kWh | 9,476 | 9,706 | 8,705 |

## (5) 窓上部 断面詳細（模式図 1:8）

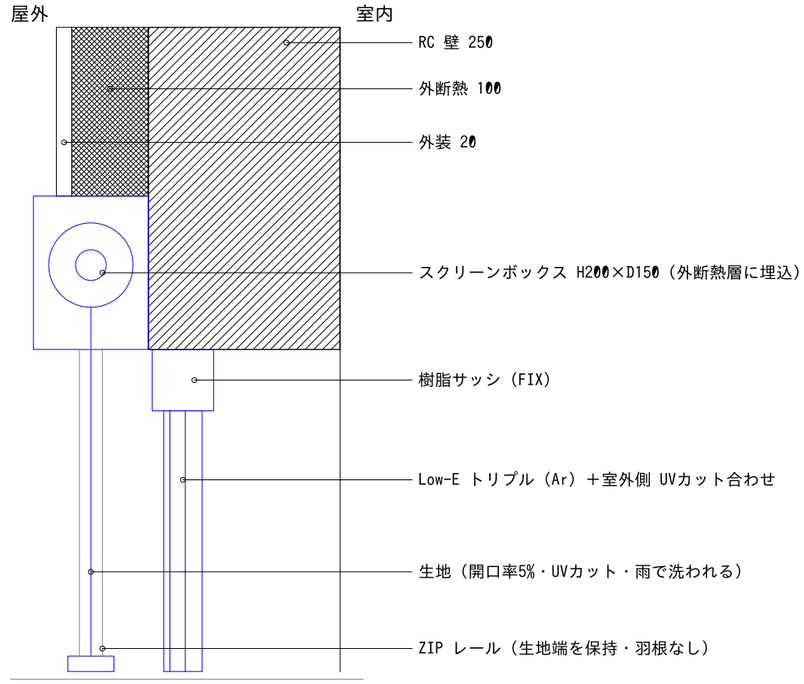


## 紫外線対策の考え方

① ガラス: 全窓の室外側を UVカット中間膜の合わせガラスとし、紫外線を約99%止める（家具・床の退色、肌への影響を抑える）。1・2階とも防犯合わせガラス（CP）を兼ねる

② 外付け電動スクリーン（ZIP型）: 南・東・西の窓は、日射と紫外線をガラスの外で止める。羽根（スラット）がなく、ほこりが溜まらず清掃不要に近い。夏（5〜9月）は日射センサーで自動降下、冬は上げて日射を取り込む。強風時は自動で巻き上げる

③ Low-E の使い分け: 南・北は日射取得型で冬の暖房を助け、夏の南面はスクリーンで遮る。東・西は低い朝夕日を防ぐ遮熱型

④ 屋外: 玄関庇（出2.0m）、ソーラーパーゴラ（被覆率70%）、カーポート屋根が、屋外の作業・乗降時の日よけになる

数値は概算（日射の5%を紫外線とし、ガラスの透過率は代表値）。実施設計でガラス・スクリーンのメーカー値により確定する

| | | | | |
|---|---|---|---|---|
| 工事名称 | 河沿要（仮称）新築計画 | | | |
| 図面名称 | 窓仕様・紫外線対策 | | | 図番 M-03 |
| 縮尺 | A3 ― | 日付 2026-10-03 | 設計 設計検討（仮） | |
| 段階 | 基本計画 ／ 本図は建築基準法令に基づく計画段階の検討図であり、確認申請・構造計算・関係機関協議により確定する | | | |

# 暮らし方への対応 ― 睡眠・空気・水・食（菜園）・運動・測定（寝室は1部屋に1人）

## (1) 寝室の空気 ― 就寝中の CO2 を 800ppm 以下に（1人 14L/h、外気 420ppm）

| 寝室 | 階 | 容積 | 基本換気 0.5回/h | 就寝中 CO2 | 計画換気 | 就寝中 CO2 |
|---|---|---|---|---|---|---|
| 居室A | 1F | 45m³ | 23m³/h | 1,042ppm | 37m³/h（0.82回/h） | 800ppm |
| 居室B | 2F | 33m³ | 16m³/h | 1,281ppm | 37m³/h（1.13回/h） | 800ppm |
| 居室C | 2F | 31m³ | 15m³/h | 1,323ppm | 37m³/h（1.19回/h） | 800ppm |
| 居室D | 2F | 44m³ | 22m³/h | 1,051ppm | 37m³/h（0.83回/h） | 800ppm |
| 主寝室 | 2F | 90m³ | 45m³/h | 732ppm | 45m³/h（0.50回/h） | 732ppm |

寝室ごとに CO2 センサーで換気量を自動で増やす（需要制御）。必要量は1人 約37m³/h。増える換気は合計 約71m³/h で、全熱交換で回収するため冷暖房の増加は年 約149kWh

全熱交換の給気フィルター ePM1 70%以上（PM2.5 を除去）、CO2・PM2.5・VOC センサーを各寝室と LDK に

## (2) 睡眠・水・測定

| 項目 | 計画 |
|---|---|
| 睡眠 | 寝室の外付けスクリーンは完全遮光の生地（開口率0%）。室ごとに温度を設定（初期値は全室目標の下限 = 夏25℃・冬20℃、±2℃の範囲で変更可）。夜（22〜6時）は照明 2200K・10% 以下、寝室の Wi-Fi AP は表示灯を消し電波を止める |
| 水 | 家全体の浄水フィルター（機械室）＋台所に逆浸透膜（RO）浄水器 |
| 運動・測定 | ジムに測定コーナー（体組成計・血圧計）、睡眠・活動の記録を bot に集約。エピゲノム検査は小平の医療機関で定期測定 |
| 温冷浴 | サウナは設けない（施主判断） |

## (3) 菜園 ― 基本はプランター、日当たりで作物を分ける

| 場所 | 面積 | 直達日射の影損失（年） | 12月 | 6月 |
|---|---|---|---|---|
| 日なたのプランター菜園（建物の南） | 植付 21.6m² | 2.1% | 8% | 0% |
| パーゴラの下（パネル被覆70%） | ― | 約71%（半日陰） | ― | ― |

| 場所 | 向く作物（家庭菜園で育てられるもの） |
|---|---|
| 日なたのプランター | ブロッコリー・カリフラワー・ケール・キャベツ（アブラナ科）、トマト、ピーマン、ズッキーニ、ブルーベリー |
| パーゴラの下（半日陰） | ほうれん草・小松菜・レタス・春菊、しそ・バジル・パセリ・ミント、しょうが・みょうが、にんにく・ねぎ |
| 購入に頼るもの | 豆類（レンズ豆など）・ナッツ・きのこ類の多く・オリーブオイル |

## (4) プランターと床（模式図 1:20）― 床を傷めない置き方

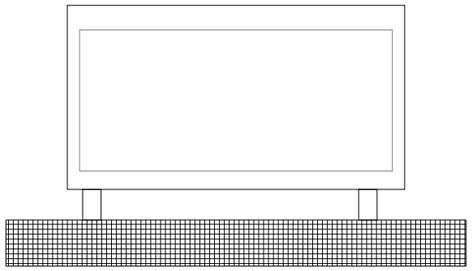

標準: Dotcon+ の上に脚付きプランター
脚で 100mm 浮かせる（土・水が床に触れない）
Dotcon+（透水・水が溜まらない）

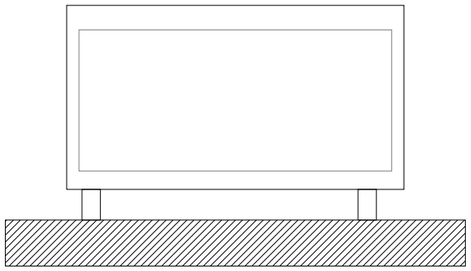

将来: RC 土間（基礎）の上の農場
脚で 100mm 浮かせる（土・水が床に触れない）
RC 土間 t150・勾配1/100・吸水防止材

### 床（基礎）の劣化を抑える考え方

土・肥料・水を床に直接触れさせない（脚で浮かせ、受け皿は置かない）。コンクリートを傷めるのは、長く湿った状態と肥料の酸・塩分、根の侵入

将来 RC 土間の上を農場にする場合: 将来「基礎（RC 土間）の上の農場」とする場合は、t150・水セメント比45%以下・かぶり50・表面に浸透性吸水防止材・勾配1/100、土は防水ライナー＋排水層で床から絶縁し、プランターと同じく脚で浮かせる

受け皿・水たまりをつくらない（蚊の発生を防ぐ、E-03）。プランターは底から排水し、水は Dotcon+ に浸透させる

土は購入した培養土を使う（旧店舗跡地の土は検査するまで使わない）

| | | | | |
|---|---|---|---|---|
| 工事名称 | 河沿要（仮称）新築計画 | | | |
| 図面名称 | 暮らし方への対応（睡眠・空気・水・菜園） | | | 図番 M-04 |
| 縮尺 | A3 ― | 日付 2026-10-03 | 設計 設計検討（仮） | |
| 段階 | 基本計画 ／ 本図は建築基準法令に基づく計画段階の検討図であり、確認申請・構造計算・関係機関協議により確定する | | | |

# 内装設計方針 ― 「すばらしいデザインは安全であるべき」「清掃とメンテナンスが簡易であるべき」

## (1) 安全 ― 危険をデザインでなくす

| 危険 | 対策（設計で決めること） | 対象 |
|---|---|---|
| 頭部の挟み込み | 階段の手すり壁・腰壁はすき間のないパネル（手すり子・横桟を使わない）。造作家具・設備まわりに 100〜230mm の階段1・2、全室<br>すき間をつくらない | |
| 指の挟み込み | 開き戸は吊元側に指はさみ防止カバー＋戸当り。引戸は上吊り・両側ソフトクローズ・引き残し50（ガラス引戸は戸と全建具<br>壁のすき間30）。遮音扉は低速クローザー＋戸先ゴム | |
| 転落 | 窓は全て FIX（開かない）。吹抜けなし。階段開口は H1,100 の手すり壁、階段の間の壁は 2FL+1,100 まで立ち上<br>げ | 窓・階段 |
| 転倒 | 段差は玄関框（2段）のみで縦手すり付き。床見切り・引戸レールは段差5mm以下（つまずかない・掃除ロボットが越え<br>られる）。水回りは濡れても滑りにくい床 | 全室 |
| 衝突 | 手の届く高さの出隅は R10。ガラス入り建具は合わせガラス（玄関ホールの透明扉は合わせ強化＋乳白の帯 FL+850〜1<br>,000・1,400〜1,550）。動線上に吊り照明を設けない | 全室 |
| ひもによる窒息 | 室内にブラインド・カーテンのひもを使わない（日射・紫外線は外付けスクリーンで制御） | 全窓 |
| 閉じ込め・溺水 | トイレ・洗面・浴室は外から開けられる非常解錠錠。浴室扉は子どもの手が届かない補助錠 H1,400 | 水回り |
| 感電・やけど | シャッター付きコンセント。IH はチャイルドロック。浴室はサーモスタット水栓（上限40℃） | 全室・水回り |
| 危険な部屋 | ジムは暗証番号錠（子どもだけで入らない）、機器は自重・広い脚で安定（床・壁に穴をあけない）、トレッドミルはジム・機械室<br>安全キー。機械室は施錠 | |
| 家具の転倒 | RC 壁には固定しない（外断熱の躯体に穴をあけない）。背の高い収納・本棚は床と天井の間の突っ張り（天井下地を補 | 全室<br>強）と、幅広の脚・背面連結・低重心（重い物は下段）の構造で倒れにくくする。扉は耐震ラッチ |

## (2) 清掃・メンテナンス ― 手入れの頻度を減らす

| 部位 | 清掃・メンテナンスを簡単にする選び方 |
|---|---|
| 床 | 床清掃は掃除ロボットが行う（各階に自動ゴミ収集・給排水直結のドック）。段差5mm以下、床に配線を這わせない、家具は台輪で床まで塞ぐか<br>脚下250mm以上、黒い床・敷物を避ける（段差センサーの誤作動）。継目の少ないノンワックス床 |
| 巾木・入隅 | 薄型ソフト巾木（入隅一体）で、ほこりが溜まる段差・すき間をなくす |
| 壁 | 拭き取れる耐汚染塗装。汚れやすい所（キッチン・トイレ・玄関・ジムの腰）は目地のない化粧パネル |
| 天井・照明 | フラット天井（溝なし）。主照明は天井直付けのライン LED（乳白・継ぎ目の少ない連結型）、埋込ダウンライトは弱い補助灯。時刻で自動変<br>化（調光・調色） |
| 収納 | 扉付き・天井まで（上部にほこりが溜まらない）。突っ張り式で天井と一体に見せ、すき間をつくらない。キッチン・パントリーは施主指示によ<br>り全露出のオープン棚（毎日使う物以外はバスケット・透明容器、月1回の拭き取り） |
| 水回り | タンク式便器（フチなし・防汚、停電・断水後も洗浄しやすい）、一体成形のカウンター・シンク、浴室乾燥機でカビを抑える |
| 窓 | 全て FIX で網戸なし。室外側ガラスは親水コーティング（雨で汚れが流れる）。2階の外側は地上から水洗いポール（約6m）で清掃 |
| 日よけ | 外付けスクリーンは ZIP 型（羽根なし）。生地は雨で洗われ、傷んだら生地だけ交換 |
| 空調 | 全館空調のフィルターは機械室で床から手の届く高さ。吹出口・吸込口は天井スリット（床ガラリなし＝ゴミ・指が入らない） |

## (3) 階段の寸法（品確法 高齢者等配慮 等級5相当で確認）

| 階段 | 蹴上 R | 踏面 T | 勾配 R/T（≦6/7） | 2R+T（550〜650） | 有効幅 | 蹴込み | 判定 |
|---|---|---|---|---|---|---|---|
| 階段1 | 177.8 | 260 | 0.684 | 616 | 1,150 | 30以下（蹴込み板あり） | OK |
| 階段2 | 177.8 | 240 | 0.741 | 596 | 950 | 30以下（蹴込み板あり） | OK |

## (4) 手すり壁・腰壁（頭部 100〜230mm・指 8〜25mm のすき間をつくらない）

| 位置 | 長さ | 高さ | 端部のすき間 | 判定 |
|---|---|---|---|---|
| 階段1 2階開口 | 1,250 | 1,100 | 0（壁に接する）・0（壁に接する） | OK |
| 階段1 2階開口 | 1,385 | 1,100 | 1,050（降り口の通路）・0（壁に接する） | OK |
| 階段2 2階開口 | 1,050 | 1,100 | 0（壁に接する）・0（壁に接する） | OK |
| 階段の間の手すり壁 | 全長 | 2FL+1,100 | 上下の階段で連続（すき間なし） | OK |

## (5) 手すり壁の考え方（模式図）

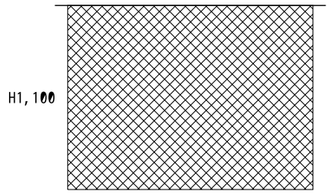


採用：すき間のないパネル

不採用：手すり子・横桟

## 一貫させること

すばらしいデザインは安全であるべき ― 子どもの頭・指が挟まるすき間、転落・転倒・衝突・感電・絞首の危険をつくらない

清掃とメンテナンスが簡易であるべき ― ほこりが溜まる凹凸・目地・溝をつくらず、頻繁な手入れを要する素材・機構を使わない

見た目のための凹凸（オープン棚・間接照明の溝・格子・スリット）は、危険かほこり溜まりになるなら採用しない。意匠は素材の質感・色・光（窓の位置）でつくる

各室の仕上げは I-02 内装仕上表による。建具金物（指はさみ防止・ソフトクローズ・非常解錠）は A-09 建具表の全建具に適用

| | | | | |
|---|---|---|---|---|
| 工事名称 | 河沿要（仮称）新築計画 | | | |
| 図面名称 | 内装設計方針（安全・清掃性） | | | 図番 I-01 |
| 縮尺 | A3 ― | 日付 2026-10-03 | 設計 設計検討（仮） | |
| 段階 | 基本計画 ／ 本図は建築基準法令に基づく計画段階の検討図であり、確認申請・構造計算・関係機関協議により確定する | | | |

# 内装仕上表 ― 安全で、掃除と手入れが簡単な仕上げに統一

| 階 | 室名 | 面積 | 床 | 巾木 | 壁 | 天井 | 安全・清掃の要点 |
|---|---|---|---|---|---|---|---|
| 1F | リビング・ダイニング | 34.5 | 複合フローリング（ノンワックス・耐傷・耐水） | 薄型ソフト巾木 H60（入隅一体） | PB＋耐汚染塗装（拭き取り可） | PB＋EP（フラット・溝なし）＋直付ライン LED（主）・埋込 LED（弱） | 出隅 R10、コンセントはシャッター付き |
| 1F | キッチン | 25.3 | 複合フローリング（ノンワックス・耐傷・耐水） | 薄型ソフト巾木 H60（入隅一体） | コンロ前 メラミン不燃パネル一枚貼り（目地なし） | PB＋EP（フラット・溝なし）＋直付ライン LED（主）・埋込 LED（弱） | IH（チャイルドロック）・一体成形シンク・ダウンドラフト換気（フィルターは食洗機で洗える）・オープン棚（全露出、施主指示 v4.17）・包丁は FL+1,600 の磁石バー |
| 1F | パントリー | 7.9 | 複合フローリング（ノンワックス・耐傷・耐水） | 薄型ソフト巾木 H60（入隅一体） | PB＋耐汚染塗装（拭き取り可） | PB＋EP（フラット・溝なし）＋直付ライン LED（主）・埋込 LED（弱） | 突っ張り式のオープン棚＋ワイヤーバスケット・透明容器（全露出、施主指示 v4.17） |
| 1F | 玄関土間 | 10.8 | 大判磁器タイル 600角（細目地・防汚目地、濡れても滑りにくい） | タイル巾木（面一） | 腰 化粧パネル H1,000＋耐汚染塗装 | PB＋EP（フラット・溝なし）＋直付ライン LED（主）・埋込 LED（弱） | 下足入れは扉付き・台輪で床まで塞ぐ、框に縦手すり |
| 1F | 式台（框1） | 2.3 | 複合フローリング（ノンワックス・耐傷・耐水） | 薄型ソフト巾木 H60（入隅一体） | PB＋耐汚染塗装（拭き取り可） | PB＋EP（フラット・溝なし）＋直付ライン LED（主）・埋込 LED（弱） | 框は人造大理石 一体成形・角R、段鼻に色差 |
| 1F | ホール | 20.7 | 複合フローリング（ノンワックス・耐傷・耐水） | 薄型ソフト巾木 H60（入隅一体） | PB＋耐汚染塗装（拭き取り可） | PB＋EP（フラット・溝なし）＋直付ライン LED（主）・埋込 LED（弱） | 出隅 R10、コンセントはシャッター付き |
| 1F | ジム | 51.6 | ゴムシート t15（継目溶接・シームレス） | 床シート立上げ H100（巾木一体） | 腰 耐衝撃化粧パネル H1,200＋耐汚染塗装 | PB＋EP（直天井） | 暗証番号錠、機器は自重・広い脚で安定（床・壁に穴をあけない）、鏡は飛散防止フィルム・突っ張り枠 |
| 1F | ホール・階段1 | 20.4 | 複合フローリング（ノンワックス・耐傷・耐水）・段鼻ノンスリップ面一 | 薄型ソフト巾木 H60（入隅一体） | PB＋耐汚染塗装（拭き取り可） | PB＋EP（フラット・溝なし）＋直付ライン LED（主）・埋込 LED（弱） | 蹴込み板あり、手すり連続、手すり壁はすき間なし、足元灯（踏面から300・2段おき・停電時点灯） |
| 1F | トイレ（手洗い付） | 3.9 | 塩ビシームレスシート（耐アンモニア） | 床シート立上げ H100（巾木一体） | 腰 化粧パネル H1,000＋耐汚染塗装 | PB＋EP（フラット・溝なし）＋直付ライン LED（主）・埋込 LED（弱） | タンク式便器（フチなし・停電時も洗浄可）、非常解錠錠 |
| 1F | 機械室（西系統） | 8.6 | 防塵塗装 | ― | PB＋EP | PB＋EP | 施錠。フィルターは床から手の届く高さ |
| 1F | 機械室（東系統） | 8.8 | 防塵塗装 | ― | PB＋EP | PB＋EP | 施錠。フィルターは床から手の届く高さ |
| 1F | ランドリー・室内干し | 16.2 | 塩ビシームレスシート（耐水） | 床シート立上げ H100（巾木一体） | 耐水化粧パネル（目地なし） | PB＋EP（フラット・溝なし）＋直付ライン LED（主）・埋込 LED（弱） | 物干しは天井付け・取外し式（ひも・昇降ワイヤーなし） |
| 1F | ファミリークローゼット | 11.4 | 複合フローリング（ノンワックス・耐傷・耐水） | 薄型ソフト巾木 H60（入隅一体） | 化粧 PB | PB＋EP（フラット・溝なし）＋直付ライン LED（主）・埋込 LED（弱） | 扉付き・天井まで（上部にほこり溜まりなし） |
| 1F | 洗面・脱衣 | 8.3 | 塩ビシームレスシート（耐水） | 床シート立上げ H100（巾木一体） | 耐水化粧パネル（目地なし） | PB＋EP（フラット・溝なし）＋直付ライン LED（主）・埋込 LED（弱） | 一体成形カウンターボウル、非常解錠錠 |
| 1F | 浴室 | 10.5 | ユニットバス 速乾床 | ― | ユニットバス パネル | ユニットバス 平天井 | 浴室乾燥機・排水口は清掃容易型・扉に補助錠 H1,400 |
| 1F | 廊下 ×2 | 15.1 | 複合フローリング（ノンワックス・耐傷・耐水） | 薄型ソフト巾木 H60（入隅一体） | PB＋耐汚染塗装（拭き取り可） | PB＋EP（フラット・溝なし）＋直付ライン LED（主）・埋込 LED（弱） | 出隅 R10、コンセントはシャッター付き |
| 1F | トイレ | 6.1 | 塩ビシームレスシート（耐アンモニア） | 床シート立上げ H100（巾木一体） | 腰 化粧パネル H1,000＋耐汚染塗装 | PB＋EP（フラット・溝なし）＋直付ライン LED（主）・埋込 LED（弱） | タンク式便器（フチなし・停電時も洗浄可）、非常解錠錠 |
| 1F | 居室A | 17.3 | 複合フローリング（ノンワックス・耐傷・耐水） | 薄型ソフト巾木 H60（入隅一体） | PB＋耐汚染塗装（拭き取り可） | PB＋EP（フラット・溝なし）＋直付ライン LED（主）・埋込 LED（弱） | 出隅 R10、コンセントはシャッター付き |
| 1F | WIC | 8.8 | 複合フローリング（ノンワックス・耐傷・耐水） | 薄型ソフト巾木 H60（入隅一体） | 化粧 PB | PB＋EP（フラット・溝なし）＋直付ライン LED（主）・埋込 LED（弱） | 棚・パイプは突っ張り式フレーム |
| 2F | 居室B | 12.5 | 複合フローリング（ノンワックス・耐傷・耐水） | 薄型ソフト巾木 H60（入隅一体） | PB＋耐汚染塗装（拭き取り可） | PB＋EP（フラット・溝なし）＋直付ライン LED（主）・埋込 LED（弱） | 出隅 R10、コンセントはシャッター付き |
| 2F | 収納 | 2.6 | 複合フローリング（ノンワックス・耐傷・耐水） | 薄型ソフト巾木 H60（入隅一体） | 化粧 PB | PB＋EP（フラット・溝なし）＋直付ライン LED（主）・埋込 LED（弱） | 扉付き・天井まで |
| 2F | 居室C | 11.9 | 複合フローリング（ノンワックス・耐傷・耐水） | 薄型ソフト巾木 H60（入隅一体） | PB＋耐汚染塗装（拭き取り可） | PB＋EP（フラット・溝なし）＋直付ライン LED（主）・埋込 LED（弱） | 出隅 R10、コンセントはシャッター付き |
| 2F | 廊下 ×3 | 20.6 | 複合フローリング（ノンワックス・耐傷・耐水） | 薄型ソフト巾木 H60（入隅一体） | PB＋耐汚染塗装（拭き取り可） | PB＋EP（フラット・溝なし）＋直付ライン LED（主）・埋込 LED（弱） | 出隅 R10、コンセントはシャッター付き |
| 2F | 居室D | 17.1 | 複合フローリング（ノンワックス・耐傷・耐水） | 薄型ソフト巾木 H60（入隅一体） | PB＋耐汚染塗装（拭き取り可） | PB＋EP（フラット・溝なし）＋直付ライン LED（主）・埋込 LED（弱） | 出隅 R10、コンセントはシャッター付き |
| 2F | WIC | 9.3 | 複合フローリング（ノンワックス・耐傷・耐水） | 薄型ソフト巾木 H60（入隅一体） | 化粧 PB | PB＋EP（フラット・溝なし）＋直付ライン LED（主）・埋込 LED（弱） | 棚・パイプは突っ張り式フレーム |
| 2F | シアター | 34.5 | タイルカーペット（汚れた1枚だけ交換） | 薄型ソフト巾木 H60（入隅一体） | PET 吸音ボード（拭き取り・掃除機可） | 吸音 PB（フラット） | 遮音扉は低速クローザー＋戸先ゴム |
| 2F | 前室（音響ロック） | 10.9 | タイルカーペット | 薄型ソフト巾木 H60（入隅一体） | PET 吸音ボード | PB＋EP（フラット・溝なし）＋直付ライン LED（主）・埋込 LED（弱） | 遮音扉は低速クローザー＋戸先ゴム |
| 2F | WIC（主寝室） | 22.3 | 複合フローリング（ノンワックス・耐傷・耐水） | 薄型ソフト巾木 H60（入隅一体） | 化粧 PB | PB＋EP（フラット・溝なし）＋直付ライン LED（主）・埋込 LED（弱） | 棚・パイプは突っ張り式フレーム |
| 2F | 図書室 | 33.8 | 複合フローリング（ノンワックス・耐傷・耐水） | 薄型ソフト巾木 H60（入隅一体） | PB＋耐汚染塗装（拭き取り可） | PB＋EP（フラット・溝なし）＋直付ライン LED（主）・埋込 LED（弱） | 本棚は床・天井の突っ張り＋背面連結、重い本は下段、可動はしごなし |
| 2F | ホール・階段1 | 20.4 | 複合フローリング（ノンワックス・耐傷・耐水）・段鼻ノンスリップ面一 | 薄型ソフト巾木 H60（入隅一体） | PB＋耐汚染塗装（拭き取り可） | PB＋EP（フラット・溝なし）＋直付ライン LED（主）・埋込 LED（弱） | 蹴込み板あり、手すり連続、手すり壁はすき間なし、足元灯（踏面から300・2段おき・停電時点灯） |
| 2F | トイレ（手洗い付） | 3.9 | 塩ビシームレスシート（耐アンモニア） | 床シート立上げ H100（巾木一体） | 腰 化粧パネル H1,000＋耐汚染塗装 | PB＋EP（フラット・溝なし）＋直付ライン LED（主）・埋込 LED（弱） | タンク式便器（フチなし・停電時も洗浄可）、非常解錠錠 |
| 2F | ファミリークローゼット | 22.2 | 複合フローリング（ノンワックス・耐傷・耐水） | 薄型ソフト巾木 H60（入隅一体） | 化粧 PB | PB＋EP（フラット・溝なし）＋直付ライン LED（主）・埋込 LED（弱） | 扉付き・天井まで（上部にほこり溜まりなし） |
| 2F | ホール・階段2 | 5.5 | 複合フローリング（ノンワックス・耐傷・耐水）・段鼻ノンスリッ | 薄型ソフト巾木 H60（入隅一体） | PB＋耐汚染塗装（拭き取り可） | PB＋EP（フラット・溝なし）＋ | 蹴込み板あり、手すり連続、手すり壁はすき間なし、足元灯（踏面から300・2段おき・停電時点灯） |

| | |
|---|---|
| 工事名称 | 河谷要（仮称）新築計画 |
| 図面名称 | 内装仕上表 |
| 縮尺 | 1/3（A3） |
| 段階 | 基本設計 |

図番 I-02

日付 2026-10-03　設計 設計検討（仮）

基本設計 ／ 本図は建築基準法令に基づく計画段階の検討図であり、確認申請・構造計算・関係機関協議により確定する

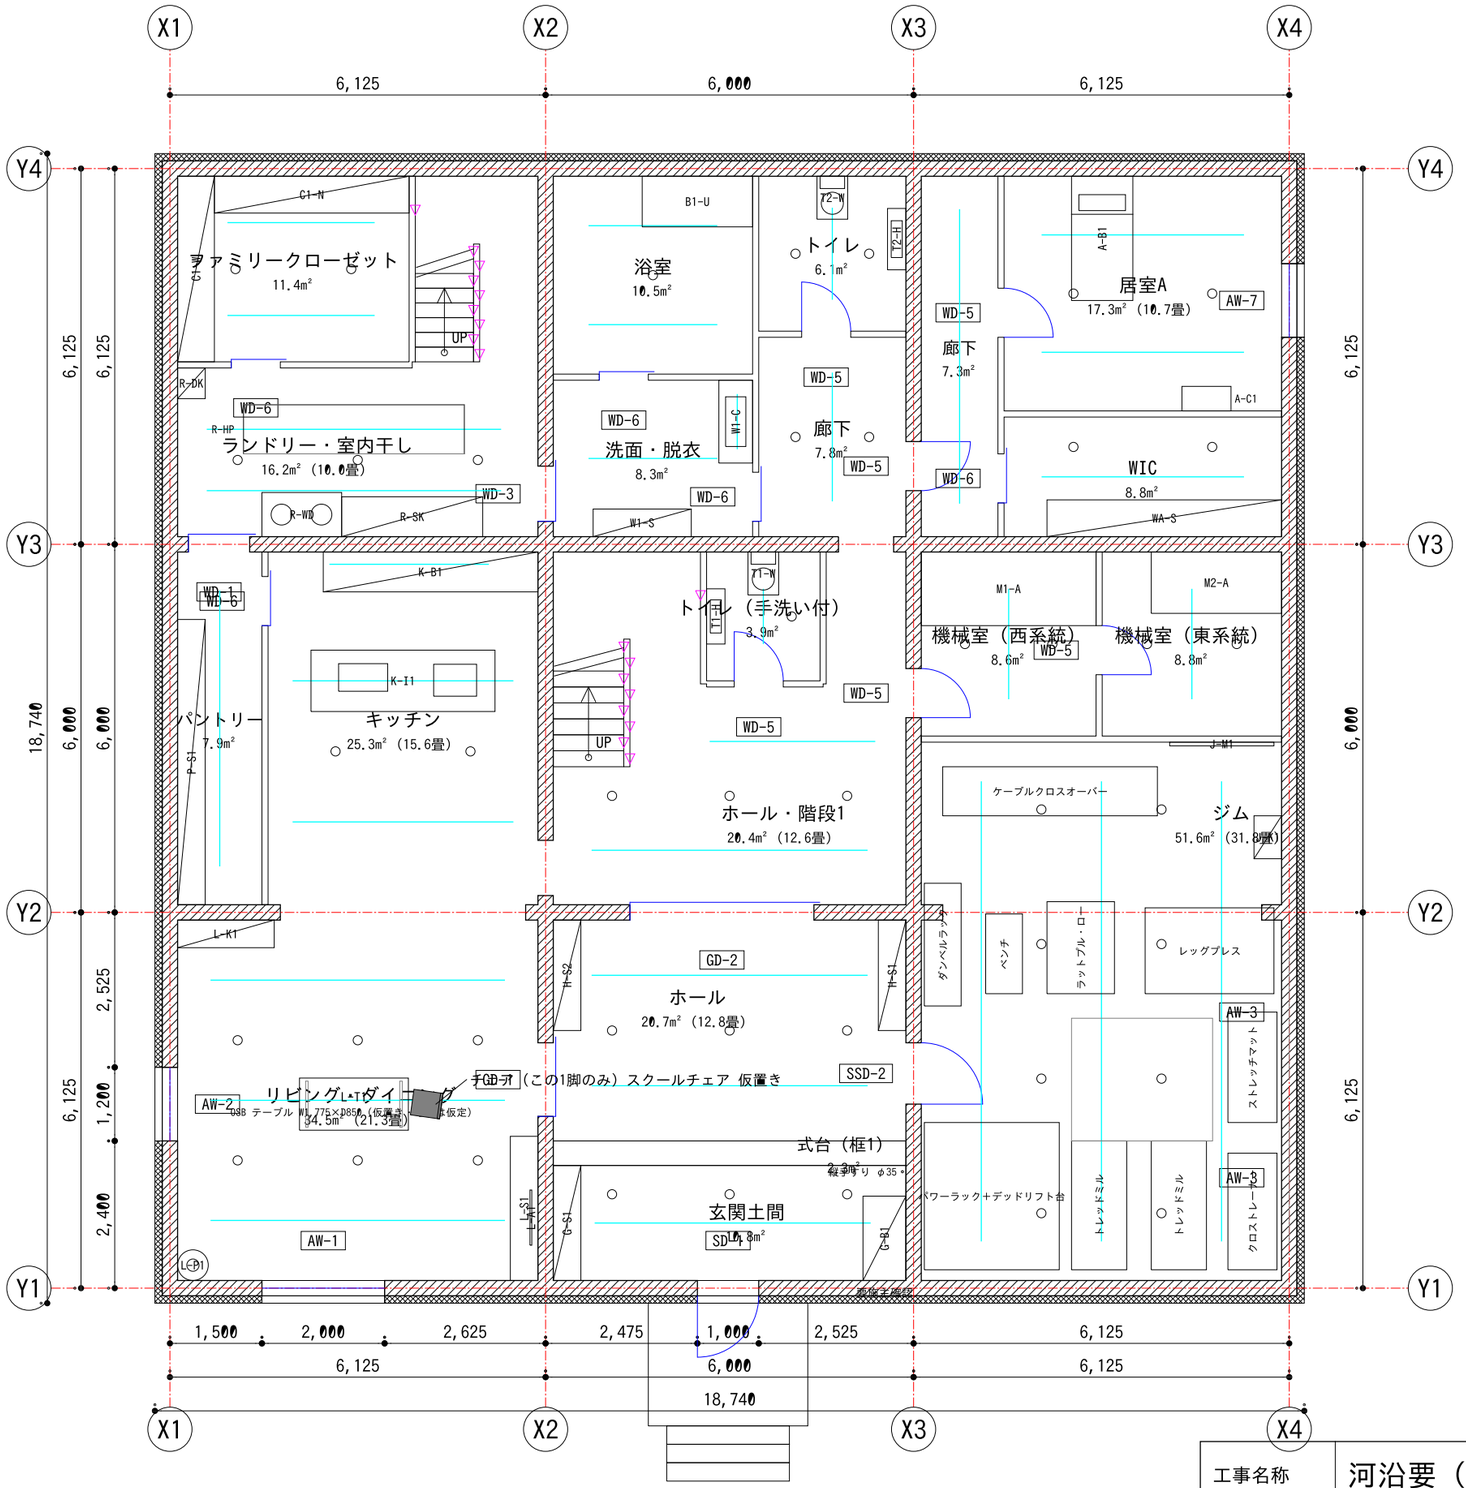


## 凡例・注記

- 家具（外形・細線）
- チェア（外形を塗り）
- 埋込ダウンライト（弱）φ100
- 直付ライン LED（主照明）
- 階段の足元灯（踏面+300）
- テーブルの脚位置・物干しパイプ
- 開き戸の軌跡

N

真北 12.3° 西振れ（建物は南側道路に平行）

## 仮置きの前提

家具は仮置き（後日差し替え）。指定商品（OSB テーブル・スクールチェア）の寸法は仮定（商品ページ未確認）。チェアは LDK の1脚のみ。色はいずれも仮定

ID は I-05 家具表の ID。収納は対角線、ベッドは枕の線、ソファは座クッションの割付を示す

床置きの家具は、台輪で床まで塞ぐ（掃除ロボット）、脚下 250mm 以上、洗面・手洗いは床から 650 浮かせる、のいずれか。壁との間は密着か 250mm 以上（頭・指が挟まるすき間をつくらない）

扉の軌跡と、扉・開口の前後 600 の通行帯には家具を置かない。コンセント・スイッチ（シャッター付き）は FL+250／FL+1,100、床コンセントなし

ジム機器は既存の配置のまま。安全帯（トレッドミル後方 2.0m）と重ねない

LDK: チェアは1脚だけ（施主指示）。テーブルは回遊①の通り道から 1,600 以上離す

玄関のベンチ・下足入れは既存（A-03）。座る家具の扱い（ベンチ）は要施主確認。下足入れは台輪で床まで塞ぐ（ブリーフ17章の「床から浮かせる」との食い違いは要施主確認）

キッチンの換気は IH 一体のダウンドラフト（天井はフラットのまま。要施主確認）

## 1階 家具配置図（仮置き） S=1:100

1FL = 設計GL+1,500（TP+1100.50）／天井高 CH=2,600／○ = 埋込ダウンライト（弱）、太線 = 直付ライン LED

| | | | | |
|---|---|---|---|---|
| 工事名称 | 河沿要（仮称）新築計画 | | | |
| 図面名称 | 1階 家具配置図（仮置き） | | | 図番 I-03 |
| 縮尺 | A3 1:100 | 日付 2026-10-03 | 設計 設計検討（仮） | |
| 段階 | 基本計画 ／ 本図は建築基準法令に基づく計画段階の検討図であり、確認申請・構造計算・関係機関協議により確定する | | | |

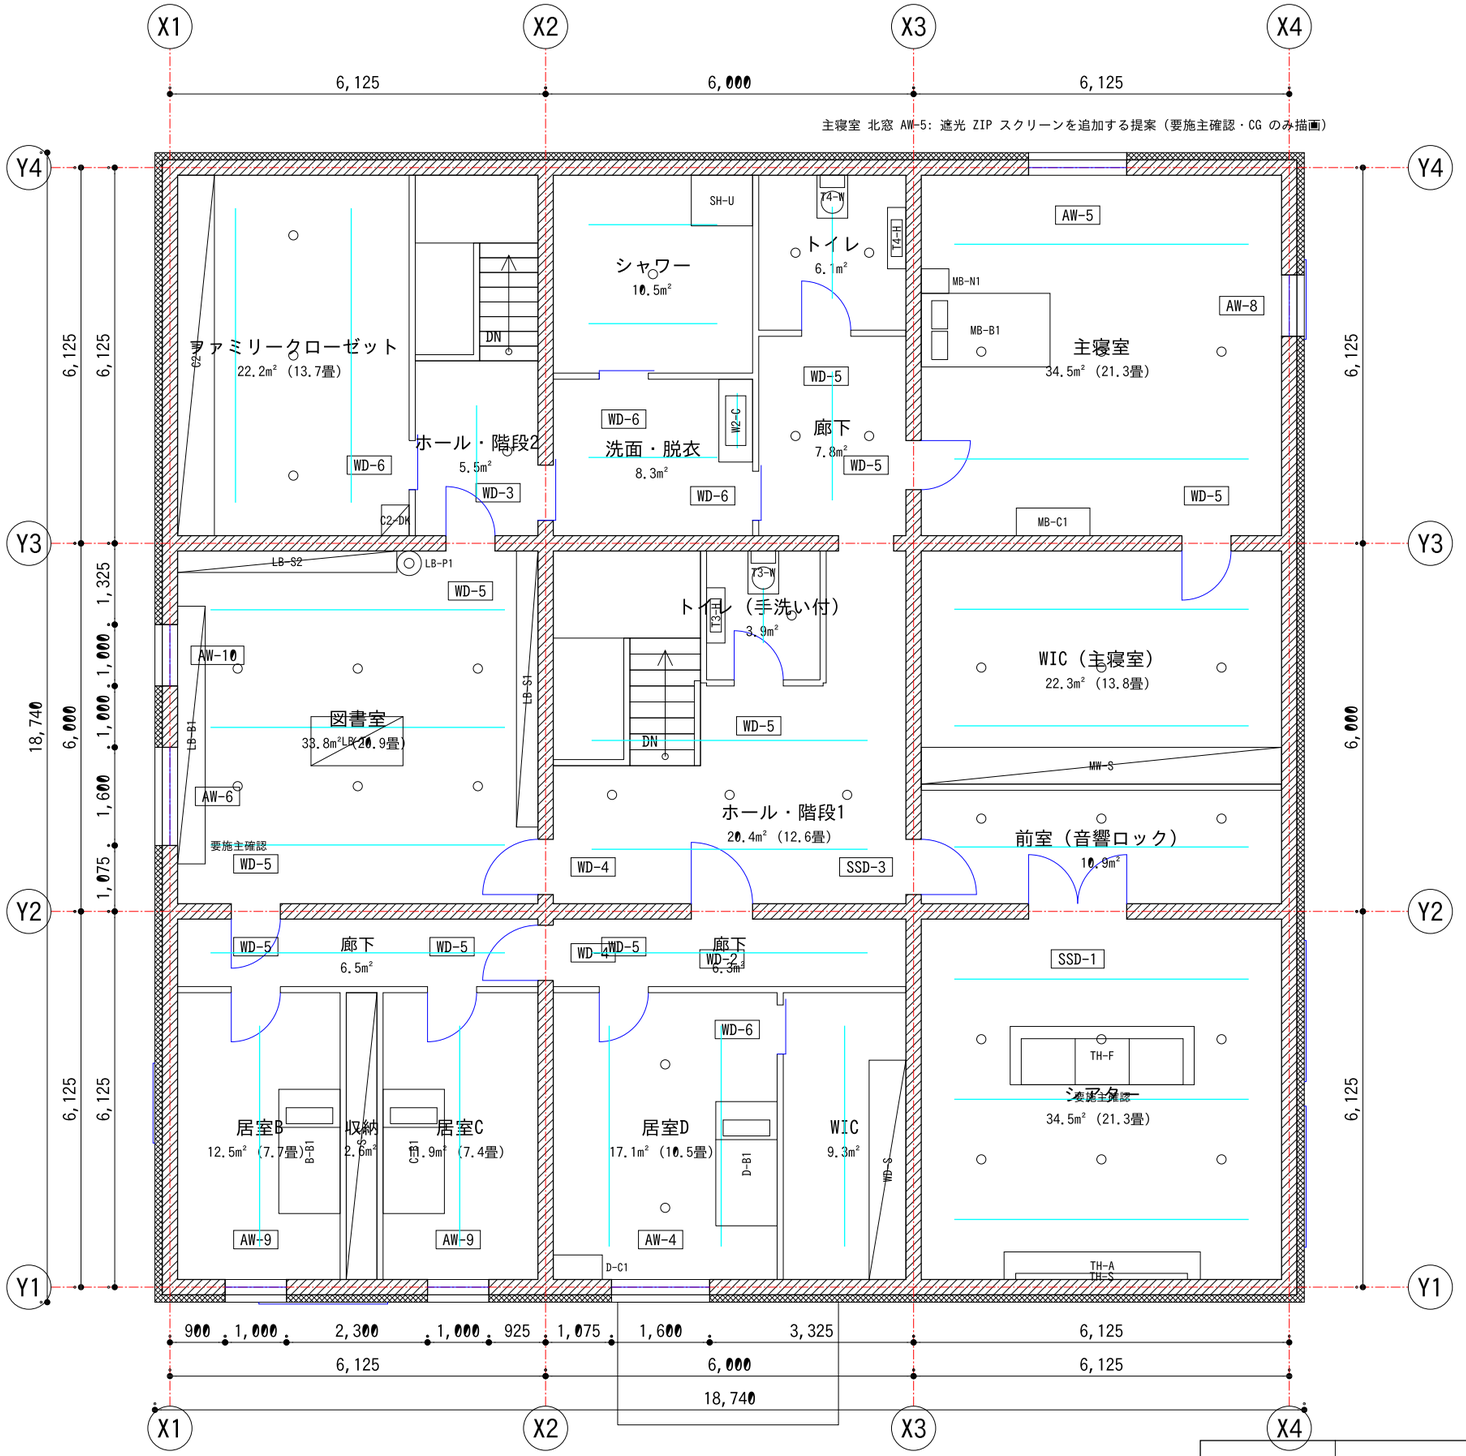


## 凡例・注記

- 家具（外形・細線）
- チェア（外形を塗り）
- 埋込ダウンライト（弱）φ100
- 直付ライン LED（主照明）
- 階段の足元灯（踏面+300）
- テーブルの脚位置・物干しパイプ
- 開き戸の軌跡

N

真北 12.3° 西振れ（建物は南側道路に平行）

## 仮置きの前提

家具は仮置き（後日差し替え）。指定商品（OSB テーブル・スクールチェア）の寸法は仮定（商品ページ未確認）。チェアは LDK の1脚のみ。色はいずれも仮定

ID は I-05 家具表の ID。収納は対角線、ベッドは枕の線、ソファは座クッションの割付を示す

床置きの家具は、台輪で床まで塞ぐ（掃除ロボット）、脚下 250mm 以上、洗面・手洗いは床から 650 浮かせる、のいずれか。壁との間は密着か 250mm 以上（頭・指が挟まるすき間をつくらない）

扉の軌跡と、扉・開口の前後 600 の通行帯には家具を置かない。コンセント・スイッチ（シャッター付き）は FL+250／FL+1,100、床コンセントなし

ジム機器は既存の配置のまま。安全帯（トレッドミル後方 2.0m）と重ねない

シアターの箱型ソファ・図書室の窓下ベンチは座る家具（要施主確認）。設定 furniture.optional_seating で一括して外せる

ベッドは1部屋1台。頭は窓のない壁側。チェア・スツールは LDK の1脚のほか置かない

# 2階 家具配置図（仮置き） S=1:100

2FL = 設計GL+4,700（TP+113.70）／天井高 CH=2,600／○ = 埋込ダウンライト（弱）、太線 = 直付ライン LED

| | | | | |
|---|---|---|---|---|
| 工事名称 | 河沿要（仮称）新築計画 | | | |
| 図面名称 | 2階 家具配置図（仮置き） | | | 図番 I-04 |
| 縮尺 | A3 1:100 | 日付 2026-10-03 | 設計 設計検討（仮） | |
| 段階 | 基本計画 ／ 本図は建築基準法令に基づく計画段階の検討図であり、確認申請・構造計算・関係機関協議により確定する | | | |

# 家具表・内装色彩計画 ― 家具は仮置き（後日差し替え）。指定商品の寸法は仮定、色はいずれも仮定

## (1) 家具表（建物座標・mm。座る家具は要施主確認）

| ID | 室 | 名称 | W×D×H(mm) | 数 | 材質・色 | 床との納まり |
|---|---|---|---|---|---|---|
| L-T1 | 1F リビング・ダイニング | マテリア ダイニングテーブル OSB 177.5cm ロの字脚 ブラック(スチール) カラー:ステンレス（指定・仮置き） | 1775×850×H720 | 1 | OSB t30（クリア塗装）＋ステンレス縁 #C9A878 | 脚（天板下690・ロの字脚） |
| L-C1 | 1F リビング・ダイニング | ペッパー スクールチェア チャコールブラウン（指定・仮置き） | 420×480×H780 | 1 | 座・背 合板（チャコールブラウン）／フレーム 鋼管（黒に近い暗褐色） #4A3F38 | 脚（座下430） |
| L-S1 | 1F リビング・ダイニング | サイドボード | 450×2350×H700 | 1 | アッシュ突板 #DCCFB9 | 台輪（H60） |
| L-K1 | 1F リビング・ダイニング | リビング収納 | 1575×450×H2600 | 1 | アッシュ突板 #DCCFB9 | 台輪（H60） |
| L-P1 | 1F リビング・ダイニング | 鉢植え | φ500×H1900 | 1 | 植物（鉢は生成り） #5D6B3A | 鉢を床に直置き |
| L-A1 | 1F リビング・ダイニング | アートパネル | W900×D30×H640 | 1 | アート（からし・オリーブ） #B8892D | 上に立て掛け・載せ置き |
| K-I1 | 1F キッチン | アイランドキッチン | 3000×1000×H900 | 1 | オリーブ色の扉 #5E6A3C | 台輪（H60） |
| K-B1 | 1F キッチン | 背面収納 | 3500×650×H2600 | 1 | アッシュ突板 #DCCFB9 | 台輪（H60） |
| P-S1 | 1F パントリー | パントリー収納 | 450×4650×H2600 | 1 | アッシュ突板 #DCCFB9 | 台輪（H60） |
| G-S1 | 1F 玄関土間 | 下足入れ | 450×1875×H2960 | 1 | アッシュ突板 #DCCFB9 | 台輪（H60） |
| G-B1 | 1F 玄関土間 | 腰掛けベンチ | 700×1375×H420 | 1 | アッシュ突板 #DCCFB9 | 台輪（H60） 要施主確認 |
| H-S1 | 1F ホール | ホール収納 | 450×1800×H2600 | 1 | アッシュ突板 #DCCFB9 | 台輪（H60） |
| H-S2 | 1F ホール | コート収納 | 450×1800×H2600 | 1 | アッシュ突板 #DCCFB9 | 台輪（H60） |
| J-M1 | 1F ジム | 鏡 | 1700×60×H2000 | 1 | 鏡 #E8ECEC | 突っ張り枠 |
| J-K1 | 1F ジム | 測定コーナーのカウンター | 450×700×H900 | 1 | アッシュ突板 #DCCFB9 | 台輪（H60） |
| T1-W | 1F トイレ（手洗い付） | タンク式便器 | 500×700×H800 | 1 | 陶器 #F5F4F0 | 床置き |
| T1-H | 1F トイレ（手洗い付） | 手洗いカウンター | 300×900×H850 | 1 | 人造大理石（一体成形） #EEEAE2 | 浮かせ（下端 FL+650） |
| T2-W | 1F トイレ | タンク式便器 | 500×700×H800 | 1 | 陶器 #F5F4F0 | 床置き |
| T2-H | 1F トイレ | 手洗いカウンター | 300×1000×H850 | 1 | 人造大理石（一体成形） #EEEAE2 | 浮かせ（下端 FL+650） |
| W1-C | 1F 洗面・脱衣 | 洗面カウンター | 550×1350×H850 | 1 | 人造大理石（一体成形） #EEEAE2 | 浮かせ（下端 FL+650） |
| W1-S | 1F 洗面・脱衣 | リネン収納 | 1600×450×H2600 | 1 | アッシュ突板 #DCCFB9 | 台輪（H60） |
| B1-U | 1F 浴室 | ユニットバスの浴槽 | 1800×825×H550 | 1 | ユニットバス #F1EFEA | ユニット |
| R-WD | 1F ランドリー・室内干し | ドラム式洗濯乾燥機 ×2 | 1300×720×H1060 | 2 | 家電（白） #EDEDEA | 床置き |
| R-SK | 1F ランドリー・室内干し | 作業カウンター＋スロップシンク | 2300×650×H900 | 1 | 人造大理石（一体成形） #EEEAE2 | 台輪（H60） |
| R-DK | 1F ランドリー・室内干し | 掃除ロボットのドック | 450×500×H600 | 1 | 家電（白） #EDEDEA | 床置き |
| R-HP | 1F ランドリー・室内干し | 物干しパイプ | 3600×800×H30 | 2 | ステンレス | 天井から吊り |
| C1-W | 1F ファミリークローゼット | 収納 | 600×3025×H2600 | 1 | アッシュ突板 #DCCFB9 | 台輪（H60） |
| C1-N | 1F ファミリークローゼット | 収納 | 3175×600×H2600 | 1 | アッシュ突板 #DCCFB9 | 台輪（H60） |
| M1-A | 1F 機械室（西系統） | 空調機・全熱交換器 | 2850×1200×H1900 | 1 | 機器（灰） #C9C8C2 | 床置き |
| M2-A | 1F 機械室（東系統） | 浄水器・ラック・蓄電池 | 2125×1000×H1900 | 1 | 機器（灰） #C9C8C2 | 床置き |
| WA-S | 1F WIC | 棚・パイプ | 3825×600×H2600 | 1 | アッシュ突板 #DCCFB9 | 台輪（H60） |
| A-B1 | 1F 居室A | ベッド シングル 1000×2000 | 1000×2025×H520 | 1 | オーク突板 #C2A07A | 脚下260 |
| A-C1 | 1F 居室A | チェスト | 800×400×H700 | 1 | アッシュ突板 #DCCFB9 | 台輪（H60） |
| B-B1 | 2F 居室B | ベッド シングル | 1000×2025×H520 | 1 | オーク突板 #C2A07A | 脚下260 |
| C-B1 | 2F 居室C | ベッド シングル | 1000×2025×H520 | 1 | オーク突板 #C2A07A | 脚下260 |
| D-B1 | 2F 居室D | ベッド シングル | 1000×2025×H520 | 1 | オーク突板 #C2A07A | 脚下260 |
| D-C1 | 2F 居室D | チェスト | 800×400×H700 | 1 | アッシュ突板 #DCCFB9 | 台輪（H60） |
| WD-S | 2F WIC | 棚・パイプ | 600×3575×H2600 | 1 | アッシュ突板 #DCCFB9 | 台輪（H60） |
| S-S | 2F 収納 | 収納棚 | 500×4675×H2600 | 1 | アッシュ突板 #DCCFB9 | 台輪（H60） |
| TH-S | 2F シアター | スクリーン 120型 | 2800×100×H1700 | 1 | スクリーン（白） #F4F4F2 | 突っ張り枠 |
| TH-A | 2F シアター | AV ボード | 3200×450×H450 | 1 | AV 台（暗褐色） #4E4A44 | 台輪（H60） |
| TH-F | 2F シアター | 箱型ソファ 3人掛け | 3000×950×H780 | 1 | 布張り（オリーブ） #56603A | 台輪（H60） 要施主確認 |
| LB-S1 | 2F 図書室 | 本棚 | 350×4500×H2600 | 1 | オーク突板 #C2A07A | 台輪（H60） |
| LB-S2 | 2F 図書室 | 本棚 | 3575×350×H2600 | 1 | オーク突板 #C2A07A | 台輪（H60） |
| LB-B1 | 2F 図書室 | 窓下の造作ベンチ | 4500×4200×H420 | 1 | オーク突板 #C2A07A | 台輪（H60） 要施主確認 |
| LB-T1 | 2F 図書室 | 閲覧台 | 1500×800×H950 | 1 | オーク突板 #C2A07A | 台輪（H60） |
| LB-P1 | 2F 図書室 | 鉢植え | φ400×H1500 | 1 | 植物（鉢は生成り） #5D6B3A | 鉢を床に直置き |
| MB-B1 | 2F 主寝室 | ベッド セミダブル 1200×2000 | 2100×1200×H520 | 1 | オーク突板 #C2A07A | 脚下260 |
| MB-N1 | 2F 主寝室 | ナイトテーブル | 450×400×H450 | 1 | アッシュ突板 #DCCFB9 | 台輪（H60） |
| MB-C1 | 2F 主寝室 | チェスト | 1200×450×H700 | 1 | アッシュ突板 #DCCFB9 | 台輪（H60） |
| MW-S | 2F WIC（主寝室） | 棚 | 5875×600×H2600 | 1 | アッシュ突板 #DCCFB9 | 台輪（H60） |
| C2-W | 2F ファミリークローゼット | 収納 | 600×5875×H2600 | 1 | アッシュ突板 #DCCFB9 | 台輪（H60） |
| C2-DK | 2F ファミリークローゼット | 掃除ロボットのドック | 450×500×H600 | 1 | 家電（白） #EDEDEA | 床置き |
| W2-C | 2F 洗面・脱衣 | 洗面カウンター | 550×1350×H850 | 1 | 人造大理石（一体成形） #EEEAE2 | 浮かせ（下端 FL+650） |
| T3-W | 2F トイレ（手洗い付） | タンク式便器 | 500×700×H800 | 1 | 陶器 #F5F4F0 | 床置き |
| T3-H | 2F トイレ（手洗い付） | 手洗いカウンター | 300×900×H850 | 1 | 人造大理石（一体成形） #EEEAE2 | 浮かせ（下端 FL+650） |
| T4-W | 2F トイレ | タンク式便器 | 500×700×H800 | 1 | 陶器 #F5F4F0 | 床置き |
| T4-H | 2F トイレ | 手洗いカウンター | 300×1000×H850 | 1 | 人造大理石（一体成形） #EEEAE2 | 浮かせ（下端 FL+650） |
| SH-U | 2F シャワー | シャワーユニット | 1000×825×H2000 | 1 | ユニットバス #F1EFEA | ユニット |

## (2) 指定商品2点 ― 寸法・色・解釈はすべて仮定（商品ページ未確認。要施主確認）

| 商品 | 仮定した寸法・形 | 色・材質（仮定） | 解釈・要確認 |
|---|---|---|---|
| マテリア ダイニングテーブル OSB 177.5cm ロの字脚 ブラック(スチール) カラー:ステンレス | 外寸 W1,775×D850×H720。天板 OSB t30。ロの字脚 2組（角パイプ □40、天板端から 100 内側）。天板下に □20×40 の補強2本 | 天板: OSB・クリア塗装（#C9A878 の平均色）。脚: 黒の粉体塗装 #1F1E1C。縁: ステンレス（ヘアライン） | 「カラー:ステンレス」は 天板の木口に巻いたステンレス縁（採用）。ほかの解釈（脚／天板色）は spec.yaml furniture.products.table_osb.stainless_part で切替。奥行・高さ・厚さ・角パイプ寸法も要確認 |
| ペッパー スクールチェア チャコールブラウン | 外寸 W420×D480×H780、座面高 SH450。鋼管 φ22のフレーム、成形合板の座面 t12、湾曲した背板 t10（3分割で近似） | 座面・背板: チャコールブラウン #4A3F38。フレーム: #2B2622（暗褐色の粉体塗装） | 寸法（大人用の学童椅子型）・形・フレーム色（チャコールブラウンか、木部はナチュラルか）を要確認。LDK に1脚だけ |

## (3) 内装パレット（sRGB。いずれも仮定。実物の見本板で確認）

| キー | 部位 | 仕上げ | 色 | 見本 |
|---|---|---|---|---|
| wall_paint | 壁 | PB＋耐汚染塗装（拭き取り可） | #F1EDE4 | |
| ceiling_paint | 天井 | PB＋EP（フラット・溝なし）＋直付ライン LED（主）・埋込 LED（弱） | #F4F2EC | |
| floor_oak | 床 居室・LDK・キッチン・図書室・階段 | 複合フローリング（ノンワックス・ややつや） | #BFA383 | |
| floor_sheet | 床 トイレ・洗面・ランドリー・浴室 | 塩ビシームレスシート（石目調） | #D6D0C3 | |
| floor_tile_genkan | 床 玄関土間 | 大判磁器タイル 600角・細目地 | #B9B2A4 | |
| floor_rubber | 床 ジム | ゴムシート t15（灰色。黒にしない） | #7C7970 | |
| floor_carpet | 床 シアター・前室 | タイルカーペット（暗すぎない） | #77705F | |
| wall_theater | 壁 シアター・前室 | PET 吸音ボード | #5A554D | |
| ceiling_theater | 天井 シアター | 吸音 PB（映写のため暗め） | #45423D | |
| wainscot_gym | 腰 ジム H1,200 | 耐衝撃化粧パネル | #DAD4C6 | |
| wainscot | 腰 トイレ・玄関 H1,000 | 化粧パネル | #E3DCCD | |
| wet_panel | 壁 洗面・ランドリー・浴室 | 耐水化粧パネル（目地なし） | #F3F0EA | |

| キー | 部位 | 仕上げ | 色 | 見本 |
|---|---|---|---|---|
| door_oak | 内部建具 | オーク突板（現行 #73614D を置き換える提案） | #C8B394 | |
| kamachi | 框・窓台 | 人造大理石 | #E9E3D6 | |
| nosing | 段鼻の色差 | 階段・框に幅30 | #7A6650 | |
| handrail | 手すり | オーク φ35 | #B08A5E | |
| case_ash | 造作収納の扉 | アッシュ突板 | #DCCFB9 | |
| case_oak | 本棚・ベッド・ベンチ | オーク | #C2A07A | |
| olive_case | アイランドの扉 | オリーブ色（外観のアソートに合わせる） | #5E6A3C | |
| sofa_olive | ソファ・ジムのパッド | 布張り（オリーブ） | #56603A | |
| osb | 指定: テーブル天板 | OSB t30 クリア塗装（仮定） | #C9A878 | |
| steel_black | 指定: テーブル脚 | 鋼管 □40 黒の粉体塗装（仮定） | #1F1E1C | |
| chair_wood | 指定: チェア座・背 | 合板 チャコールブラウン（仮定） | #4A3F38 | |
| chair_frame | 指定: チェアのフレーム | 鋼管 φ22 暗褐色（仮定） | #2B2622 | |

| | | | | |
|---|---|---|---|---|
| 工事名称 | 河沿要（仮称）新築計画 | | | |
| 図面名称 | 家具表・内装色彩計画（仮置き） | | | 図番 I-05 |
| 縮尺 | A3 ― | 日付 2026-10-03 | 設計 設計検討（仮） | |
| 段階 | 基本計画 ／ 本図は建築基準法令に基づく計画段階の検討図であり、確認申請・構造計算・関係機関協議により確定する | | | |

# 館内 Wi-Fi 電波計画 ― 5GHz 帯で受信 -67dBm 以上を床面の98%以上（壁の減衰込みの概算）

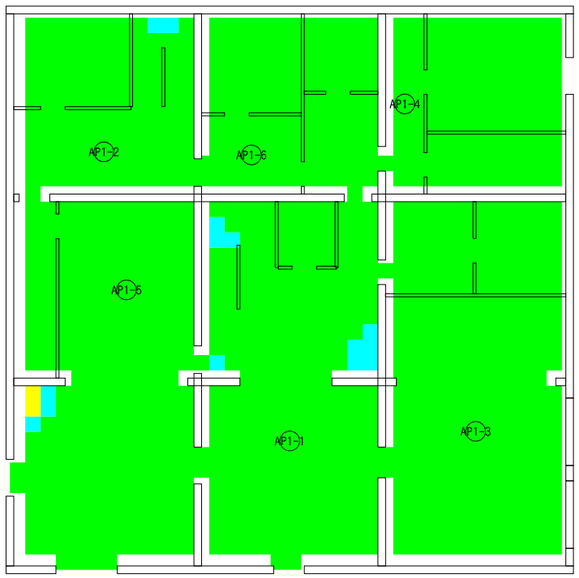


1階（AP 6台・目標を満たす面積 100%）

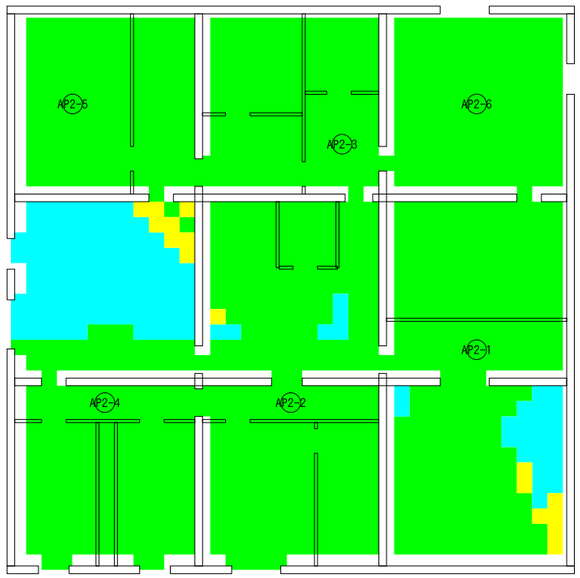


2階（AP 6台・目標を満たす面積 99%）

- -60dBm 以上（高速）
- -67～-60dBm（快適）
- -75～-67dBm（つながるが遅い）
- -75dBm 未満（不安定）

## (1) アクセスポイント

| AP | 設置位置（天井） | 階 |
|---|---|---|
| AP1-1 | ホール | 1F |
| AP1-2 | ランドリー・室内干し | 1F |
| AP1-3 | ジム | 1F |
| AP1-4 | 廊下 | 1F |
| AP1-5 | キッチン | 1F |
| AP1-6 | 洗面・脱衣 | 1F |
| AP2-1 | 前室（音響ロック） | 2F |
| AP2-2 | 廊下 | 2F |
| AP2-3 | 廊下 | 2F |
| AP2-4 | 廊下 | 2F |
| AP2-5 | ファミリークローゼット | 2F |
| AP2-6 | 主寝室 | 2F |

## 計画の考え方

機器: Wi-Fi 7（6GHz/5GHz/2.4GHz）天井埋込 AP・PoE＋・有線バックホール（Cat6A）。各 AP は PoE＋の有線（Cat6A）で機械室（東系統）のネットワークラックに集める（無線中継に頼らない）

壁式 RC は内部の耐力壁も RC 250mm で、5GHz は1枚で約25dB 減衰する。床スラブも厚いため、各階に AP を置き、RC 壁で囲まれた区画ごとに電波を届ける

計算: 送信 20dBm、自由空間損失＋通過する壁の減衰（RC 25dB・間仕切 4dB・扉 4dB・透明扉 3dB）。0.5m メッシュで受信強度を求め、目標を満たす面積が最大になる位置に AP を1台ずつ追加

シアター・ジムは遮音のため扉が重く、それぞれ室内に AP を置くと安定する（必要に応じて実施設計で追加）。外構（菜園・駐車場）は屋外用 AP を別途

実施設計で、機種の送信出力・アンテナ特性を用いて現地測定（竣工後のサイトサーベイ）で確認する

| | | | | |
|---|---|---|---|---|
| 工事名称 | 河沿要（仮称）新築計画 | | | |
| 図面名称 | Wi-Fi 電波計画 | | | 図番 E-01 |
| 縮尺 | A3　1:200 | 日付　2026-10-03 | 設計　設計検討（仮） | |
| 段階 | 基本計画　／　本図は建築基準法令に基づく計画段階の検討図であり、確認申請・構造計算・関係機関協議により確定する | | | |

# 制御・照明・掃除ロボット計画 ― スクリーン・照明・空調・ロボットを bot から操作できる共通の制御基盤

## (1) 制御の構成

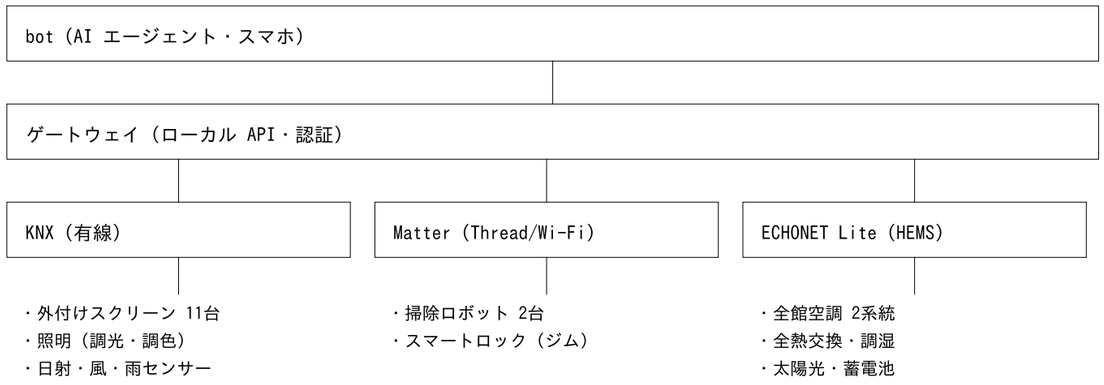


優先順位：強風・凍結・火災・停電時は自動制御・手元スイッチが bot の指令より優先

| 対象 | 機器 | 操作 | 優先・安全 |
|---|---|---|---|
| 外付けスクリーン | 南・東・西の窓 11台。モーターは KNX/Matter 対応、位置（%）を返す | 自動（日射・風センサー）／bot（API）／手元スイッチ | 強風・凍結時の巻上げが最優先。次に手元スイッチ、bot、自動スケジュールの順 |
| 照明 | 全室 調光・調色 LED（DALI-2 DT8 → KNX） | 時刻スケジュール／bot／壁スイッチ・人感 | 壁スイッチが bot より優先。停電時は非常照明 |
| 空調・換気 | 全館空調2系統・全熱交換・調湿（ECHONET Lite） | 温湿度センサー／bot | 排煙・火災時は防災設備が優先 |
| 掃除ロボット | 各階1台・自動ゴミ収集・給排水直結ドック | スケジュール（不在時）／bot | 就寝・在室中の室は避ける。階段の手前で停止 |
| 防犯・車両 | 電動スライド門扉・電動昇降ボラード・赤外線カメラ・ビームセンサー | スケジュール（夜間・不在時はボラード上げ）／bot | 人・車を検知したらボラードは上げない（挟まれ防止）。停電時は門扉を内側から手動解錠 |
| ネットワーク | 天井 AP（PoE+）・機械室（東系統）にラック・UPS | ― | 制御機器は別ネットワーク（VLAN）に分け、API は認証付き |

## (3) 掃除ロボット（床清掃はロボットが行う）

| 階 | 清掃範囲 | 室数 | ドック |
|---|---|---|---|
| 1F | 247m² | 15 | ランドリー・室内干し |
| 2F | 276m² | 19 | ファミリークローゼット |

段差は5mm以下（引戸レール・床見切りを含む）。玄関框・階段は越えない（各階に1台）
床に配線を這わせない（コンセントは家具の高さ・床コンセントなし）
家具は台輪で床まで塞ぐか、脚下 250mm 以上（ロボットが入れ、子どもの頭が挟まらない寸法）
黒い床・敷物は避ける（段差センサーの誤作動）。ラグは毛足の短いものを固定
ドック：1階 ランドリー、2階 ファミリークローゼット。自動ゴミ収集・給排水直結で水拭きの水替え不要
清掃時は bot が上吊り引戸を開けた状態を確認してから走らせる（戸は手動・自動とも可）

## (2) 照明の時刻スケジュール（全室共通の初期値・室ごと/bot で変更可）

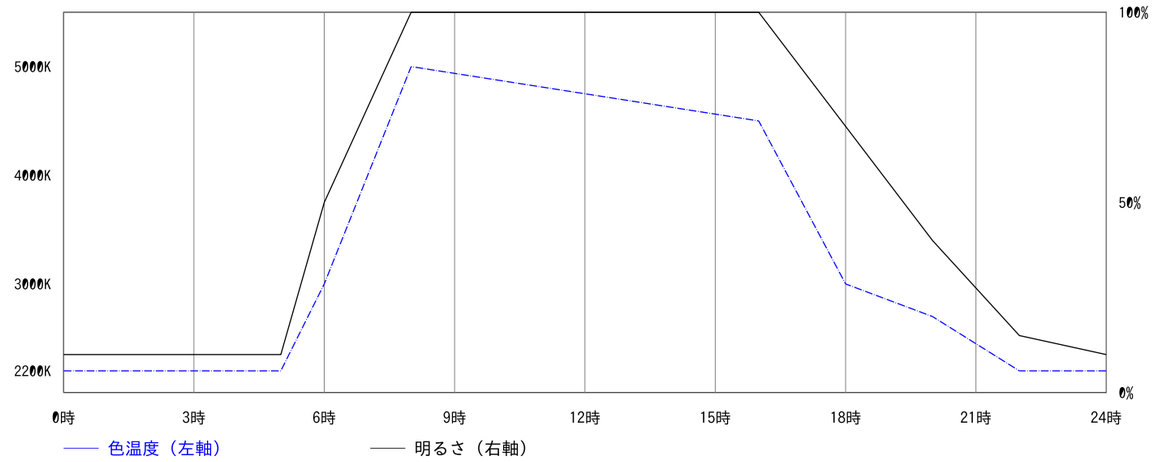


| 時刻 | 色温度 | 明るさ | ねらい |
|---|---|---|---|
| 0〜5時 | 2200K | 10% | 夜間の移動は足元だけ（眠りを妨げない） |
| 6〜8時 | 3000→5000K | 50→100% | 朝日に合わせて上げる（目覚め） |
| 8〜16時 | 5000→4500K | 100% | 昼の活動・ジム |
| 18〜22時 | 3000→2200K | 70→15% | 夕方から暖色・暗めへ（就寝前） |

## 照明の仕様

主照明は天井直付けのライン LED（調光 1〜100%・調色 2200〜5000K、DALI-2 DT8、製品未確定）、埋込ダウンライトは弱い補助灯（最大250lm・2200〜3000K）、階段は踏面から300の足元灯（停電時点灯）。L・D・F の3チャネルを時刻で自動変化させ、室ごと・bot から変更できる（E-04〜E-06）
シアターは上映時に自動で消灯・足元灯のみ。ジムは運動時 5000K・100%

## スクリーンの bot 制御

全11台を個別・グループ（方位・室）で操作でき、位置を bot に返す。日没後の自動降下で光漏れを防ぐ（虫を寄せない、E-03）
強風（10m/s 以上）・凍結時はセンサーで自動巻上げ、この間は bot の降下指令を受け付けない

| | | | | |
|---|---|---|---|---|
| 工事名称 | 河沿要（仮称）新築計画 | | | |
| 図面名称 | 制御・照明・掃除ロボット計画 | | | 図番 E-02 |
| 縮尺 | A3 ― | 日付 2026-10-03 | 設計 設計検討（仮） | |
| 段階 | 基本計画 ／ 本図は建築基準法令に基づく計画段階の検討図であり、確認申請・構造計算・関係機関協議により確定する | | | |

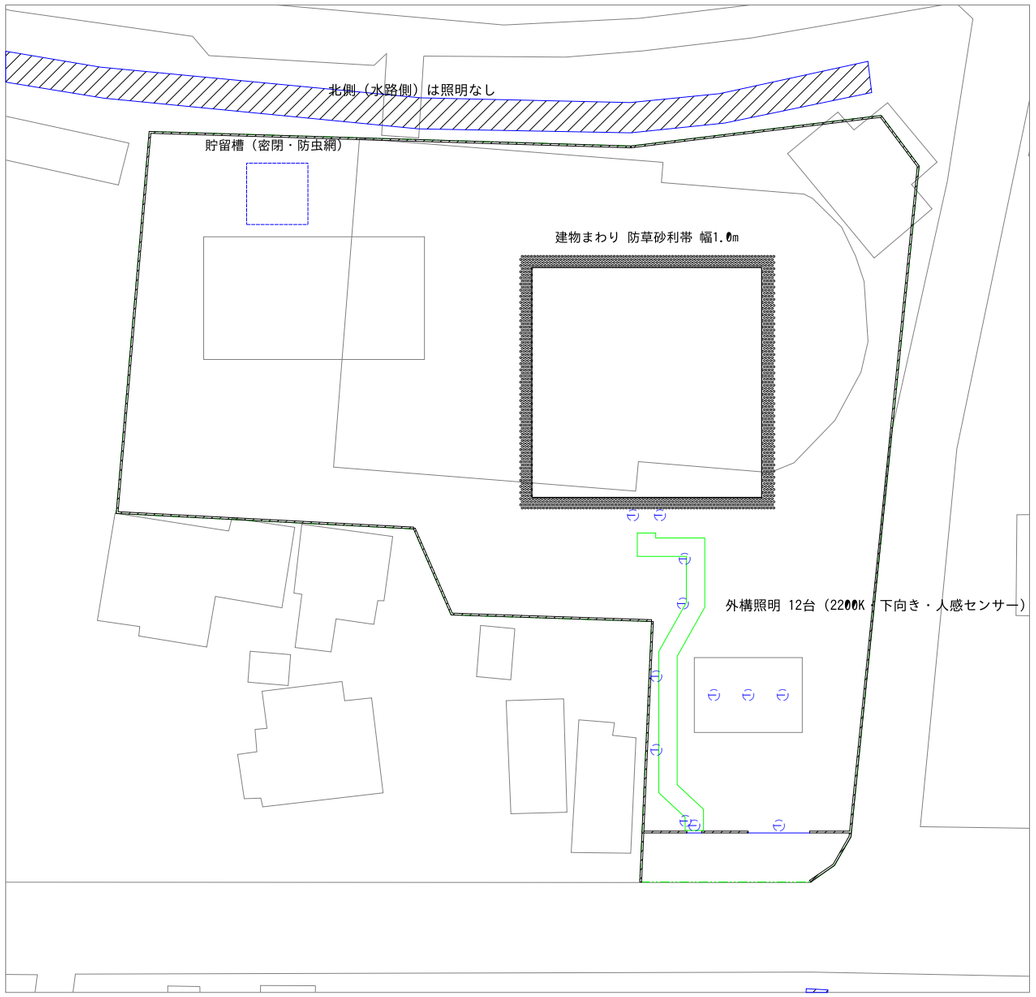


## 防虫の工夫

| 項目 | 虫を寄せない・発生させない工夫 |
|---|---|
| 光の色 | 外構照明は 2200K（アンバー寄り）の LED。虫が集まりやすい紫外線・青色光をほとんど含まない |
| 光の向き | 上向きの光なし（全カットオフ）。H600 のボラードと足元灯で地面だけを照らす。玄関ドアの真上・窓際に光源を置かない |
| 点灯時間 | 人感センサー＋タイマー。必要なときに必要な所だけ点ける。北側（水路側）には照明を設けない |
| 室内の光漏れ | 日没後は外付けスクリーンを自動で下ろし（bot 制御）、室内の光を外に出さない |
| たまり水 | 地下貯留槽は密閉・通気口と越流管に防虫網。樋・パーゴラの雨どいは勾配をとり水を溜めない。透水舗装で水たまりをつくらない |
| 建物まわり | 外壁の足元に幅1.0m の防草砂利帯（草・落ち葉・湿気を建物に寄せない） |
| 菜園・ごみ | 堆肥は密閉式コンポスト。生ごみは蓋付きの保管庫。作物には防虫ネット |
| 換気・排水 | 給排気フードに防虫網（全熱交換のフィルターと併用）。排水はトラップで封水、床下ピットは密閉 |
| 開口部 | 窓は FIX（網戸不要）。玄関ドアは気密パッキン。玄関の明かりは庇下の低い足元灯 |

## 外構照明の器具

| 器具 | 台数 | 仕様 |
|---|---|---|
| ボラード | 5 | 2200K・全カットオフ・人感・H600 |
| 足元灯 | 2 | 2200K・全カットオフ・人感 |
| カーポート下 ダウンライト | 3 | 2200K・全カットオフ・人感 |
| 門灯 | 2 | 2200K・全カットオフ・人感 |

N

真北 12.3° 西振れ（建物は南側道路に平行）

外構照明・防虫計画図 S=1:500

| | | | | |
|---|---|---|---|---|
| 工事名称 | 河沿要（仮称）新築計画 | | | |
| 図面名称 | 外構照明・防虫計画図 | | | 図番 E-03 |
| 縮尺 | A3 1:500 | 日付 2026-10-03 | 設計 設計検討（仮） | |
| 段階 | 基本計画 ／ 本図は建築基準法令に基づく計画段階の検討図であり、確認申請・構造計算・関係機関協議により確定する | | | |

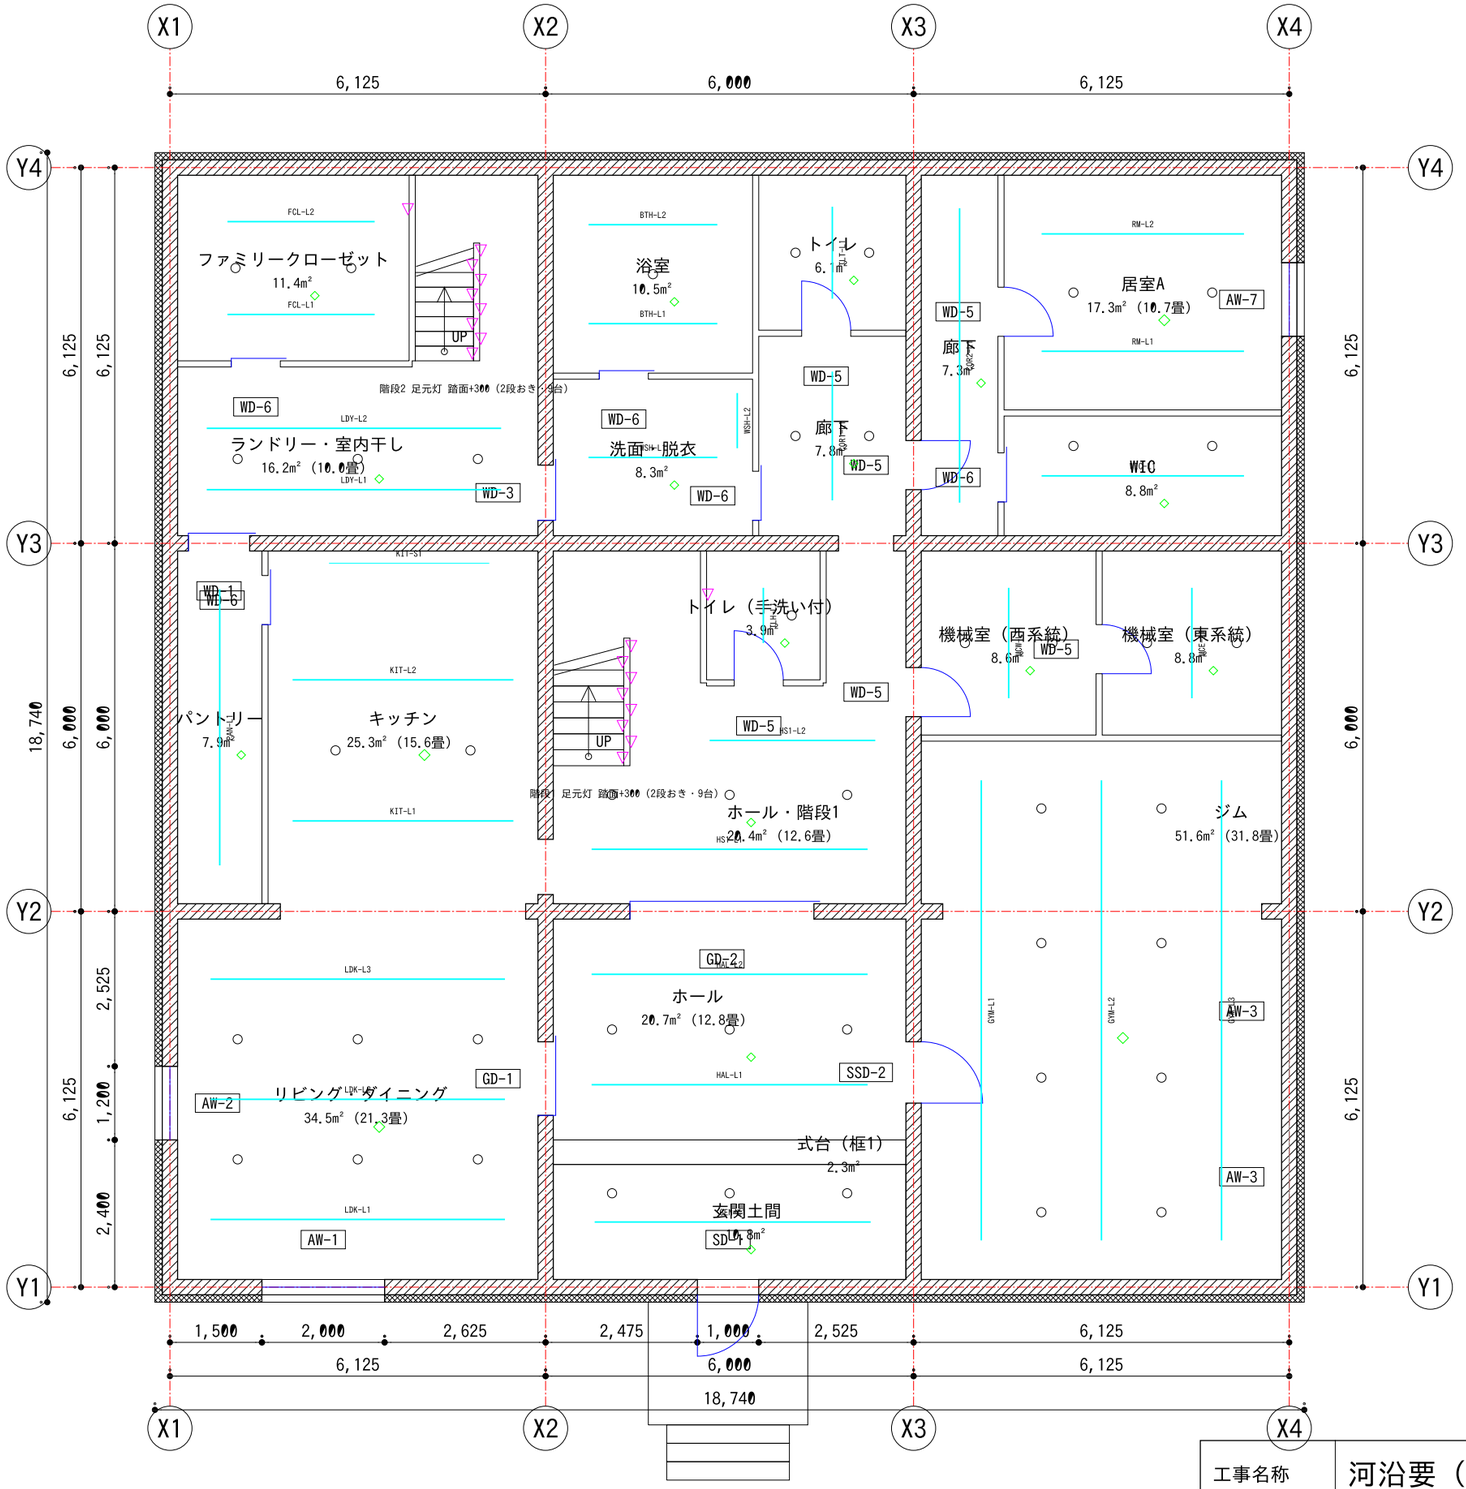


## 凡例

- 直付ライン LED（主照明・天井面に直付け）
- 埋込ダウンライト（弱い補助灯 最大2500lm）○
- 階段の足元灯（踏面から300）▼
- 人感／在室センサー ◇

N

真北 12.3° 西振れ（建物は南側道路に平行）

## 計画の考え方

主照明は天井面に直付けする棒状（ライン）LED（乳白カバー・連結部が目立たない側面発光）。埋込ダウンライトは夕方〜夜の弱い補助灯。コーブ（溝）・吊り器具はつくらない

ライン列は室の長手方向に平行。階段の吹抜け・天井まで届く家具の範囲は 150 離して切る。ダウンライトはライン軸から 450 以上・壁から 400 以上

六角形の連結照明は実在するが壁用・装飾用で天井の主照明に適さないため不採用（E-06）。製品は未確定で、数値は仮定値

センサー：人感（PIR）は廊下・水回り・収納・ホール・階段、在室（ミリ波）は居室・LDK・ジム・図書室・シアター

階段の足元灯は壁（LGS の手すり壁の両面・踊場の間仕切）に埋込。停電時は内蔵電池で自動点灯（30分以上と仮定）

| 器具 ID | 長さ | lm/m | 器具数 |
|---|---|---|---|
| 1F-LDK-L1 | 4,800 | 2,000 | 2 |
| 1F-LDK-L2 | 4,800 | 2,000 | 2 |
| 1F-LDK-L3 | 4,800 | 2,000 | 2 |
| 1F-KIT-L1 | 3,600 | 3,000 | 2 |
| 1F-KIT-L2 | 3,600 | 3,000 | 2 |
| 1F-KIT-S1 | 2,600 | 1,000 | 2 |
| 1F-PAN-L1 | 4,500 | 1,600 | 2 |
| 1F-GEN-L1 | 4,500 | 2,000 | 2 |
| 1F-HAL-L1 | 4,500 | 1,600 | 2 |
| 1F-HAL-L2 | 4,500 | 1,600 | 2 |
| 1F-GYM-L1 | 7,500 | 3,000 | 4 |
| 1F-GYM-L2 | 7,500 | 3,000 | 4 |
| 1F-GYM-L3 | 7,500 | 3,000 | 4 |
| 1F-HS1-L1 | 4,500 | 1,600 | 2 |
| 1F-HS1-L2 | 2,700 | 1,600 | 2 |
| 1F-TLH-L1 | 900 | 3,500 | 1 |
| 1F-MCW-L1 | 1,800 | 3,500 | 1 |
| 1F-MCE-L1 | 1,800 | 3,500 | 1 |
| 1F-LDY-L1 | 4,800 | 2,000 | 2 |
| 1F-LDY-L2 | 4,800 | 2,000 | 2 |
| 1F-FCL-L1 | 2,400 | 2,000 | 1 |
| 1F-FCL-L2 | 2,400 | 2,000 | 1 |
| 1F-WSH-L1 | 2,100 | 3,500 | 1 |
| 1F-WSH-L2 | 900 | 1,500 | 1 |
| 1F-BTH-L1 | 2,100 | 2,000 | 1 |
| 1F-BTH-L2 | 2,100 | 2,000 | 1 |
| 1F-COR1-L1 | 2,100 | 1,600 | 1 |
| 1F-TLT-L1 | 1,500 | 3,500 | 1 |
| 1F-RM-L1 | 3,300 | 2,000 | 2 |
| 1F-RM-L2 | 3,300 | 2,000 | 2 |
| 1F-WIC-L1 | 3,300 | 2,500 | 2 |
| 1F-COR2-L1 | 4,800 | 600 | 2 |

## 照明配置図（1階） S=1:100

1FL = 設計GL+1,500（TP+11000.50）／天井高 CH=2,600／製品未確定・仮定値

| | | | | |
|---|---|---|---|---|
| 工事名称 | 河沿要（仮称）新築計画 | | | |
| 図面名称 | 照明配置図（1階） | | | 図番 E-04 |
| 縮尺 | A3 1:100 | 日付 2026-10-03 | 設計 設計検討（仮） | |
| 段階 | 基本計画 ／ 本図は建築基準法令に基づく計画段階の検討図であり、確認申請・構造計算・関係機関協議により確定する | | | |

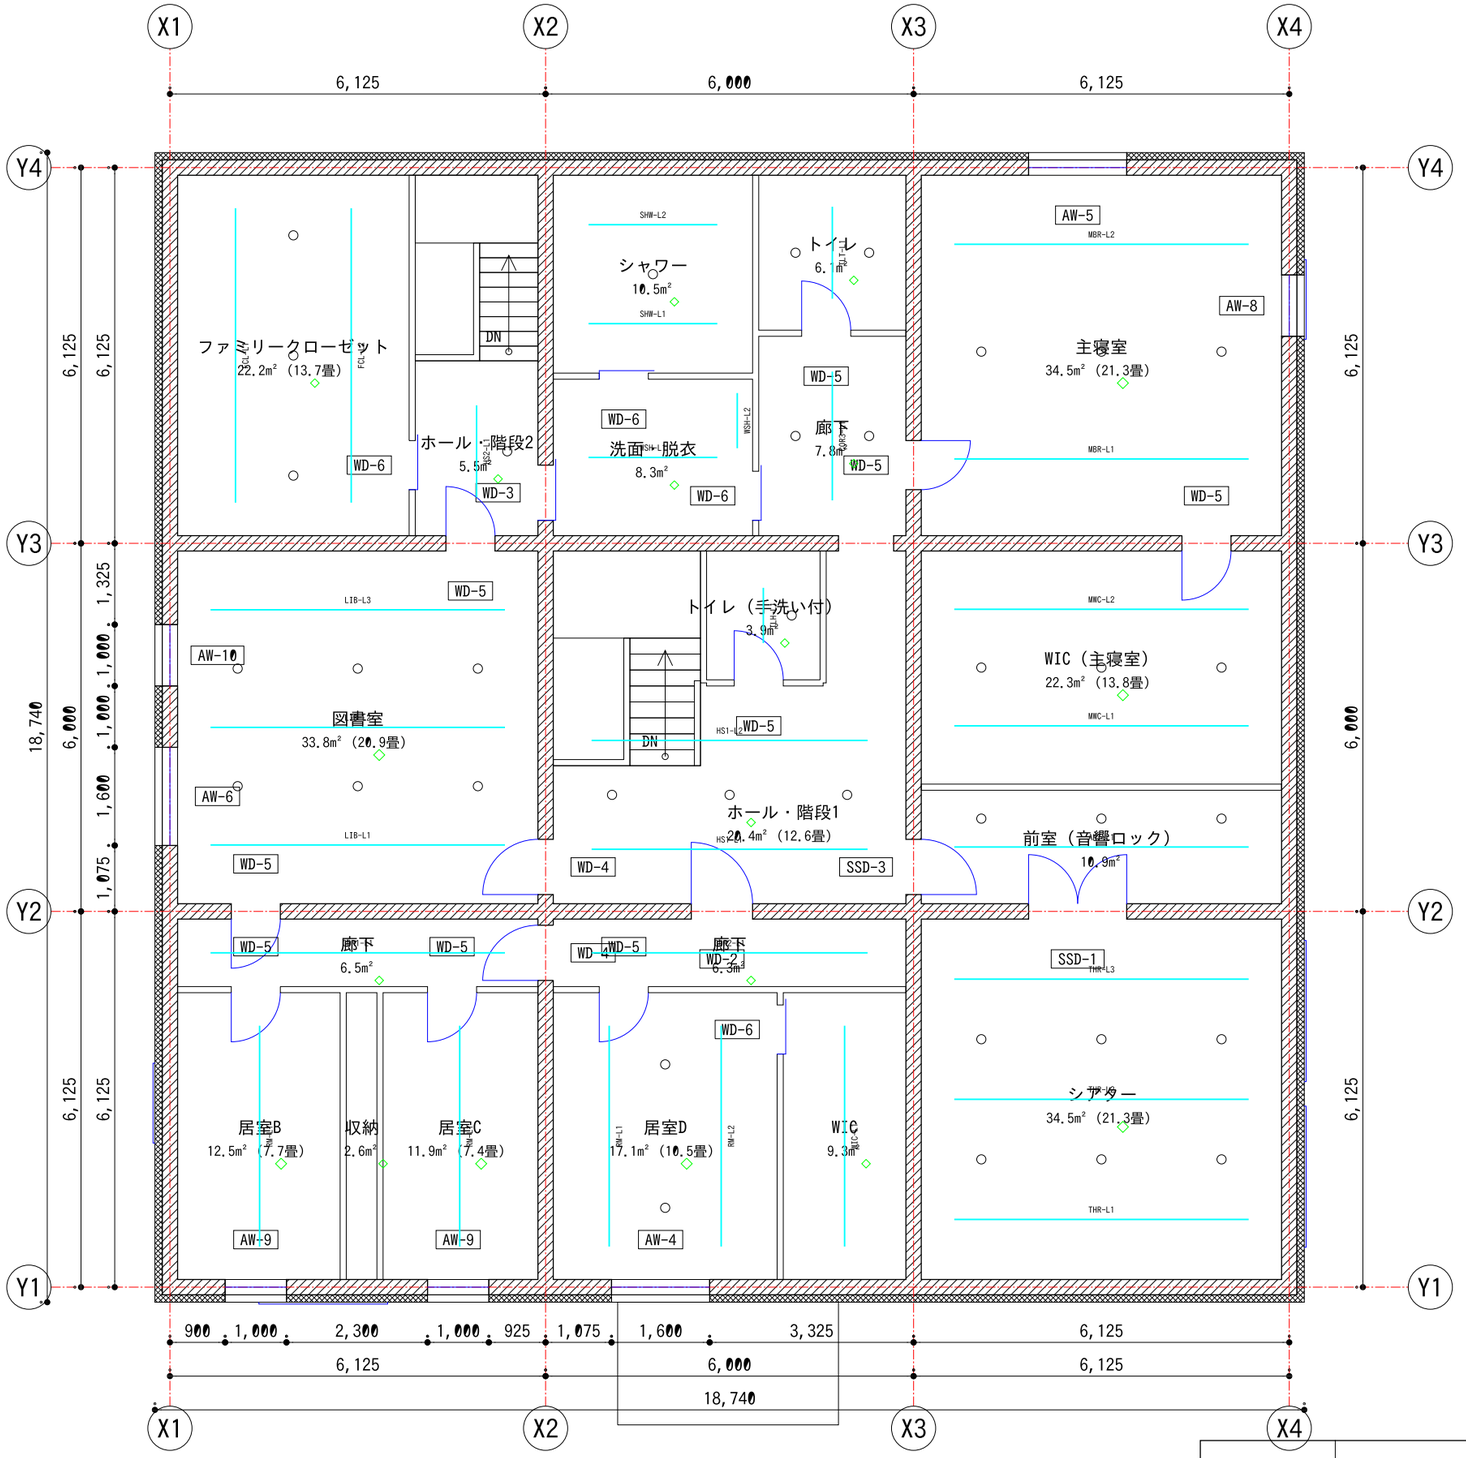


## 凡例

- 直付ライン LED（主照明・天井面に直付け）
- 埋込ダウンライト（弱い補助灯 最大250lm）○
- 階段の足元灯（踏面から300）▼
- 人感／在室センサー ◇

N

真北 12.3° 西振れ（建物は南側道路に平行）

## 計画の考え方

主照明は天井面に直付けする棒状（ライン）LED（乳白カバー・連結部が目立たない側面発光）。埋込ダウンライトは夕方〜夜の弱い補助灯。コーブ（溝）・吊り器具はつくらない

ライン列は室の長手方向に平行。階段の吹抜け・天井まで届く家具の範囲は 150 離して切る。ダウンライトはライン軸から 450 以上・壁から 400 以上

六角形の連結照明は実在するが壁用・装飾用で天井の主照明に適さないため不採用（E-06）。製品は未確定で、数値は仮定値

センサー：人感（PIR）は廊下・水回り・収納・ホール・階段、在室（ミリ波）は居室・LDK・ジム・図書室・シアター

| 器具 ID | 長さ | lm/m | 器具数 |
|---|---|---|---|
| 2F-RM-L1 | 3,600 | 2,500 | 2 |
| 2F-RM-L1 | 3,600 | 2,500 | 2 |
| 2F-COR1-L1 | 4,800 | 600 | 2 |
| 2F-RM-L1 | 3,600 | 1,600 | 2 |
| 2F-RM-L2 | 3,600 | 1,600 | 2 |
| 2F-WIC-L1 | 3,600 | 2,000 | 2 |
| 2F-COR2-L1 | 4,500 | 600 | 2 |
| 2F-THR-L1 | 4,800 | 2,500 | 2 |
| 2F-THR-L2 | 4,800 | 2,500 | 2 |
| 2F-THR-L3 | 4,800 | 2,500 | 2 |
| 2F-ANT-L1 | 4,800 | 1,000 | 2 |
| 2F-MWC-L1 | 4,800 | 1,600 | 2 |
| 2F-MWC-L2 | 4,800 | 1,600 | 2 |
| 2F-LIB-L1 | 4,800 | 2,000 | 2 |
| 2F-LIB-L2 | 4,800 | 2,000 | 2 |
| 2F-LIB-L3 | 4,800 | 2,000 | 2 |
| 2F-HS1-L1 | 4,500 | 1,200 | 2 |
| 2F-HS1-L2 | 4,500 | 1,200 | 2 |
| 2F-TLH-L1 | 900 | 3,500 | 1 |
| 2F-FCL-L1 | 4,800 | 1,600 | 2 |
| 2F-FCL-L2 | 4,800 | 1,600 | 2 |
| 2F-HS2-L1 | 1,500 | 2,500 | 1 |
| 2F-WSH-L1 | 2,100 | 3,500 | 1 |
| 2F-WSH-L2 | 900 | 1,500 | 1 |
| 2F-SHW-L1 | 2,100 | 2,000 | 1 |
| 2F-SHW-L2 | 2,100 | 2,000 | 1 |
| 2F-COR3-L1 | 2,100 | 1,600 | 1 |
| 2F-TLT-L1 | 1,500 | 3,500 | 1 |
| 2F-MBR-L1 | 4,800 | 2,500 | 2 |
| 2F-MBR-L2 | 4,800 | 2,500 | 2 |

## 照明配置図（2階） S=1:100

2FL = 設計GL+4,700（TP+113.70）／天井高 CH=2,600／製品未確定・仮定値

| | | | | |
|---|---|---|---|---|
| 工事名称 | 河沿要（仮称）新築計画 | | | |
| 図面名称 | 照明配置図（2階） | | | 図番 E-05 |
| 縮尺 | A3 1:100 | 日付 2026-10-03 | 設計 設計検討（仮） | |
| 段階 | 基本計画 ／ 本図は建築基準法令に基づく計画段階の検討図であり、確認申請・構造計算・関係機関協議により確定する | | | |

# 照明器具表・照度計算・制御 ― 主照明は直付ライン LED、埋込ダウンライトは弱い補助灯、階段は足元灯（製品未確定・仮定値）

## (1) 器具表

| 種類 | 寸法・仕様（仮定値） | 台数・数量 | 備考 |
|---|---|---|---|
| ライン（主） | 幅50×高60、長さ 600〜2,400 を連結、乳白・直付、2200〜5000K、Ra90以上、1〜100%、DALI-2 DT8（製品未確定） | 62列・約228m・計46.7万lm | 出力区分 600〜3500 lm/m、効率 120 lm/W、全点灯 約3.9kW |
| ダウンライト（弱） | φ75〜100 グレアレス、最大250lm、2200〜3000K、Ra90 | 80台 | 夕方〜夜の補助灯（昼は消灯） |
| 足元灯 | 壁埋込 プレート70×120（出っ張り2以下）、約40lm、2200K、人感＋時刻、停電時自動点灯 | 18台（階段1・2 各9台） | 踏面から300、2段おき＋踊場 |

## (2) 照度計算（光束法 E = Φ×U×M/A、M=0.8、床面平均。JIS Z 9110 を参考にした仮定の目標値）

| 階 | 室 | ㎡ | 目標lx | U | 列数 | 器具長さ(mm) | lm/m | 計画lx | ダウン |
|---|---|---|---|---|---|---|---|---|---|
| 1F | リビング・ダイニング | 34.5 | 300 | 0.48 | 3 | 4,800＋4,800＋4,800 | 2,000 | 318 | 6 |
| 1F | キッチン | 25.3 | 300 | 0.44 | 3 | 3,600＋3,600＋2,600 | 3,000 | 300 | 2 |
| 1F | パントリー | 7.9 | 200 | 0.33 | 1 | 4,500 | 1,600 | 240 | 0 |
| 1F | 玄関土間 | 10.8 | 200 | 0.33 | 1 | 4,500 | 2,000 | 220 | 3 |
| 1F | ホール | 20.7 | 200 | 0.41 | 2 | 4,500＋4,500 | 1,600 | 230 | 3 |
| 1F | ジム | 51.6 | 500 | 0.49 | 3 | 7,500＋7,500＋7,500 | 3,000 | 509 | 8 |
| 1F | ホール・階段1 | 20.4 | 150 | 0.41 | 2 | 4,500＋2,700 | 1,600 | 186 | 3 |
| 1F | トイレ（手洗い付） | 3.9 | 200 | 0.33 | 1 | 900 | 3,500 | 214 | 1 |
| 1F | 機械室（西系統） | 8.6 | 200 | 0.33 | 1 | 1,800 | 3,500 | 195 | 2 |
| 1F | 機械室（東系統） | 8.8 | 200 | 0.33 | 1 | 1,800 | 3,500 | 190 | 2 |
| 1F | ランドリー・室内干し | 16.2 | 300 | 0.37 | 2 | 4,800＋4,800 | 2,000 | 354 | 3 |
| 1F | ファミリークローゼット | 11.4 | 200 | 0.35 | 2 | 2,400＋2,400 | 2,000 | 233 | 2 |
| 1F | 洗面・脱衣 | 8.3 | 300 | 0.33 | 2 | 2,100＋900 | 3,500 | 277 | 0 |
| 1F | 浴室 | 10.5 | 200 | 0.34 | 2 | 2,100＋2,100 | 2,000 | 217 | 1 |
| 1F | 廊下 | 7.8 | 100 | 0.33 | 1 | 2,100 | 1,600 | 114 | 2 |
| 1F | トイレ | 6.1 | 200 | 0.33 | 1 | 1,500 | 3,500 | 229 | 2 |
| 1F | 居室A | 17.3 | 200 | 0.40 | 2 | 3,300＋3,300 | 2,000 | 243 | 2 |
| 1F | WIC | 8.8 | 200 | 0.33 | 1 | 3,300 | 2,500 | 247 | 2 |
| 1F | 廊下 | 7.3 | 100 | 0.33 | 1 | 4,800 | 600 | 104 | 0 |

| 階 | 室 | ㎡ | 目標lx | U | 列数 | 器具長さ(mm) | lm/m | 計画lx | ダウン |
|---|---|---|---|---|---|---|---|---|---|
| 2F | 居室B | 12.5 | 200 | 0.35 | 4 | 3,600＋3,600＋3,600＋3,600 | 2,500 | 659 | 2 |
| 2F | 居室C | 11.9 | 200 | 0.34 | 4 | 3,600＋3,600＋3,600＋3,600 | 2,500 | 678 | 2 |
| 2F | 廊下 | 6.5 | 100 | 0.33 | 1 | 4,800 | 600 | 118 | 0 |
| 2F | 居室D | 17.1 | 200 | 0.40 | 4 | 3,600＋3,600＋3,600＋3,600 | 2,500 | 548 | 2 |
| 2F | WIC | 9.3 | 200 | 0.33 | 1 | 3,600 | 2,000 | 203 | 0 |
| 2F | 廊下 | 6.3 | 100 | 0.33 | 1 | 4,500 | 600 | 113 | 0 |
| 2F | シアター | 34.5 | 200 | 0.29 | 3 | 4,800＋4,800＋4,800 | 2,500 | 238 | 6 |
| 2F | 前室（音響ロック） | 10.9 | 100 | 0.33 | 1 | 4,800 | 1,000 | 117 | 3 |
| 2F | WIC（主寝室） | 22.3 | 200 | 0.42 | 2 | 4,800＋4,800 | 1,600 | 232 | 3 |
| 2F | 図書室 | 33.8 | 300 | 0.47 | 3 | 4,800＋4,800＋4,800 | 2,000 | 323 | 6 |
| 2F | ホール・階段1 | 20.4 | 150 | 0.41 | 2 | 4,500＋4,500 | 1,200 | 174 | 3 |
| 2F | トイレ（手洗い付） | 3.9 | 200 | 0.33 | 1 | 900 | 3,500 | 214 | 1 |
| 2F | ファミリークローゼット | 22.2 | 200 | 0.42 | 2 | 4,800＋4,800 | 1,600 | 233 | 3 |
| 2F | ホール・階段2 | 5.5 | 150 | 0.33 | 1 | 1,500 | 2,500 | 180 | 1 |
| 2F | 洗面・脱衣 | 8.3 | 300 | 0.33 | 2 | 2,100＋900 | 3,500 | 277 | 0 |
| 2F | シャワー | 10.5 | 200 | 0.34 | 2 | 2,100＋2,100 | 2,000 | 217 | 1 |
| 2F | 廊下 | 7.8 | 100 | 0.33 | 1 | 2,100 | 1,600 | 114 | 2 |
| 2F | トイレ | 6.1 | 200 | 0.33 | 1 | 1,500 | 3,500 | 229 | 2 |
| 2F | 主寝室 | 34.5 | 200 | 0.48 | 2 | 4,800＋4,800 | 2,500 | 265 | 3 |

## (3) チャネルと時刻ごとの配分（L=ライン、D=ダウンライト、F=足元灯）

| 時刻 | L（ライン・主） | D（ダウンライト・弱） | F（足元灯） |
|---|---|---|---|
| 00:00 | 消灯 | 2200K・10% | 2200K・30% |
| 05:30 | 消灯 | 2200K・10% | 2200K・30% |
| 07:00 | 4000K・75% | 消灯 | 消灯 |
| 12:00 | 4750K・100% | 消灯 | 消灯 |
| 17:00 | 3750K・85% | 2700K・50% | 消灯 |
| 19:00 | 2850K・55% | 2700K・70% | 消灯 |
| 21:00 | 2450K・25% | 2200K・55% | 消灯 |
| 23:00 | 消灯 | 2200K・20% | 2200K・30% |
| 室ごとの上書き | ジムは使用中 5000K・100%。シアターは上映で L・D を 0、F のみ。寝室は 21 時以降 L 消灯・D 20% 以下 | | 停電時は内蔵電池で自動点灯 |

## (4) DALI-2 系統・グループ（各階3系統・64台・16グループ。KNX-DALI ゲートウェイ経由で bot から操作）

| 系統 | グループ数 | 器具数 |
|---|---|---|
| 1F-1 | 16 | 63 |
| 1F-2 | 16 | 32 |
| 1F-3 | 6 | 26 |
| 2F-1 | 15 | 60 |
| 2F-2 | 16 | 39 |
| 2F-3 | 3 | 9 |
| 合計 | 72 | 229 |

## 六角形の連結照明の検討（試験済み・不採用）

製品: Nanoleaf Shapes Hexagons（確認日 2026-10-25、メーカー・国内販売店のページを確認）。実在し、連結・調色（1200〜6500K）・Matter 対応。

判定: 実在するが壁用・装飾用。天井へのテープ取付不可（落下は保証外）、1枚 100lm・Ra80 で LDK 300lx に 217〜270 枚、継ぎ目と段差が総延長約 150m 残り清掃性に反する。代わりに棒状 LED（遠藤照明 Linear series の調光調色品を第一候補、Zumtobel SLOTLIGHT infinity II を代替。型番・DALI 対応・防塵等級は要確認）を採用

試験: LDK の天井を 3 案（既存／六角形217枚／ライン3列）で描画し比較（docs/cg_lighting_hex_vs_line.jpg）。六角形は柔らかい光の面になるが、継ぎ目の格子と段差が天井に多数残る

## 足元灯・防災

足元灯は階段の手すり壁（LGS）の両面と踊場の間仕切に埋込み、各段の踏面から300・2段おき。火災報知で避難経路の L を 100%（4000K）。一戸建て住宅は非常用の照明の対象外（令126条の4）で、足元灯は自主的な安全対策

## 仮定・要確認

照明の設置容量は全点灯で約7.5W/㎡。運用平均は 2W/㎡ 相当と仮定（performance.py の前提は据え置き）。製品の型番・光束・DALI 対応・防塵等級・PSE は未確認（要施主確認）

| | | | | |
|---|---|---|---|---|
| 工事名称 | 河沿要（仮称）新築計画 | | | |
| 図面名称 | 照明器具表・照度計算・制御 | | | 図番 E-06 |
| 縮尺 | A3 ― | 日付 2026-10-03 | 設計 設計検討（仮） | |
| 段階 | 基本計画 ／ 本図は建築基準法令に基づく計画段階の検討図であり、確認申請・構造計算・関係機関協議により確定する | | | |