

河沿要（仮称）新築計画

基本計画図 / 2026-10-03 / 設計検討（仮）

計画概要

項目	内容
建設地	東京都八王子市大和田町7丁目
主要用途	一戸建ての住宅
用途地域	準工業地域（推定・要確認）
敷地面積	2,772.42 m ² （推定・要測量）
建築面積	297.56 m ² （建ぺい率 10.73%）
延べ面積	595.12 m ² （容積率 21.47%）
構造・階数	壁式鉄筋コンクリート造 地上2階
高さ	最高高さ 8.50m（設計GL基準）
階高・床高	1FL GL+1,500／階高 3,200×2
地盤	設計GL＝南側道路 TP+109.0／FGL GL+450（現況維持）
外構	RC塀 H2.0m（止水構造）・Dotcon+ 透水舗装・雨水貯留浸透
根拠資料	docs/kawazanyo_design_brief_v3.md、国土地理院 基盤地図情報・DEM5A


図面リスト

図番	図面名称	縮尺
A-00	表紙・図面リスト・計画概要	—
A-01	配置図・求積図	1:500
A-02	外構・雨水排水計画図	1:400
A-03	1階平面図	1:100
A-04	2階平面図	1:100
A-05	屋根伏図	1:100
A-06	立面図	1:200
A-07	断面図（建物）	1:100
A-08	敷地断面図（地形・浸水）	1:300
A-09	建具表	1:50・1:100
A-10	開口部仕様・排煙計画	—
A-11	法規チェックリスト（1/2）	—
A-12	法規チェックリスト（2/2）	—
S-01	基礎伏図・耐力壁配置図	1:100
S-02	RC塀・止水・透水舗装 詳細図	1:30

工事名称	河沿要（仮称）新築計画			
図面名称	表紙・図面リスト・計画概要			図番 A-00
縮尺	A3 ー	日付 2026-10-03	設計 設計検討（仮）	
段階	基本計画 / 本図は建築基準法令に基づく計画段階の検討図であり、確認申請・構造計算・関係機関協議により確定する			



水路（法定外公共物）／北側道路（幅員4m未満）TP+112.5～113.0

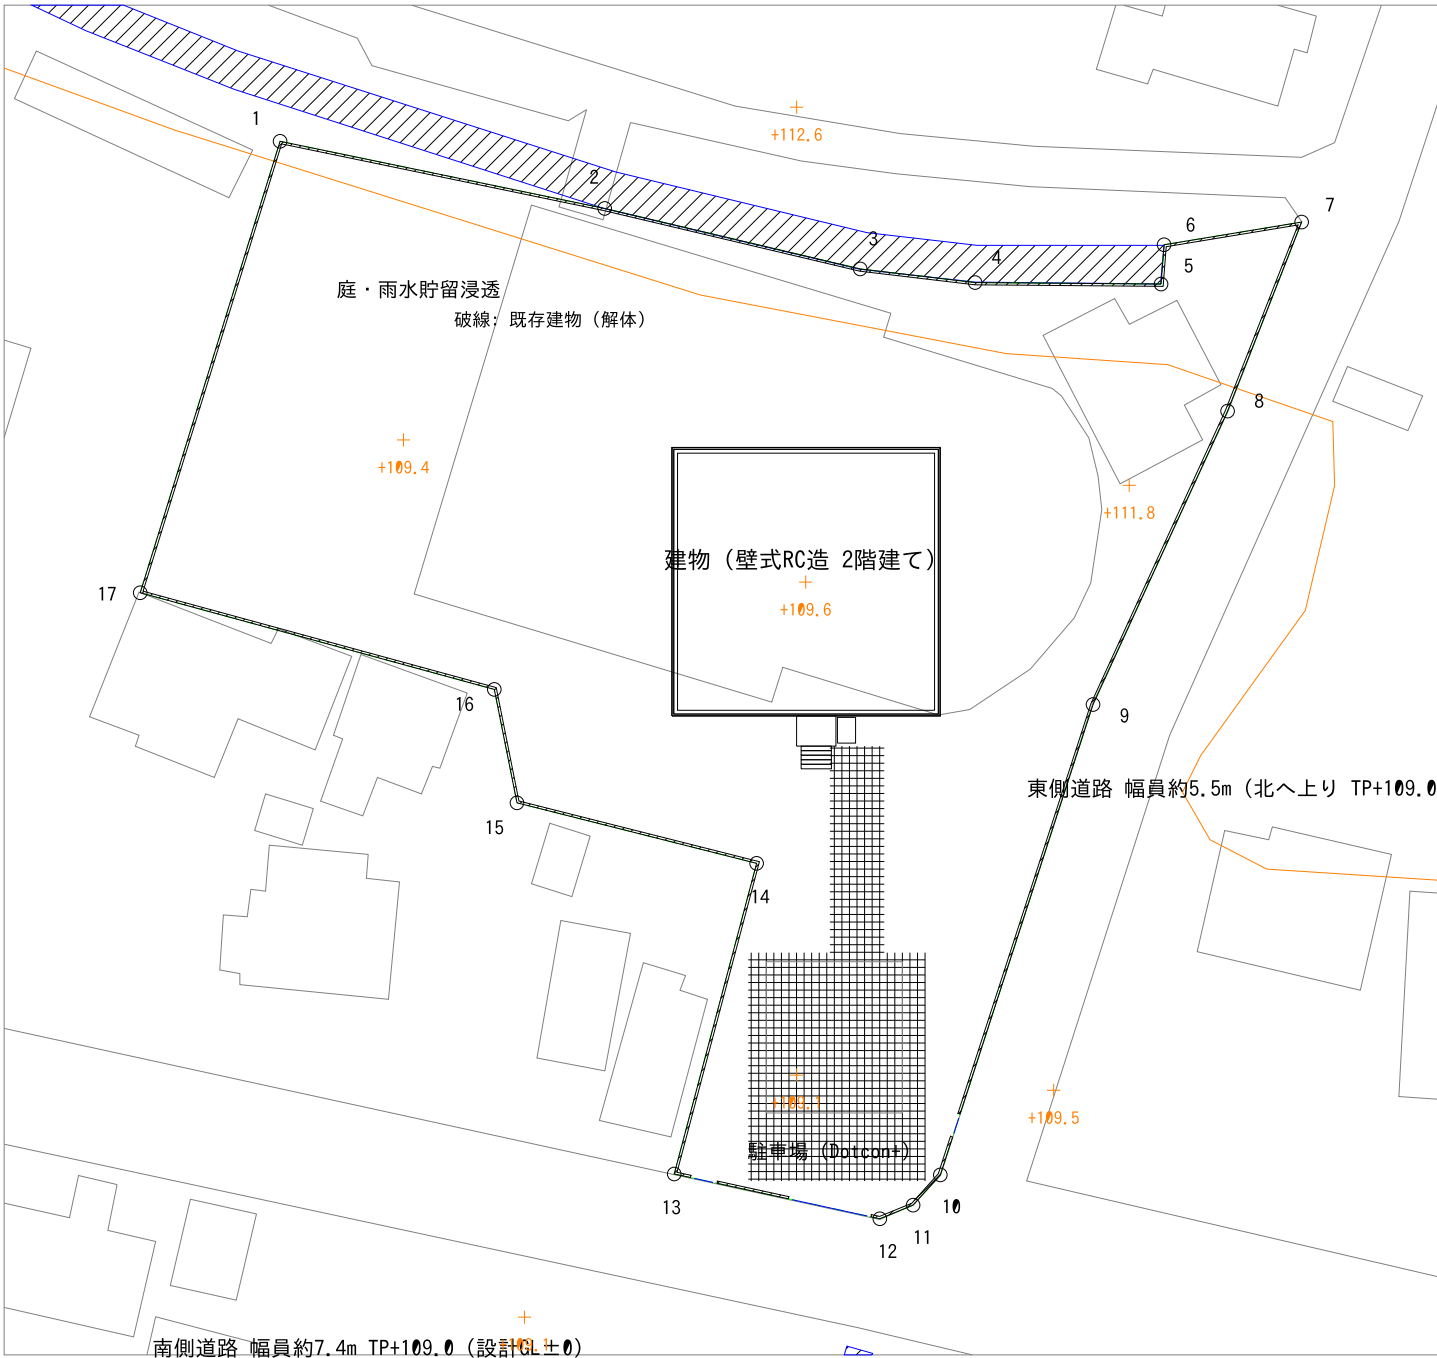

座標求積表（建物 X1・Y1 壁芯交点を原点、m）

点	X(m)	Y(m)	Xn(Yn+1-Yn-1)
1	-26.17	37.74	-664.85
2	-4.69	33.30	39.63
3	12.21	29.30	-59.80
4	19.80	28.41	-19.80
5	32.11	28.30	80.26
6	32.30	30.91	132.45
7	41.41	32.41	-455.46
8	36.51	19.90	-1164.51
9	27.61	0.50	-1394.05
10	17.50	-30.60	-579.42
11	15.70	-32.59	-45.54
12	13.50	-33.50	27.82
13	-0.09	-30.54	-2.23
14	5.35	-10.00	131.41
15	-10.50	-6.00	-120.69
16	-12.00	1.50	-166.61
17	-35.41	7.89	-1283.44
		倍面積	5544.84
		面積	2772.42 m ²


項目	面積・比率
敷地面積（推定）	2,772.42 m ² （838.7坪）
建築面積（壁芯）	297.56 m ²
延べ面積	595.12 m ²
建ぺい率	10.73%（≦60%）
容積率	21.47%（≦200%）

※ 西側境界は標高109.6の点を通り駐車場白線に平行な直線（ご指定）。13～15は隣接建物からの推定（要測量）。

配置図 S=1:500

敷地境界・道路縁・水路・隣接建物・等高線：国土地理院 基盤地図情報／標高：DEM5A（TP m）

工事名称	河沿要（仮称）新築計画		
図面名称	配置図・求積図		図番 A-01
縮尺	A3 1:500	日付 2026-10-03	設計 設計検討（仮）
段階	基本計画 ／ 本図は建築基準法令に基づく計画段階の検討図であり、確認申請・構造計算・関係機関協議により確定する		

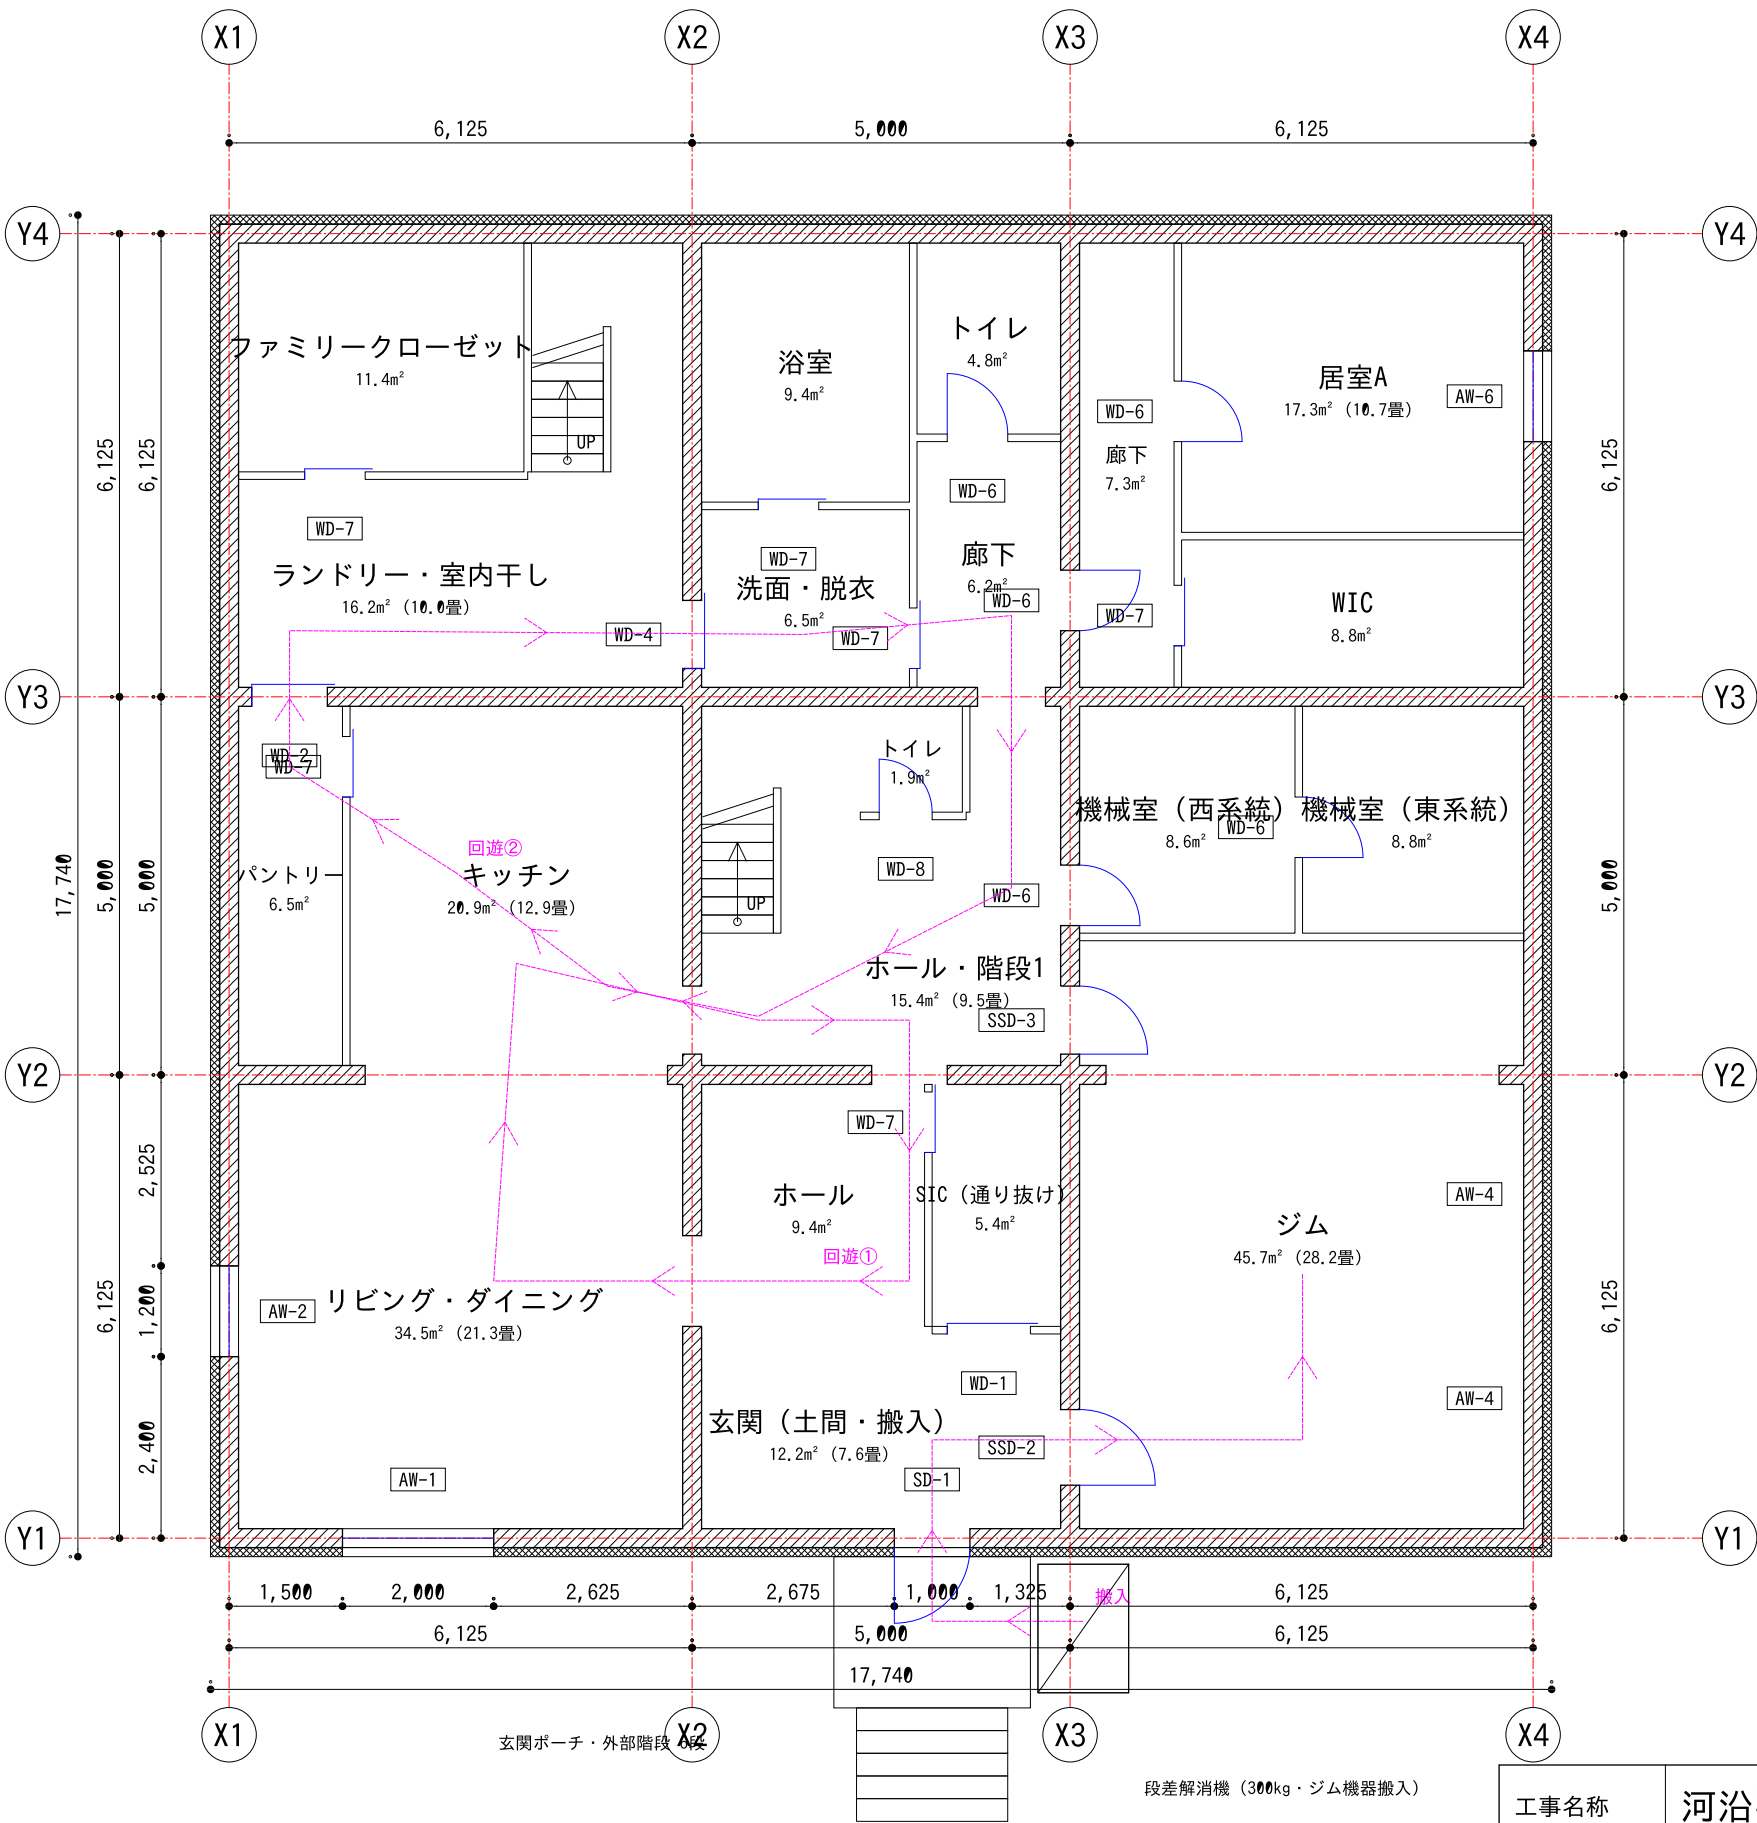

凡例

- RC壁 t=250 (耐力壁)
- 外断熱100+外装20
- 乾式間仕切 (LGS) t=100
- 通り芯 (壁芯)
- 動線 (回遊・家事・搬入)



計画の考え方 (v3.2)

回遊① (家族) : 玄関ホール→LDK→キッチン→ホール→玄関。行き止まりのない一周動線

回遊② (家事) : キッチン→パントリー→ランドリー→洗面脱衣→廊下→ホール→キッチン

洗う→干す→しまう: ランドリー・室内干し → 隣のファミリークローゼット／階段2で2階ファミクロへ直行

ジム 45.7m² (従前の1.32倍)。搬入は玄関から: 段差解消機 → 玄関 (W1,000×H2,300) → 土間 → 遮音ドア W1,000 → ジム (直進)。組立式パワーラック・一般ジム規模の機器を想定

ジムの窓: 外部扉を廃止し、窓は天井際の FIX 高窓 (窓台 FL+2,000、防犯合わせガラス・トリプル Low-E) に集約

防音: ジムは浮き床+遮音ドア Ts-35、機械室・WIC を緩衝帯として居室Aと分離。真上は2階シアター (騒音ゾーンを上下に集約)


排煙: LDK・ジム・居室Aは機械排煙 (令126条の3)。窓は FIX (トリプルガラス)。1階の窓は防犯合わせガラス (CP)

寸法: mm、面積: 壁芯内法の概算

1階平面図 S=1:100

1FL = 設計GL+1,500 (TP+110.50) /天井高 CH=2,600

工事名称	河沿要（仮称）新築計画			
図面名称	1階平面図			図番 A-03
縮尺	A3 1:100	日付 2026-10-03	設計 設計検討（仮）	
段階	基本計画 / 本図は建築基準法令に基づく計画段階の検討図であり、確認申請・構造計算・関係機関協議により確定する			

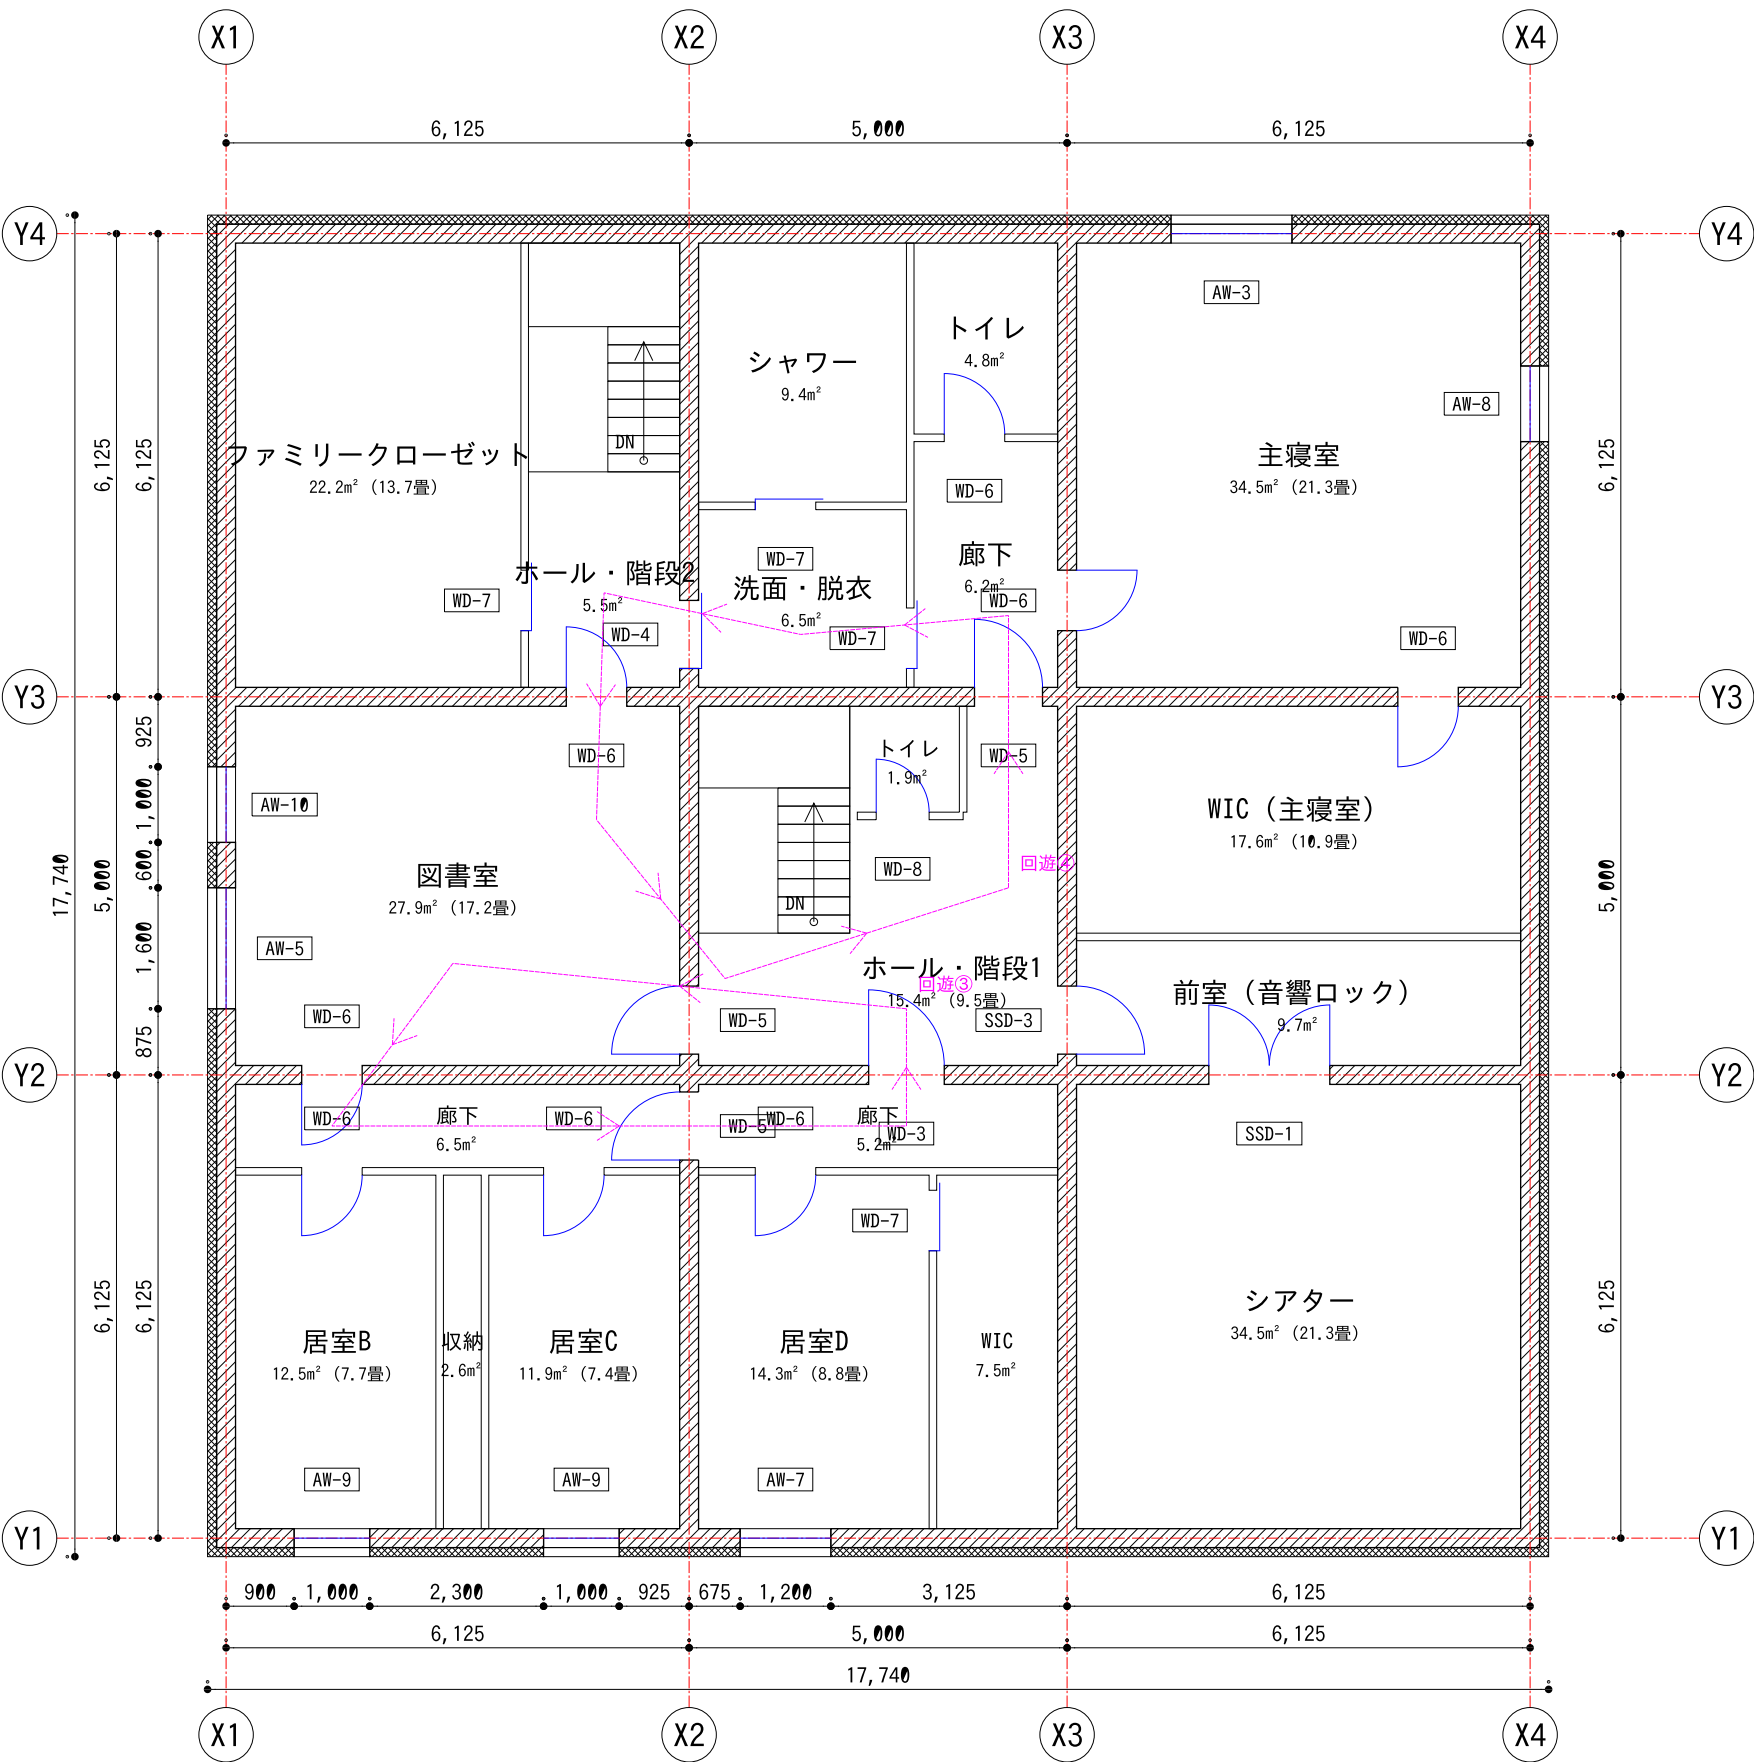

凡例

- RC壁 t=250 (耐力壁)
- 外断熱100+外装20
- 乾式間仕切 (LGS) t=100
- 通り芯 (壁芯)
- 動線 (回遊・家事・搬入)




計画の考え方 (v3.2)

回遊③: ホール→図書室→南廊下→ホール。回遊④: ホール→洗面→階段2ホール→図書室→ホール
窓: FIX (樹脂枠・Low-E トリプル・合わせガラス UVカット、 $U_w \leq 0.90$)。排煙は各居室の天井排煙口による機械排煙 (A-10 参照)
防音: シアターは前室 (音響ロック) + 両開き遮音扉 T_s-40 。主寝室とは前室・WIC の2層で分離
居室B・C・D は収納・WIC を間に挟んで隣室と分離 (戸境に収納)
ファミリークローゼット: 1階ランドリーから階段2で直結
寸法: mm、面積: 壁芯内法の概算

2階平面図 S=1:100

2FL = 設計GL+4,700 (TP+113.70) /天井高 CH=2,600


工事名称	河沿要 (仮称) 新築計画			
図面名称	2階平面図			図番 A-04
縮尺	A3 1:100	日付 2026-10-03	設計 設計検討 (仮)	
段階	基本計画 / 本図は建築基準法令に基づく計画段階の検討図であり、確認申請・構造計算・関係機関協議により確定する			

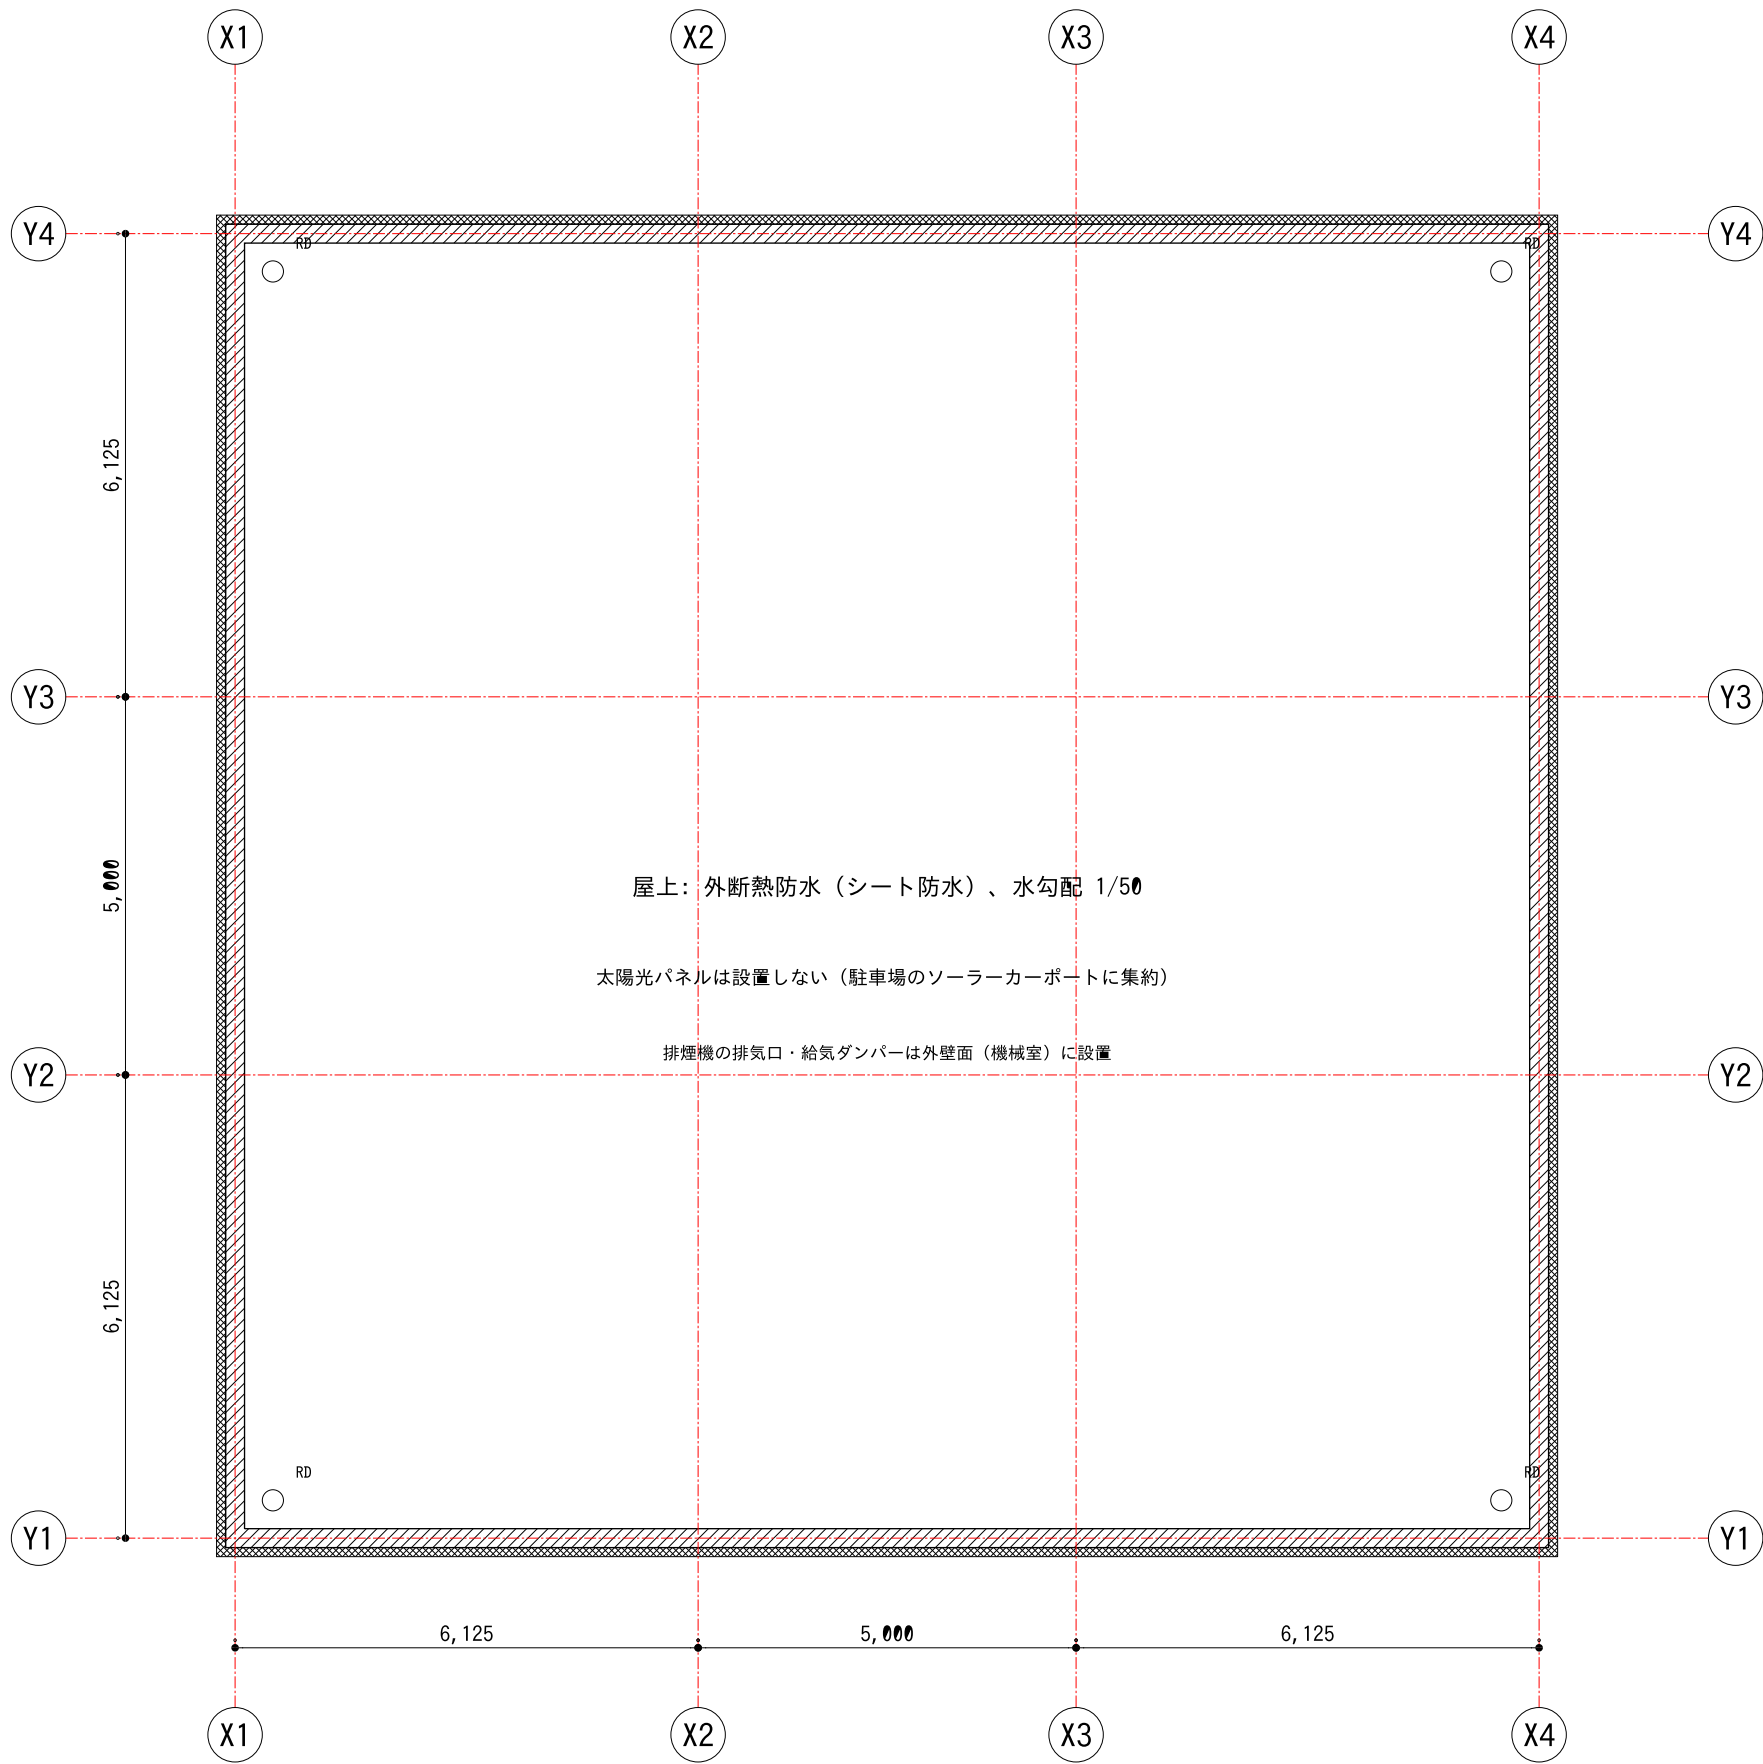


屋根伏図 S=1:100

RFL = 設計GL+7,900 / パラペット天端 GL+8,500


工事名称	河沿要（仮称）新築計画			
図面名称	屋根伏図			図番 A-05
縮尺	A3 1:100	日付 2026-10-03	設計 設計検討（仮）	
段階	基本計画 / 本図は建築基準法令に基づく計画段階の検討図であり、確認申請・構造計算・関係機関協議により確定する			

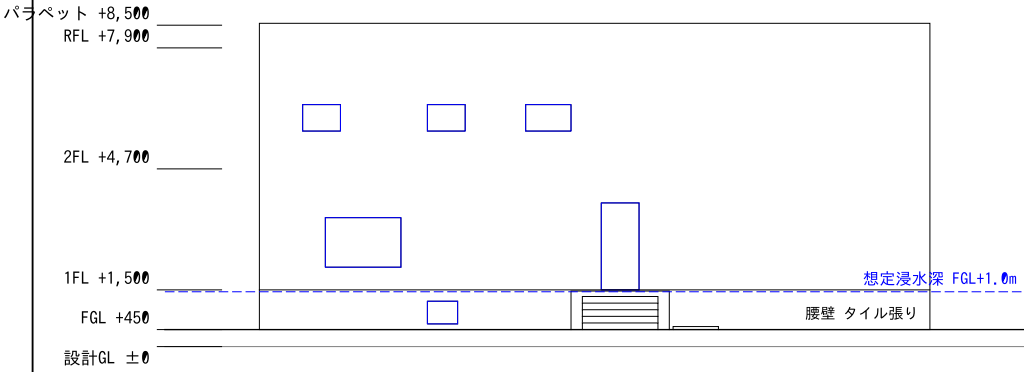


南立面図

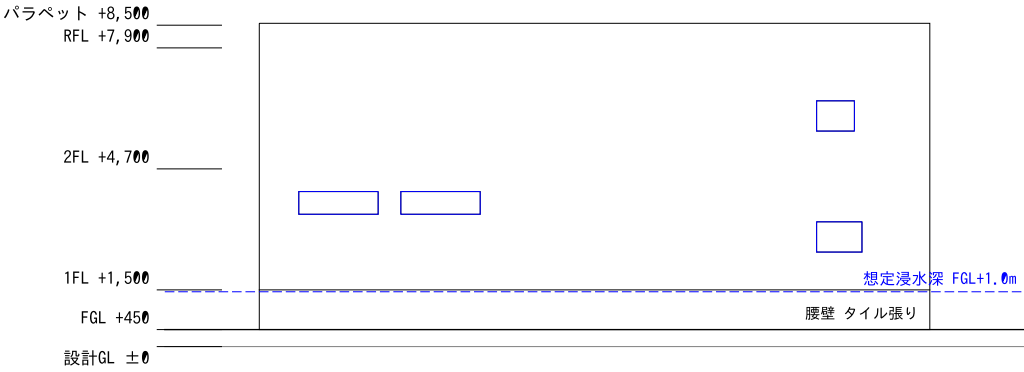

東立面図

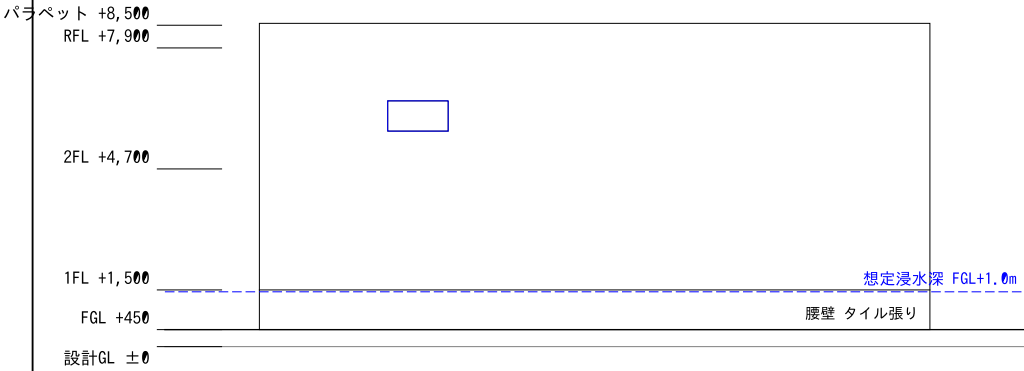

北立面図

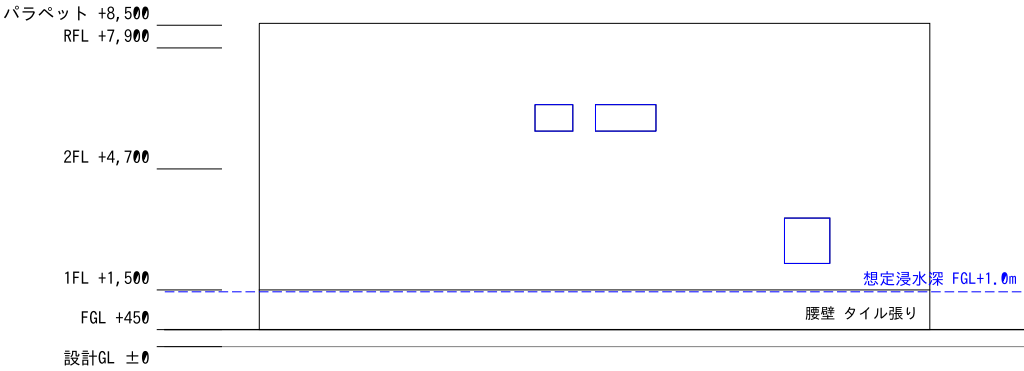


西立面図


外壁：外断熱100 + 外装仕上げ（腰壁 GL～+1,500 はタイル張り） 窓：FIX（トリプルガラス）

工事名称	河沿要（仮称）新築計画			
図面名称	立面図			図番 A-06
縮尺	A3 1:200	日付 2026-10-03	設計 設計検討（仮）	
段階	基本計画 / 本図は建築基準法令に基づく計画段階の検討図であり、確認申請・構造計算・関係機関協議により確定する			

断面図 A-A（X2-X3間、階段1を通る南北断面）

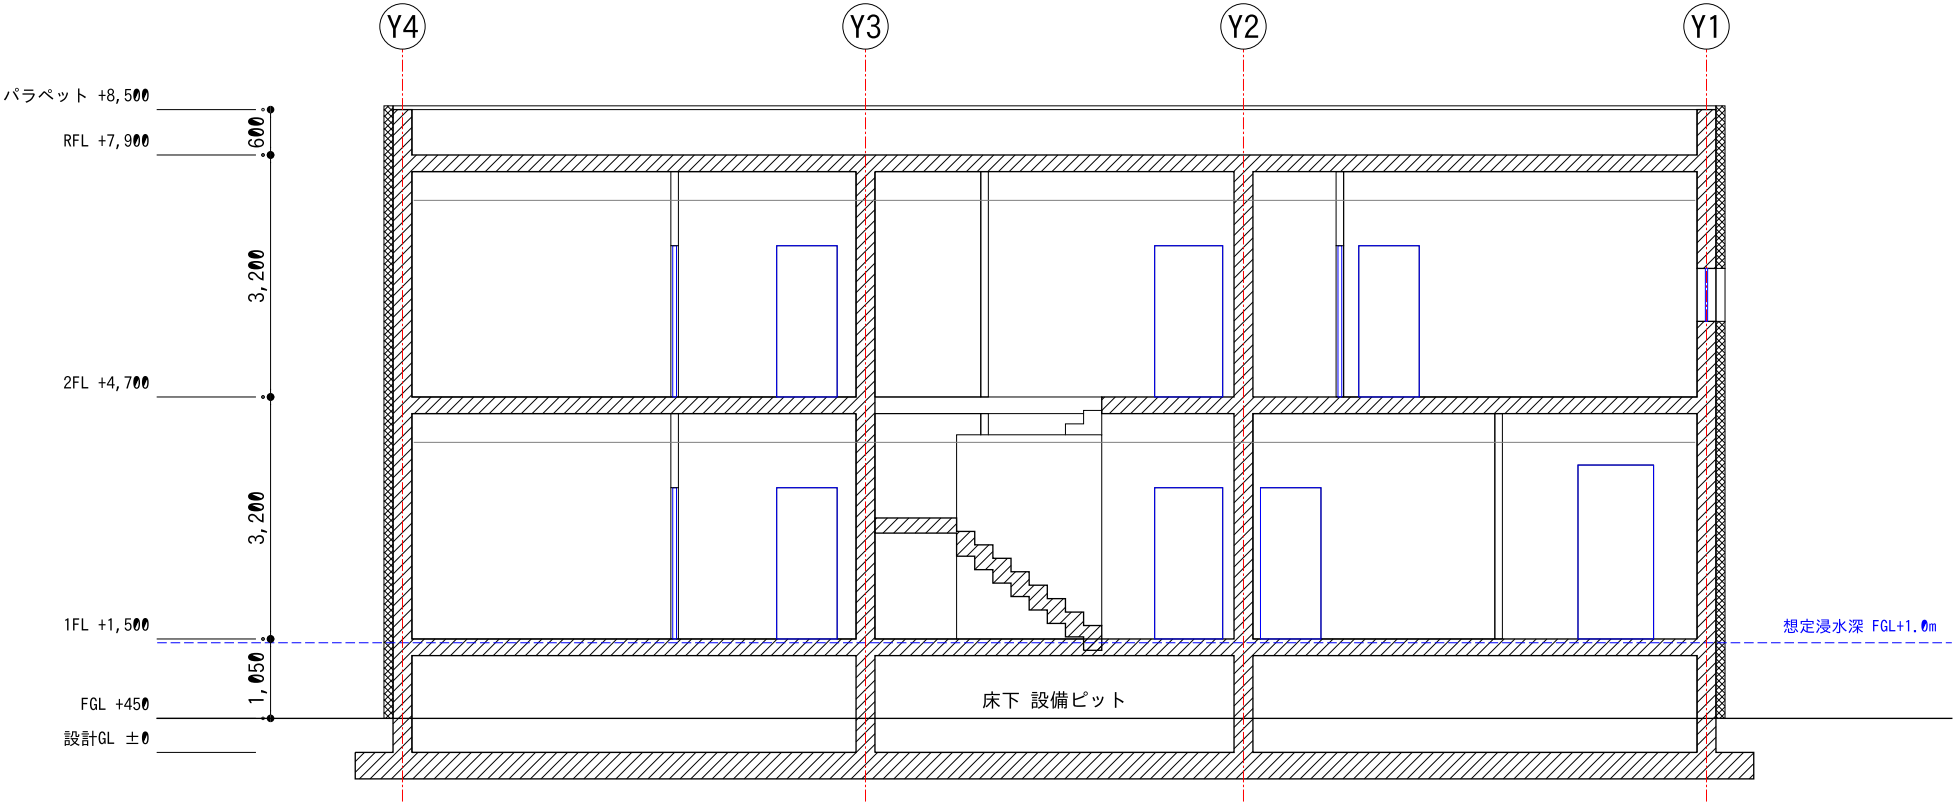

断面図 B-B（Y1-Y2間、LDK・玄関土間・ジム搬入扉を通る東西断面）

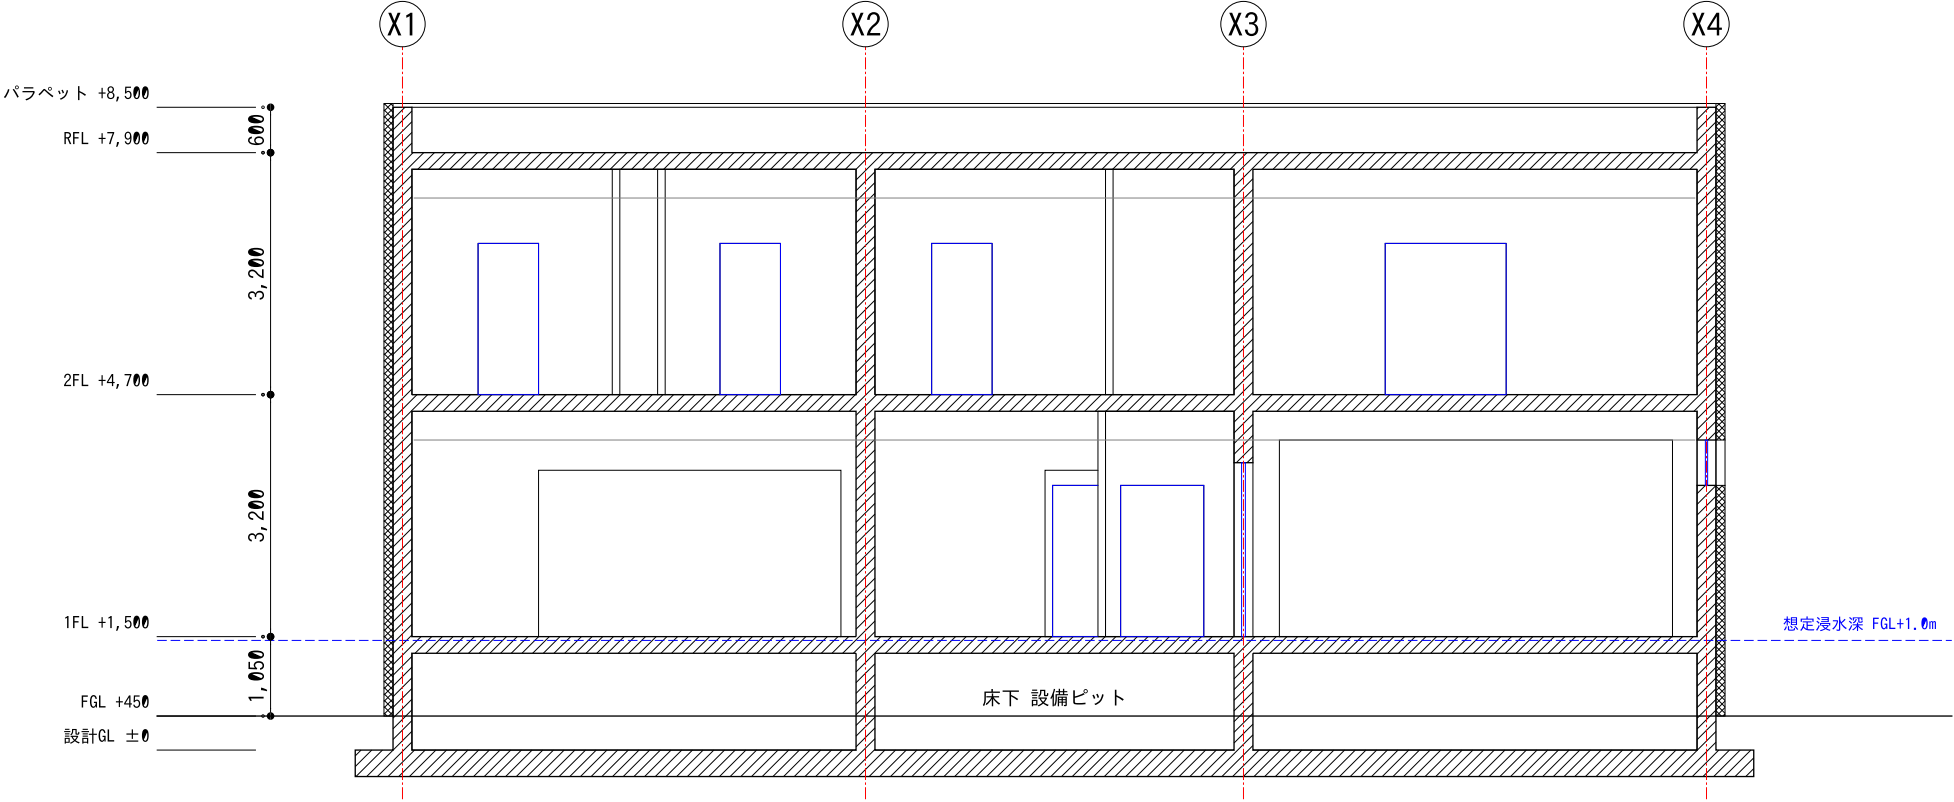

特記


階高 3,200×2／スラブ t=220／壁 RC t=250
天井高 CH=2,600（破線）。天井懐にダクト・浮き床
1FL=GL+1,500：想定浸水深(FGL+1.0m)より上
基礎：べた基礎 t=350＋地中梁（RC壁を基礎まで連続）
階段：蹴上 177.8 × 18段、踏面 240、有効幅 950（令23条 住宅）

工事名称	河沿要（仮称）新築計画			
図面名称	断面図（建物）			図番 A-07
縮尺	A3 1:100	日付 2026-10-03	設計 設計検討（仮）	
段階	基本計画 / 本図は建築基準法令に基づく計画段階の検討図であり、確認申請・構造計算・関係機関協議により確定する			


地形（DEM5A）

敷地 TP+109.3～109.6（ほぼ平坦）
北側道路 TP+112.5～113.0（敷地より約3.2m高い）
東側道路 TP+109.0→112.9（北へ上り）
→ 敷地は北・東からの表流水が集まる低い側。RC塀下部の止水と排水で対応
がけ（高さ2m超）からの離れ：北 約11.1m ≧ 2H=6.4m、東 約9.4m ≧ 2H=6.6m（東京都建築安全条例6条）

南北断面（建物中央 X2-X3間）（縦横同縮尺）

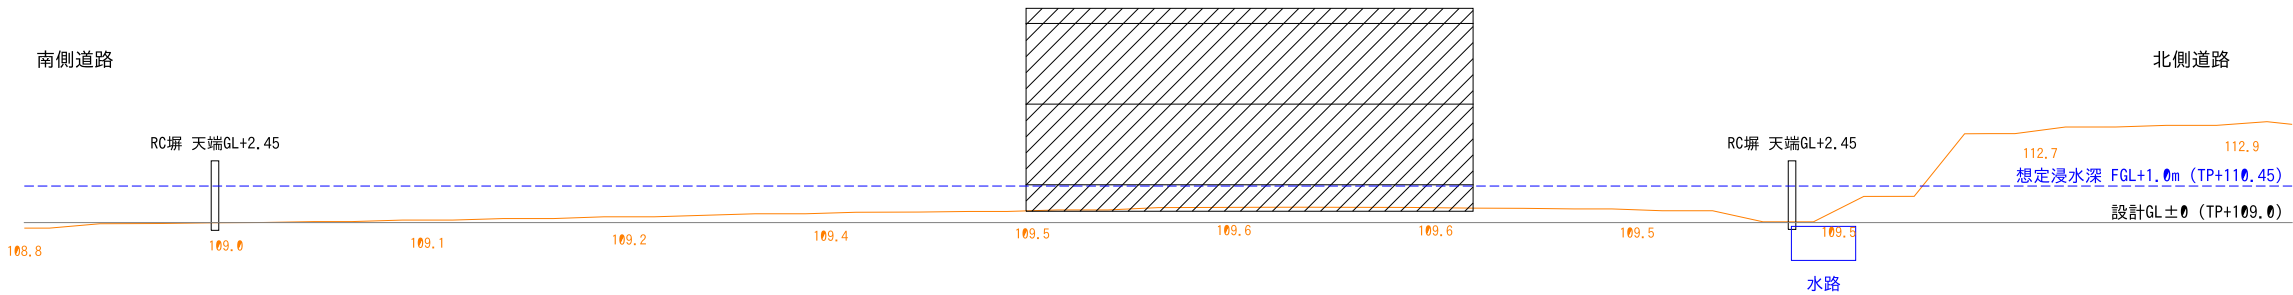

東西断面（建物中央 Y2-Y3間）（縦横同縮尺）

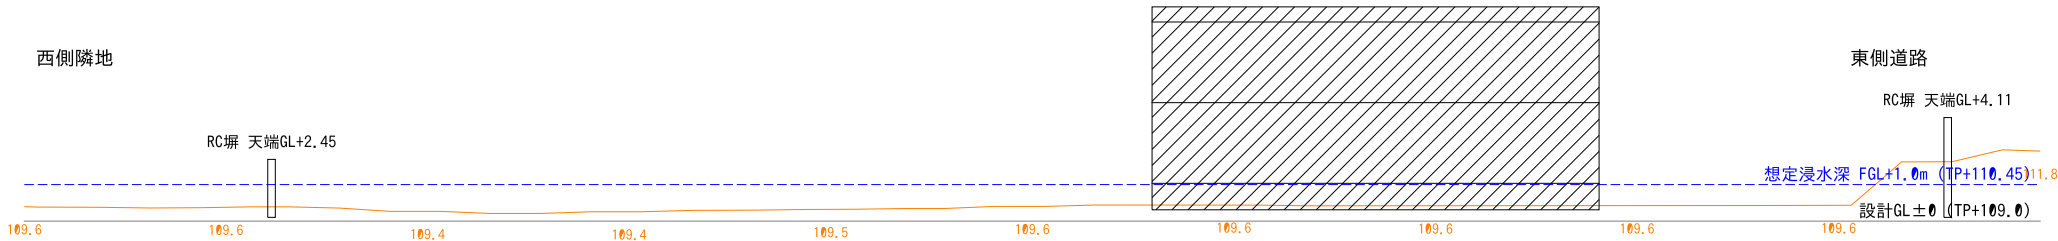

工事名称	河沿要（仮称）新築計画			
図面名称	敷地断面図（地形・浸水）			図番 A-08
縮尺	A3 1:300	日付 2026-10-03	設計 設計検討（仮）	
段階	基本計画 / 本図は建築基準法令に基づく計画段階の検討図であり、確認申請・構造計算・関係機関協議により確定する			

開口部仕様・排煙計画（2階の窓仕様と排煙方式の検討、ジム開口部の改善）

（1）居室の窓と採光（㎡）

階	居室	床面積	必要 15.29%	ガラス	有効(K3.0)	余裕
1F	LDK（キッチン含む）	55.4	8.47	4.06	12.18	1.44倍
1F	ジム	45.7	6.98	2.52	7.56	1.08倍
1F	居室A	17.3	2.65	0.96	2.88	1.09倍
2F	居室B	12.5	1.91	0.70	2.10	1.10倍
2F	居室C	11.9	1.82	0.70	2.10	1.15倍
2F	居室D	14.3	2.18	0.84	2.52	1.16倍
2F	図書室	27.9	4.27	1.82	5.46	1.28倍
2F	主寝室	34.5	5.28	2.08	6.24	1.18倍

（2）排煙計画（令126条の2・3）

階	防煙区画（居室）	面積	方式	系統	排煙口→最遠	参考:自然排煙の必要開放
1F	LDK（キッチン含む）	55.4	機械排煙	西系統	4.2m	1.11㎡
1F	ジム	45.7	機械排煙	東系統	4.9m	0.91㎡
1F	居室A	17.3	機械排煙	東系統	3.0m	0.35㎡
2F	居室B	12.5	機械排煙	西系統	2.7m	0.25㎡
2F	居室C	11.9	機械排煙	西系統	2.7m	0.24㎡
2F	居室D	14.3	機械排煙	西系統	2.8m	0.29㎡
2F	図書室	27.9	機械排煙	西系統	3.8m	0.56㎡
2F	主寝室	34.5	機械排煙	東系統	4.2m	0.69㎡

系統	区画数	最大区画	必要能力	計画
東系統	3	45.7㎡	120㎡ ³ /分	120㎡ ³ /分×1台
西系統	5	55.4㎡	120㎡ ³ /分	120㎡ ³ /分×1台

（3）2階の排煙方式の比較

比較項目	A 機械排煙（採用）	B 自然排煙（高窓の一部を開閉式）
窓	全室 FIX のまま	各室に内倒し窓（天井下80cm以内、床面積1/50以上）
防犯	開閉部なし（侵入経路にならない）	開閉部が増え、2階でも足場があれば弱点
気密・断熱	サッシ開閉部の隙間なし	開閉部の気密・熱貫流が劣る（Uw 約+0.2）
設備	排煙機・ダクト・予備電源（1階と共用）	手動開放装置のみ（設備は少ない）
維持管理	年1回の作動点検	開閉装置の点検・雨仕舞
判定	防犯・断熱・FIX方針と整合 → 採用	不採用

（4）ジム開口部の改善（防犯・熱貫流）

項目	改善前（v3.1）	改善後（v3.2）
窓	腰高窓 1.5×1.0m ×2（窓台 FL+1,000）	FIX 高窓 2.1×0.6m ×2（窓台 FL+2,000）
外部扉	南面 両開き搬入扉 1.8×2.4m	廃止（搬入は玄関から）
開口面積	7.32 ㎡	2.52 ㎡
開口まわり熱損失	9.2 W/K	3.3 W/K（64%減）
防犯	外部から手の届く窓・扉	窓下端 地盤+3.05m・防犯合わせガラス（CP、耐貫通5分以上）・開閉部なし
採光	9.00 ㎡（有効）	7.56 ㎡（必要 6.98）

窓の仕様（全窓 FIX）

枠：樹脂（またはアルミ樹脂複合）、ガラス：Low-E トリプル（アルゴン）＋合わせガラス（UVカット約99%）、Uw≦0.90 W/㎡K

1階：外側を防犯合わせガラス（CP 認定品）。2階：合わせガラス。窓台：居室 FL+1,000、ジム FL+2,000

換気は全館空調・全熱交換（窓に依存しない）。排煙時は機械室の給気ダンパーが連動して開く

排煙機：西・東系統の各機械室に 120㎡³/分×1台。排煙口は各居室の天井、手動開放装置は床から0.8～1.5m。予備電源は蓄電池（駐車場PV と連携、30分以上）

工事名称	河沿要（仮称）新築計画			
図面名称	開口部仕様・排煙計画			図番 A-10
縮尺	A3 ー	日付 2026-10-03	設計 設計検討（仮）	
段階	基本計画 ／ 本図は建築基準法令に基づく計画段階の検討図であり、確認申請・構造計算・関係機関協議により確定する			

法規チェックリスト（建築基準法・同施行令・関連法令／設計仕様書）

区分	項目	根拠条文	規定・要求	計画	判定
ブリーフ	敷地面積	ブリーフv3 1章	地図・航空写真・DEMによる推定	2,772.42㎡（推定誤差 ±5%程度）	要確認
ブリーフ	建物外寸・グリッド	ブリーフv3 5章	内寸17.0m角、6.0/5.0/6.0、RC250+外断熱120	壁芯 17.250m角、外寸 17.74m角	適合
ブリーフ	1階床高	ブリーフv3 3章	想定浸水深（FGL+1.0m）より上	1FL GL+1,500（FGL+1,050）	適合
ブリーフ	ジムの広さ	施主指示（v3.1）	従前 34.5㎡ の1.3倍	45.7㎡（1.32倍）	適合
ブリーフ	ジムの搬入	施主指示（v3.2）	窓からではなく玄関から搬入	組立式パワーラック・一般ジム規模の機器：車路→段差解消機→ポーチ→玄関 W1,000×H2,300→土間→遮音ドア W1,000×H2,300→ジム（直進・段差なし）	適合
ブリーフ	ジム開口部の防犯・断熱	施主指示（v3.2）	腰高窓・外部扉を弱点として改善	外部扉を廃止、窓は FIX 高窓（窓台FL+2,000）防犯合わせガラス。開口 7.3→2.5㎡、開口まわりの熱損失 9.2→3.3 W/K	適合
ブリーフ	太陽光発電	施主指示（v3.2）	住宅の屋根には設置しない（駐車場に設置）	ソーラーカーポートのみ（約90㎡）	適合
ブリーフ	駐車台数	ブリーフv3 2章	3台	3台（ソーラーカーポート下）	適合
ブリーフ	RC塀	ブリーフv3 4章	H2,000（防犯）	全周 H2.0m 以上（東側坂道沿いは道路面+1.2m以上）	適合
ブリーフ	透水性舗装	ブリーフv3 3.1	駐車場に Dotcon+	約226㎡（一時貯留 約2.9㎡）	適合
集団規定	用途地域の制限	法48条・別表第2	準工業地域（推定・要確認）：住宅は建築可	一戸建ての住宅	要確認
集団規定	接道	法43条	道路に2m以上接する	南側道路 約13.9m・東側道路 約81.8m	適合
集団規定	建ぺい率	法53条	60%以下（角地緩和は不使用）	297.56/2,772.42 = 10.73%	適合
集団規定	容積率	法52条	min(指定200%，道路7.4m×0.6=444%)	595.12/2,772.42 = 21.47%	適合
集団規定	道路斜線（南）	法56条1項1号・2項	勾配1.5、後退距離 30.3m による緩和	建物南面で許容 102.0m ≥ 高さ 8.50m	適合
集団規定	道路斜線（東）	法56条1項1号・2項	後退距離 9.4m（道路高さが敷地より高い区間は緩和あり）	許容 36.4m ≥ 8.50m	適合
集団規定	隣地斜線	法56条1項2号	31m+2.5×L	最高高さ 8.50m < 31m	適合
集団規定	北側斜線	法56条1項3号	低層・中高層住居専用地域等	準工業地域（推定）	対象外
集団規定	日影規制	法56条の2・都条例	準工業：高さ10m超が対象（指定時）	高さ 8.50m ≤ 10m	適合
集団規定	防火地域等	法61条	指定未確認（耐火建築物で計画）	壁式RC造（耐火構造）で計画	要確認
都条例	がけ（北側）	東京都建築安全条例6条	高さ2m超のがけ：下端から2H=6.4m 以上離す	水路（がけ下端）まで 11.1m	適合
都条例	がけ（東側）	東京都建築安全条例6条	道路との高低差 最大3.3m：2H=6.6m	東側道路境界まで 9.4m	適合
都条例	角敷地の隅切り	東京都建築安全条例2条	幅員がいずれも6m未満の道路の角敷地	南側道路 約7.4m（6m以上）	対象外
都条例	敷地と道路（大規模建築物）	東京都建築安全条例4条	延べ1,000㎡超は接道長さの割増し	延べ 595㎡	対象外
単体規定	採光 1F LDK（キッチン含む）	法28条1項・令19条・20条	床面積 55.4㎡ × 15.29% = 8.47㎡（法定 1/7 = 7.92）	ガラス 4.06㎡ × K3.0 = 12.18㎡	適合
単体規定	採光 1F ジム	法28条1項・令19条・20条	床面積 45.7㎡ × 15.29% = 6.98㎡（法定 1/7 = 6.53）	ガラス 2.52㎡ × K3.0 = 7.56㎡	適合
単体規定	採光 1F 居室A	法28条1項・令19条・20条	床面積 17.3㎡ × 15.29% = 2.65㎡（法定 1/7 = 2.47）	ガラス 0.96㎡ × K3.0 = 2.88㎡	適合
単体規定	採光 2F 居室B	法28条1項・令19条・20条	床面積 12.5㎡ × 15.29% = 1.91㎡（法定 1/7 = 1.79）	ガラス 0.70㎡ × K3.0 = 2.10㎡	適合
単体規定	採光 2F 居室C	法28条1項・令19条・20条	床面積 11.9㎡ × 15.29% = 1.82㎡（法定 1/7 = 1.70）	ガラス 0.70㎡ × K3.0 = 2.10㎡	適合
単体規定	採光 2F 居室D	法28条1項・令19条・20条	床面積 14.3㎡ × 15.29% = 2.18㎡（法定 1/7 = 2.04）	ガラス 0.84㎡ × K3.0 = 2.52㎡	適合
単体規定	採光 2F 図書室	法28条1項・令19条・20条	床面積 27.9㎡ × 15.29% = 4.27㎡（法定 1/7 = 3.99）	ガラス 1.82㎡ × K3.0 = 5.46㎡	適合
単体規定	採光 2F 主寝室	法28条1項・令19条・20条	床面積 34.5㎡ × 15.29% = 5.28㎡（法定 1/7 = 4.93）	ガラス 2.08㎡ × K3.0 = 6.24㎡	適合
単体規定	採光補正係数	令20条	準工業：K = 8d/h - 1（上限3.0）	隣地・道路まで十分な距離 → 3.0（要確認）	要確認
単体規定	換気	法28条2項・令20条の2	窓（1/20）または機械換気設備	全館空調・全熱交換換気（FIX窓に依存しない）	適合
単体規定	シックハウス（24時間換気）	法28条の2・令20条の8	0.5回/h 以上	全熱交換換気で常時換気	適合

判定：適合／要確認（条例・関係機関協議・別途計算による）／対象外。数値はすべて建物モデルから自動算定。

工事名称	河沿要（仮称）新築計画			
図面名称	法規チェックリスト（1/2）			図番 A-11
縮尺	A3 ー	日付 2026-10-03	設計 設計検討（仮）	
段階	基本計画 ／ 本図は建築基準法令に基づく計画段階の検討図であり、確認申請・構造計算・関係機関協議により確定する			

法規チェックリスト（建築基準法・同施行令・関連法令／設計仕様書）


区分	項目	根拠条文	規定・要求	計画	判定
単体規定	居室の天井高	令21条	2.1m以上	CH 2,600mm	適合
単体規定	階段（住宅）	令23条1項ただし書	幅750以上・蹴上230以下・踏面150以上	幅950・蹴上177.8・踏面240（2か所）	適合
単体規定	踊場・手すり	令24条・25条	高さ4m以内ごとに踊場、手すり設置	中間踊場（高さ 1.6m）・手すり設置	適合
単体規定	排煙（1階）	令126条の2・3	FIX窓の居室は「排煙上の無窓居室」→ 排煙設備	LDK・ジム・居室A：機械排煙（機械室の排煙機）	適合
単体規定	排煙（2階）	令126条の2・3	2階居室も FIX 窓 → 排煙上の無窓居室	居室B・C・D・図書室・主寝室：機械排煙（1階と同じ方式）	適合
単体規定	排煙機 能力（東系統）	令126条の3第1項9号	120m³/分以上かつ 最大区画 45.7m²×2 = 91m³/分以上（3区画）	排煙機 120m³/分（機械室）	適合
単体規定	排煙機 能力（西系統）	令126条の3第1項9号	120m³/分以上かつ 最大区画 55.4m²×2 = 111m³/分以上（5区画）	排煙機 120m³/分（機械室）	適合
単体規定	排煙口の位置	令126条の3第1項3号	防煙区画の各部分から水平距離30m以下・天井から80cm以内	各室の天井に排煙口、最遠 約4.9m	適合
単体規定	排煙の予備電源・手動開放	令126条の3第1項5号・11号	手動開放装置（床から0.8～1.5m）・予備電源	各室に手動開放装置、蓄電池（駐車場PV と連携）を予備電源に兼用	適合
単体規定	内装制限（火気使用室）	法35条の2・令128条の4第4項	2階建て住宅の1階で火気を使う室	IHクッキングヒーターなら対象外。ガス採用時は準不燃	要確認
単体規定	非常用の照明	令126条の4	一戸建ての住宅は除外	—	対象外
構造	壁量 1F X方向	平13国交告1026号 第5	12cm/m² 以上（地上2階建て）	耐力壁 53.4m / 床 297.6m² = 17.9cm/m²	適合
構造	壁量 1F Y方向	平13国交告1026号 第5	12cm/m² 以上（地上2階建て）	耐力壁 54.3m / 床 297.6m² = 18.3cm/m²	適合
構造	壁量 2F X方向	平13国交告1026号 第5	12cm/m² 以上（地上2階建て）	耐力壁 58.3m / 床 297.6m² = 19.6cm/m²	適合
構造	壁量 2F Y方向	平13国交告1026号 第5	12cm/m² 以上（地上2階建て）	耐力壁 59.5m / 床 297.6m² = 20.0cm/m²	適合
構造	耐力壁の厚さ	平13国交告1026号 第5	2階建て 15cm以上	25cm	適合
構造	耐力壁で囲まれた面積	平13国交告1026号 第5	60m² 以下	最大 37.5m²	適合
構造	階高・軒高・階数	平13国交告1026号 第1	階高3.5m以下・軒高20m以下・階数5以下	階高3.2m・軒高7.9m・2階	適合
構造	コンクリート強度	平13国交告1026号 第2・令74条	Fc18以上	Fc24	適合
構造	床版の厚さ	令77条の2・告示1026号	8cm以上かつ短辺/40	t=220（短辺 内法 5.88m /40 = 147）	適合
構造	かぶり厚さ	令79条	壁・床20（耐力壁30）／土に接する40／基礎60	設計かぶり 壁40・床30・土に接する50・基礎70	適合
構造	構造計算	法20条1項3号	壁式RC 2階建て（延べ200m²超）→ 構造計算（許容応力度等）	別途 構造計算書	要確認
構造	地盤・基礎	令38条	地盤調査に基づく基礎	べた基礎（杭の要否は調査後）	要確認
外構	RC塀	令62条の8（補強CB造）	RC塀は対象外 → 構造計算で同等以上の安全確認	H2.0m t=150 基礎1,200×400	要確認
外構	擁壁を兼ねる塀	法88条・令138条	高さ2m超の擁壁は工作物確認申請	東側坂道沿いで道路との段差を受ける区間が該当する可能性	要確認
外構	水路の占用・境界	法定外公共物管理条例（八王子市）	境界確定・占用協議	北側の塀・排水口の位置を協議	要確認
関連法令	建築物省エネ法	建築物省エネ法 10条（住宅の適合義務）	地域区分6：外皮 UA 0.87以下 ほか	UA 0.25～0.29（ブリーフ）	適合
関連法令	宅地造成・盛土等規制法	同法	規制区域内の切土・盛土	切土・盛土なし（現況地盤を維持）	適合
関連法令	雨水浸透	八王子市 雨水浸透施設の指導・助成	設置基準・補助の確認	貯留槽25m³・浸透トレンチ・浸透枳	要確認

判定：適合／要確認（条例・関係機関協議・別途計算による）／対象外。数値はすべて建物モデルから自動算定。

工事名称	河沿要（仮称）新築計画			
図面名称	法規チェックリスト（2/2）			図番 A-12
縮尺	A3 ー	日付 2026-10-03	設計 設計検討（仮）	
段階	基本計画 ／ 本図は建築基準法令に基づく計画段階の検討図であり、確認申請・構造計算・関係機関協議により確定する			

壁量・壁式構造の規定（平13国交告1026号）

階	方向	耐力壁長さ	壁量	判定
1F	X方向	53.4 m	17.9 cm/m ²	≧12 適合
1F	Y方向	54.3 m	18.3 cm/m ²	≧12 適合
2F	X方向	58.3 m	19.6 cm/m ²	≧12 適合
2F	Y方向	59.5 m	20.0 cm/m ²	≧12 適合
		壁厚	25 cm	≧15 適合

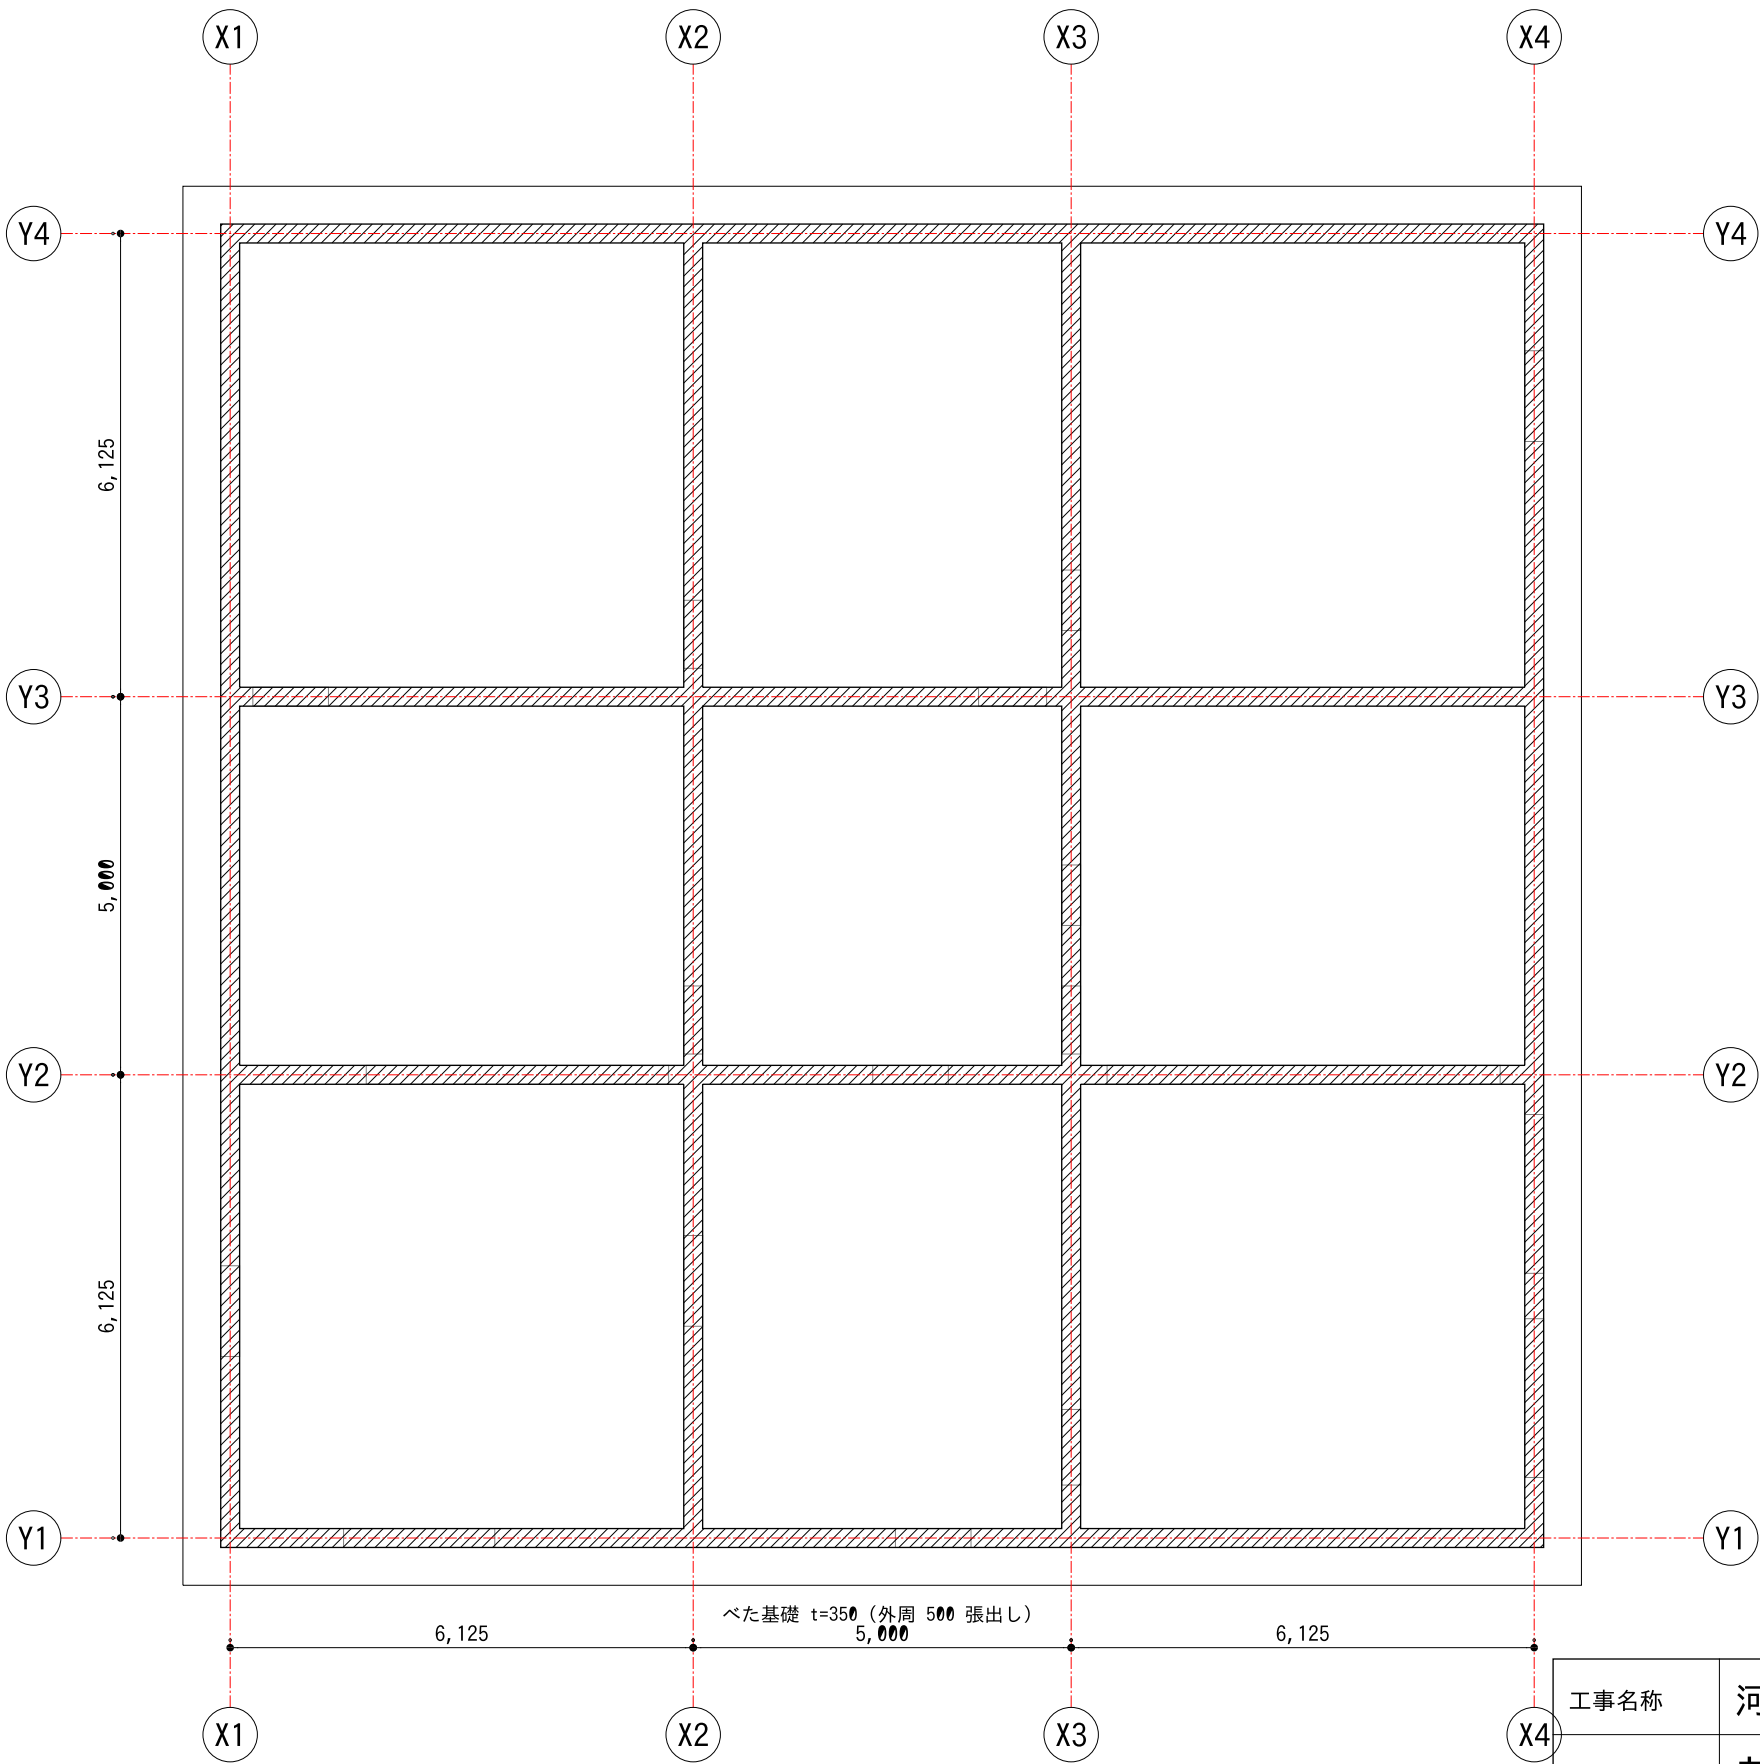

基礎伏図・耐力壁配置図（1階） S=1:100

網掛け=RC耐力壁 t=250（1・2階 同位置）、破線=開口


工事名称	河沿要（仮称）新築計画			
図面名称	基礎伏図・耐力壁配置図			図番 S-01
縮尺	A3 1:100	日付 2026-10-03	設計 設計検討（仮）	
段階	基本計画 / 本図は建築基準法令に基づく計画段階の検討図であり、確認申請・構造計算・関係機関協議により確定する			

車両門扉 W5,000・人用 W1,200・勝手口 W1,000。止水板は門扉の近くに保管



雨水浸透施設は、地盤調査（透水係数・地下水位）と八王子市の指導・助成制度を確認して決定

一時貯留 約13L/m²。車両荷重に応じた製品仕様を確認

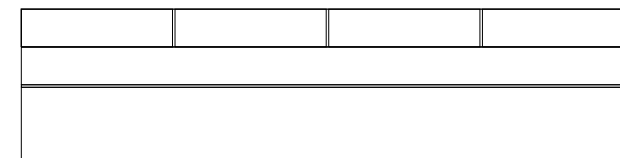

路床（現況土・透水試験で確認）

工事名称	河沿要（仮称）新築計画			
図面名称	RC塀・止水・透水舗装 詳細図			図番 S-02
縮尺	A3 1:30	日付 2026-10-03	設計 設計検討（仮）	
段階	基本計画 / 本図は建築基準法令に基づく計画段階の検討図であり、確認申請・構造計算・関係機関協議により確定する			