

河沿要（仮称）新築計画

基本計画図 / 2026-10-03 / 設計検討（仮）


計画概要

項目	内容
建設地	東京都八王子市大和田町7丁目
主要用途	一戸建ての住宅
用途地域	準工業地域（推定・要確認）
敷地面積	3,154.17 m ² （推定・要測量）
建築面積	297.56 m ² （建ぺい率 9.43%）
延べ面積	595.12 m ² （容積率 18.87%）
構造・階数	壁式鉄筋コンクリート造 地上2階
高さ	最高高さ 8.50m（設計GL基準）
階高・床高	1FL GL+1,500／階高 3,200×2
地盤	設計GL＝南側道路 TP+109.0／FGL GL+450（現況維持）
外構	RC塀 H2.0m（止水構造）・Dotcon+ 透水舗装・雨水貯留浸透
根拠資料	docs/kawazanyo_design_brief_v3.md、国土地理院 基盤地図情報・DEM5A

図面リスト

図番	図面名称	縮尺
A-00	表紙・図面リスト・計画概要	—
A-01	配置図・求積図	1:500
A-02	外構・雨水排水計画図	1:400
A-03	1階平面図	1:100
A-04	2階平面図	1:100
A-05	屋根伏図	1:100
A-06	立面図	1:200
A-07	断面図（建物）	1:100
A-08	敷地断面図（地形・浸水）	1:300
A-09	建具表	1:50・1:100
A-10	法規チェックリスト（1/2）	—
A-11	法規チェックリスト（2/2）	—
S-01	基礎伏図・耐力壁配置図	1:100
S-02	RC塀・止水・透水舗装 詳細図	1:30

工事名称	河沿要（仮称）新築計画			
図面名称	表紙・図面リスト・計画概要			図番 A-00
縮尺	A3 一	日付 2026-10-03	設計 設計検討（仮）	
段階	基本計画 / 本図は建築基準法令に基づく計画段階の検討図であり、確認申請・構造計算・関係機関協議により確定する			

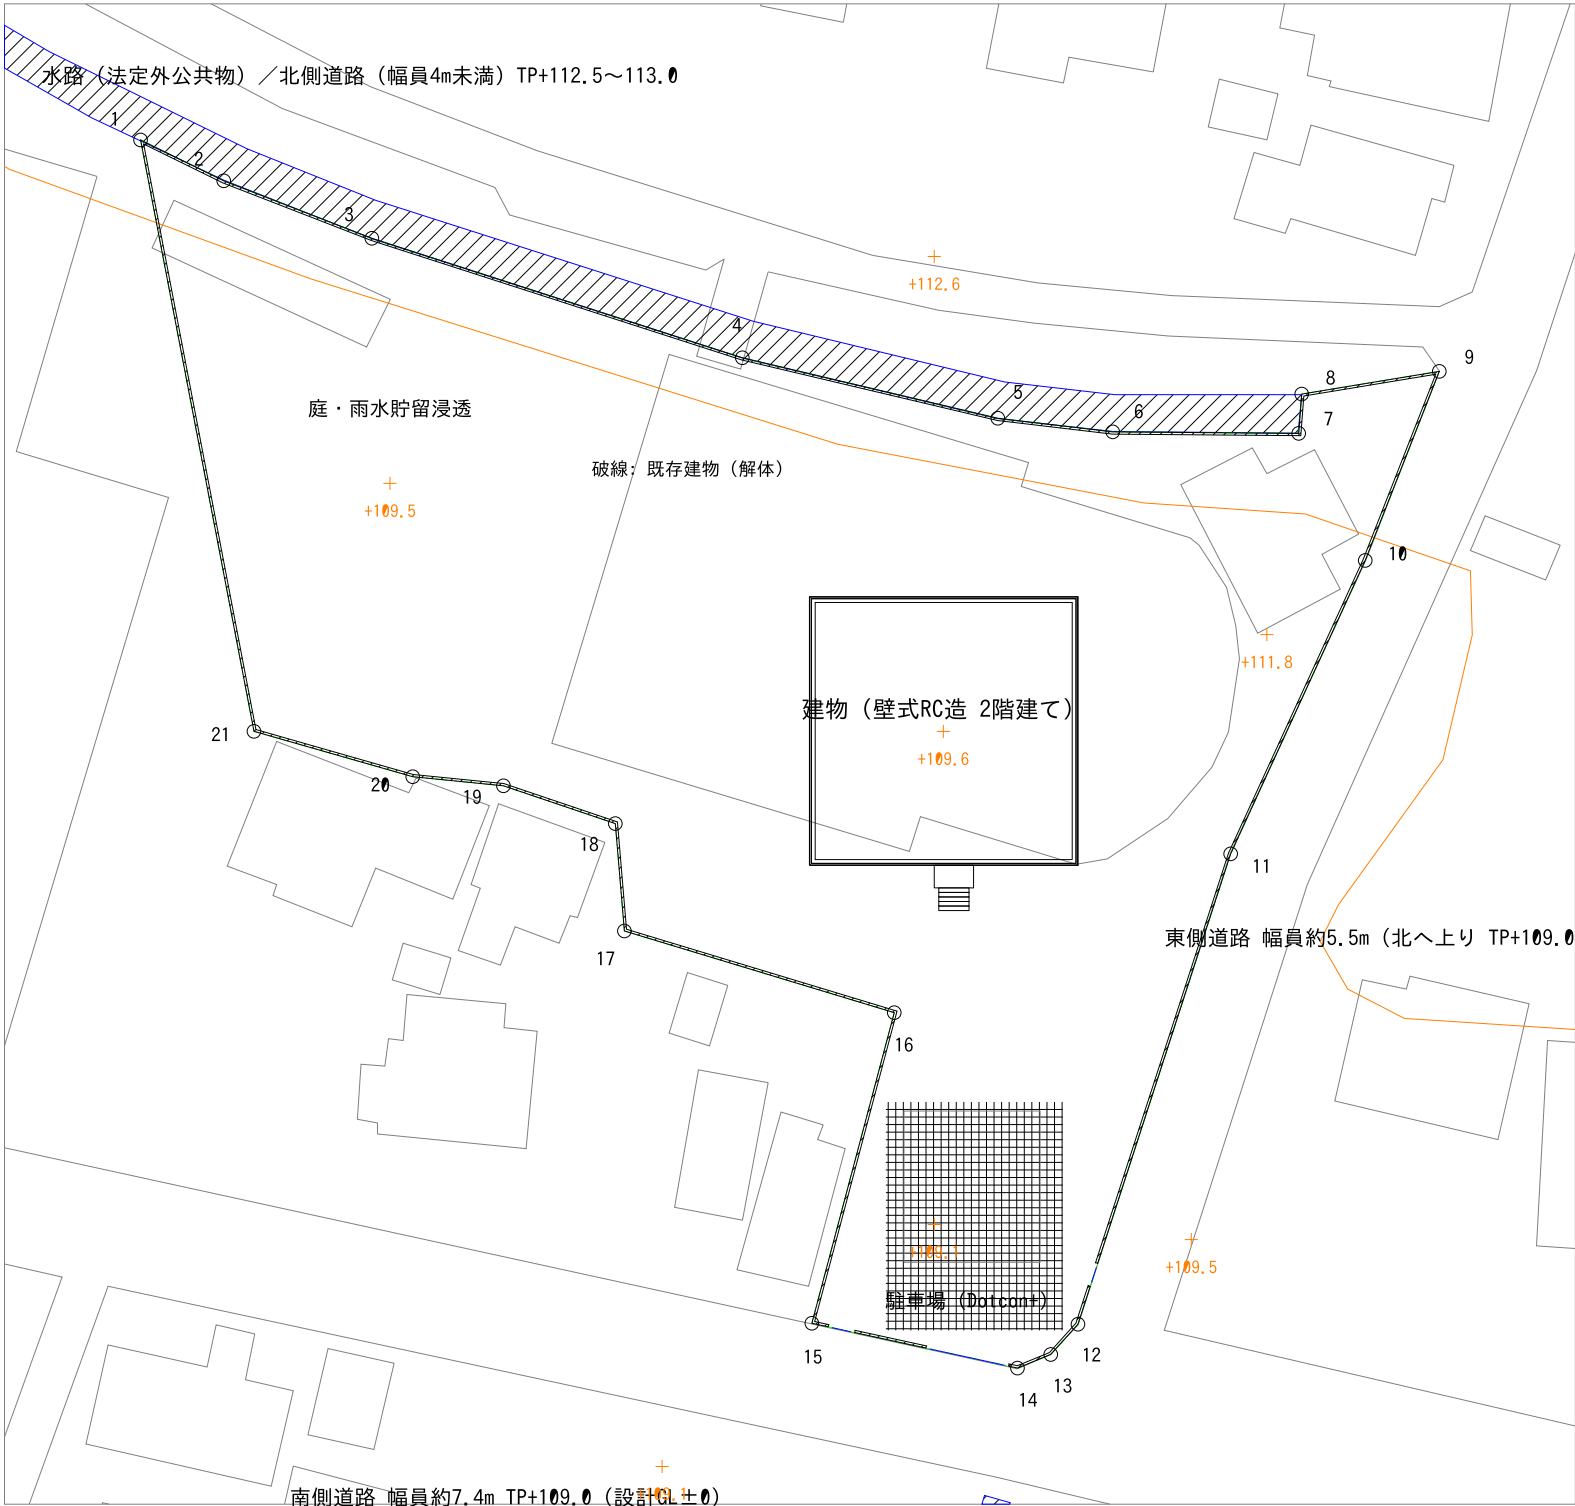

座標求積表 (建物 X1・Y1 壁芯交点を原点、m)

点	X(m)	Y(m)	Xn(Yn+1-Yn-1)
1	-44.49	47.70	-1619.62
2	-38.99	45.00	253.47
3	-29.20	41.20	341.58
4	-4.69	33.30	55.87
5	12.21	29.30	-59.80
6	19.80	28.41	-19.80
7	32.11	28.30	80.26
8	32.30	30.91	132.45
9	41.41	32.41	-455.46
10	36.51	19.90	-1164.51
11	27.61	0.50	-1394.05
12	17.50	-30.60	-579.42
13	15.70	-32.59	-45.54
14	13.50	-33.50	27.88
15	-0.09	-30.53	-2.23
16	5.35	-10.00	138.89
17	-12.50	-4.60	-156.19
18	-13.10	2.50	-125.71
19	-20.50	5.00	-63.53
20	-26.50	5.60	-95.38
21	-36.99	8.60	-1557.49
		倍面積	6308.35
		面積	3154.17 m ²


項目	面積・比率
敷地面積 (推定)	3,154.17 m ² (954.1坪)
建築面積 (壁芯)	297.56 m ²
延べ面積	595.12 m ²
建ぺい率	9.43% (≦60%)
容積率	18.87% (≦200%)

※ 境界の番号15～21は隣接建物からの推定（要測量）。誤差 ±5%程度。

配置図 S=1:500


敷地境界・道路縁・水路・隣接建物・等高線: 国土地理院 基盤地図情報／標高: DEM5A (TP m)

工事名称	河沿要 (仮称) 新築計画		
図面名称	配置図・求積図		図番 A-01
縮尺	A3 1:500	日付 2026-10-03	設計 設計検討 (仮)
段階	基本計画 / 本図は建築基準法令に基づく計画段階の検討図であり、確認申請・構造計算・関係機関協議により確定する		

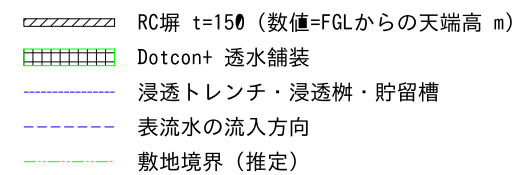

工事名称	河沿要（仮称）新築計画		
図面名称	外構・雨水排水計画図		図番 A-02
縮尺	A3 1:400	日付 2026-10-03	設計 設計検討（仮）
段階	基本計画 ／ 本図は建築基準法令に基づく計画段階の検討図であり、確認申請・構造計算・関係機関協議により確定する		

外構・雨水排水計画図 S=1:400

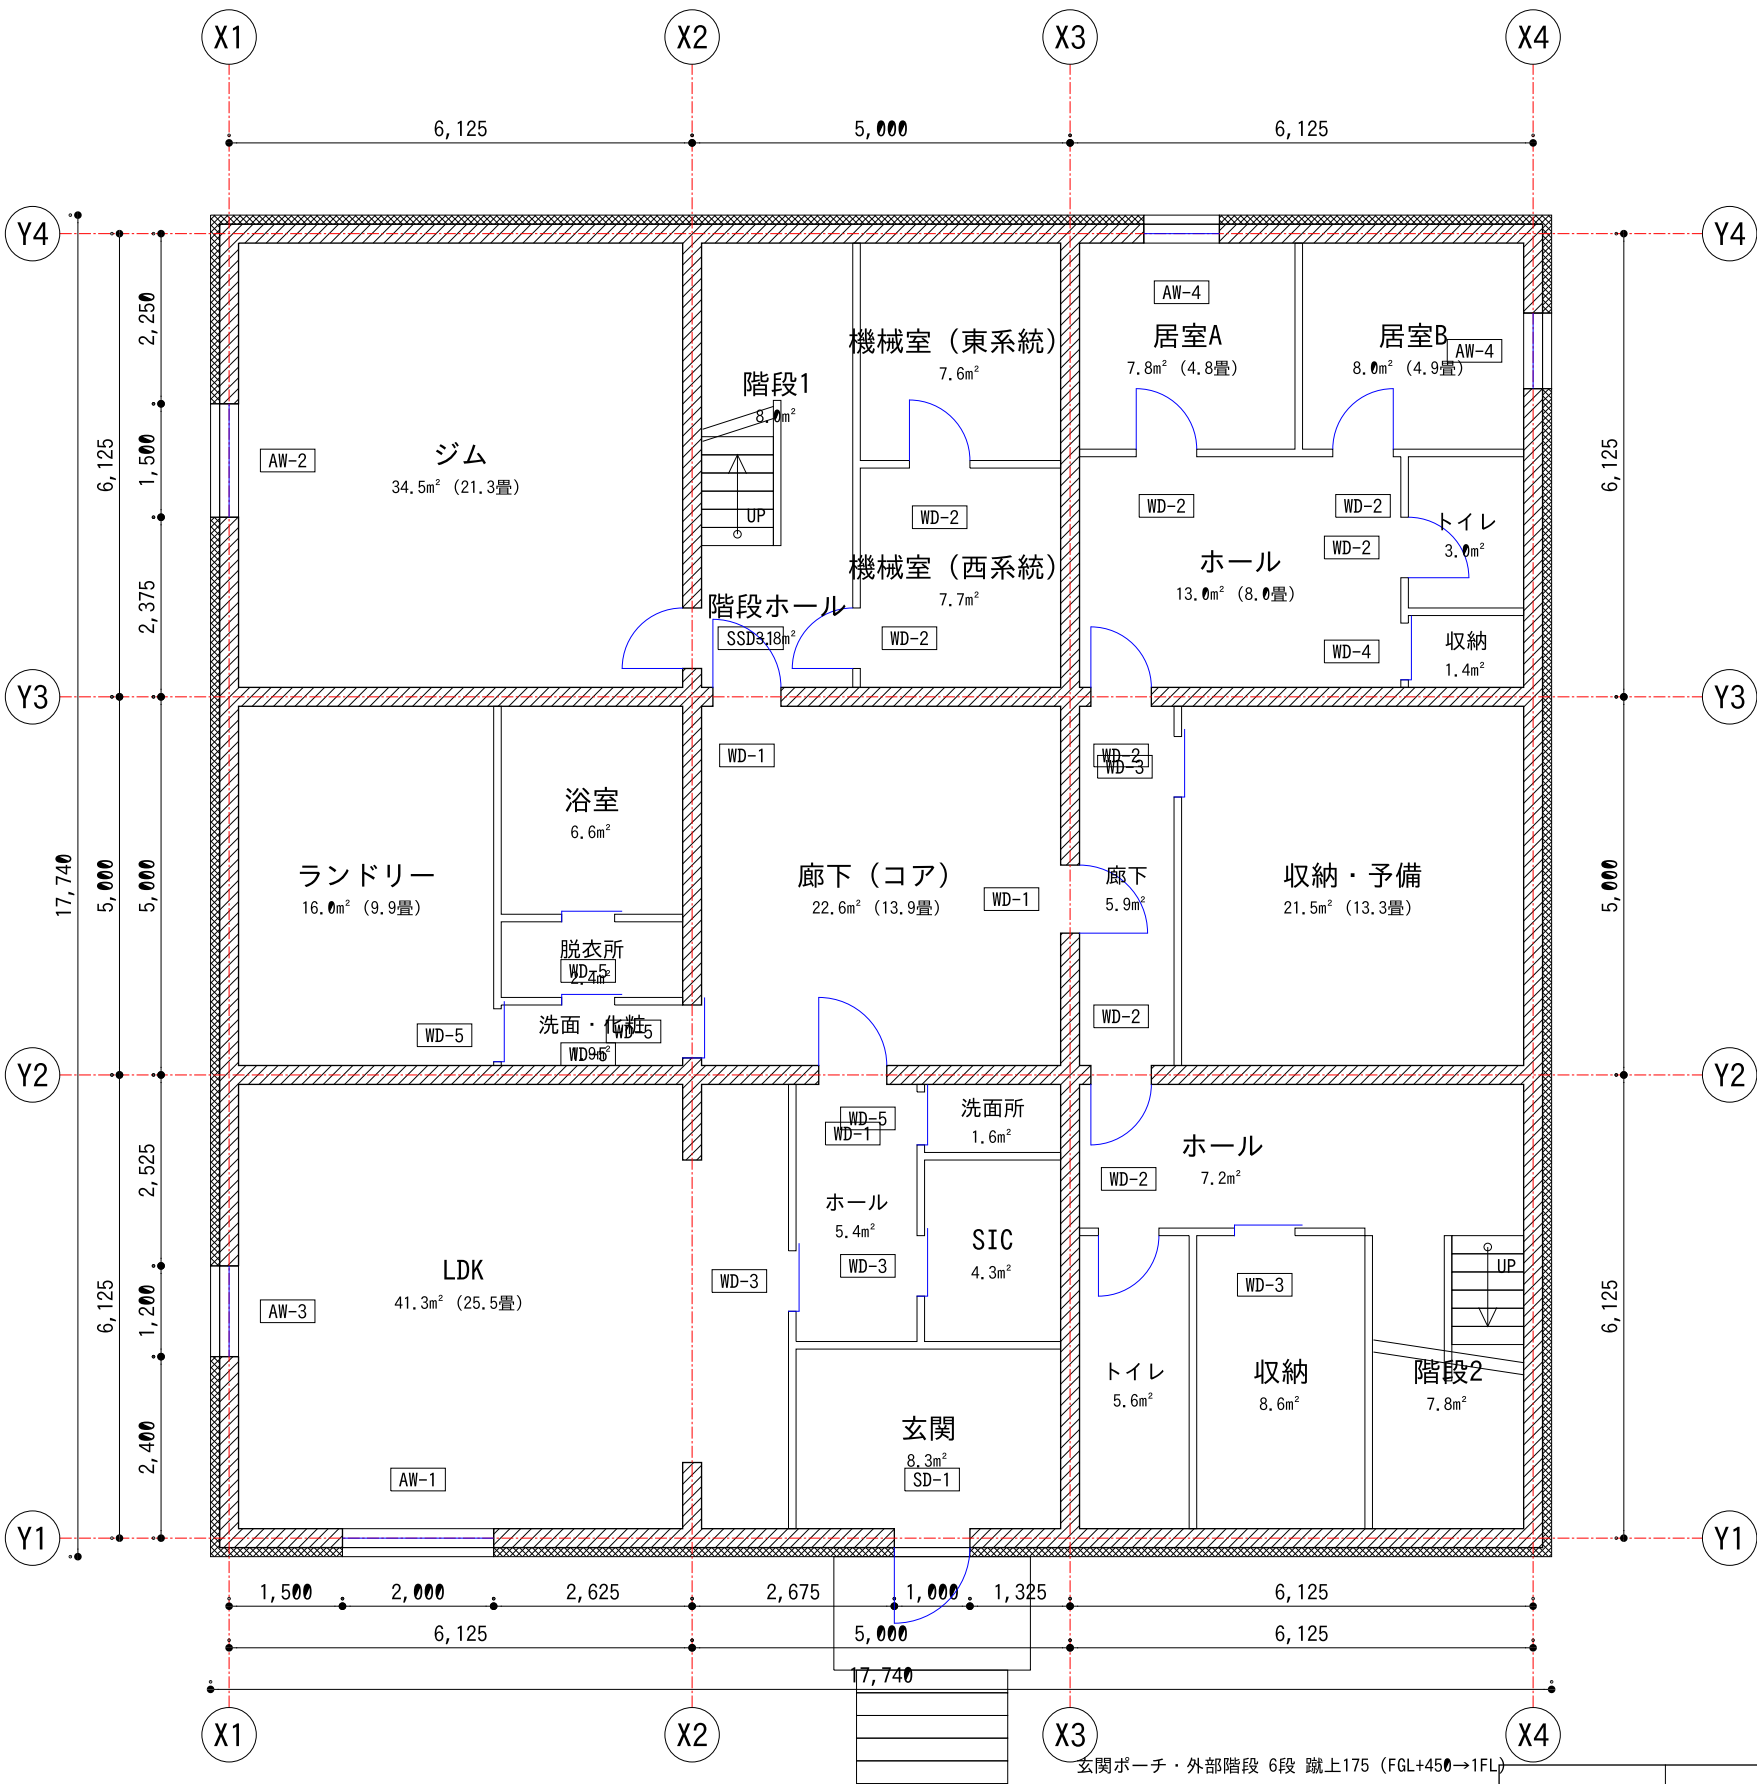

凡例

- RC壁 t=250 (耐力壁)
- 外断熱100+外装20
- 乾式間仕切 (LGS) t=100
- 通り芯 (壁芯)




特記

耐力壁: 外周+X2・X3・Y2・Y3通り (2階と同じ位置)
窓: FIX (トリプルガラス・樹脂枠・UVカット)。採光=ガラス面積×補正係数3.0
排煙: LDK・居室A・居室B・ジムは機械排煙 (令126条の3)
ジム: 浮き床 (防振)、遮音ドア Ts-35
床下: 設備ビット (高基礎)。床下点検口は防水扉
機械室: 西系統・東系統 (全熱交換・調湿・排煙機)
寸法: mm、面積: 壁芯内法の概算

1階平面図 S=1:100

1FL = 設計GL+1,500 (TP+110.50) /天井高 CH=2,600

工事名称	河沿要 (仮称) 新築計画			
図面名称	1階平面図			図番 A-03
縮尺	A3 1:100	日付 2026-10-03	設計 設計検討 (仮)	
段階	基本計画 / 本図は建築基準法令に基づく計画段階の検討図であり、確認申請・構造計算・関係機関協議により確定する			

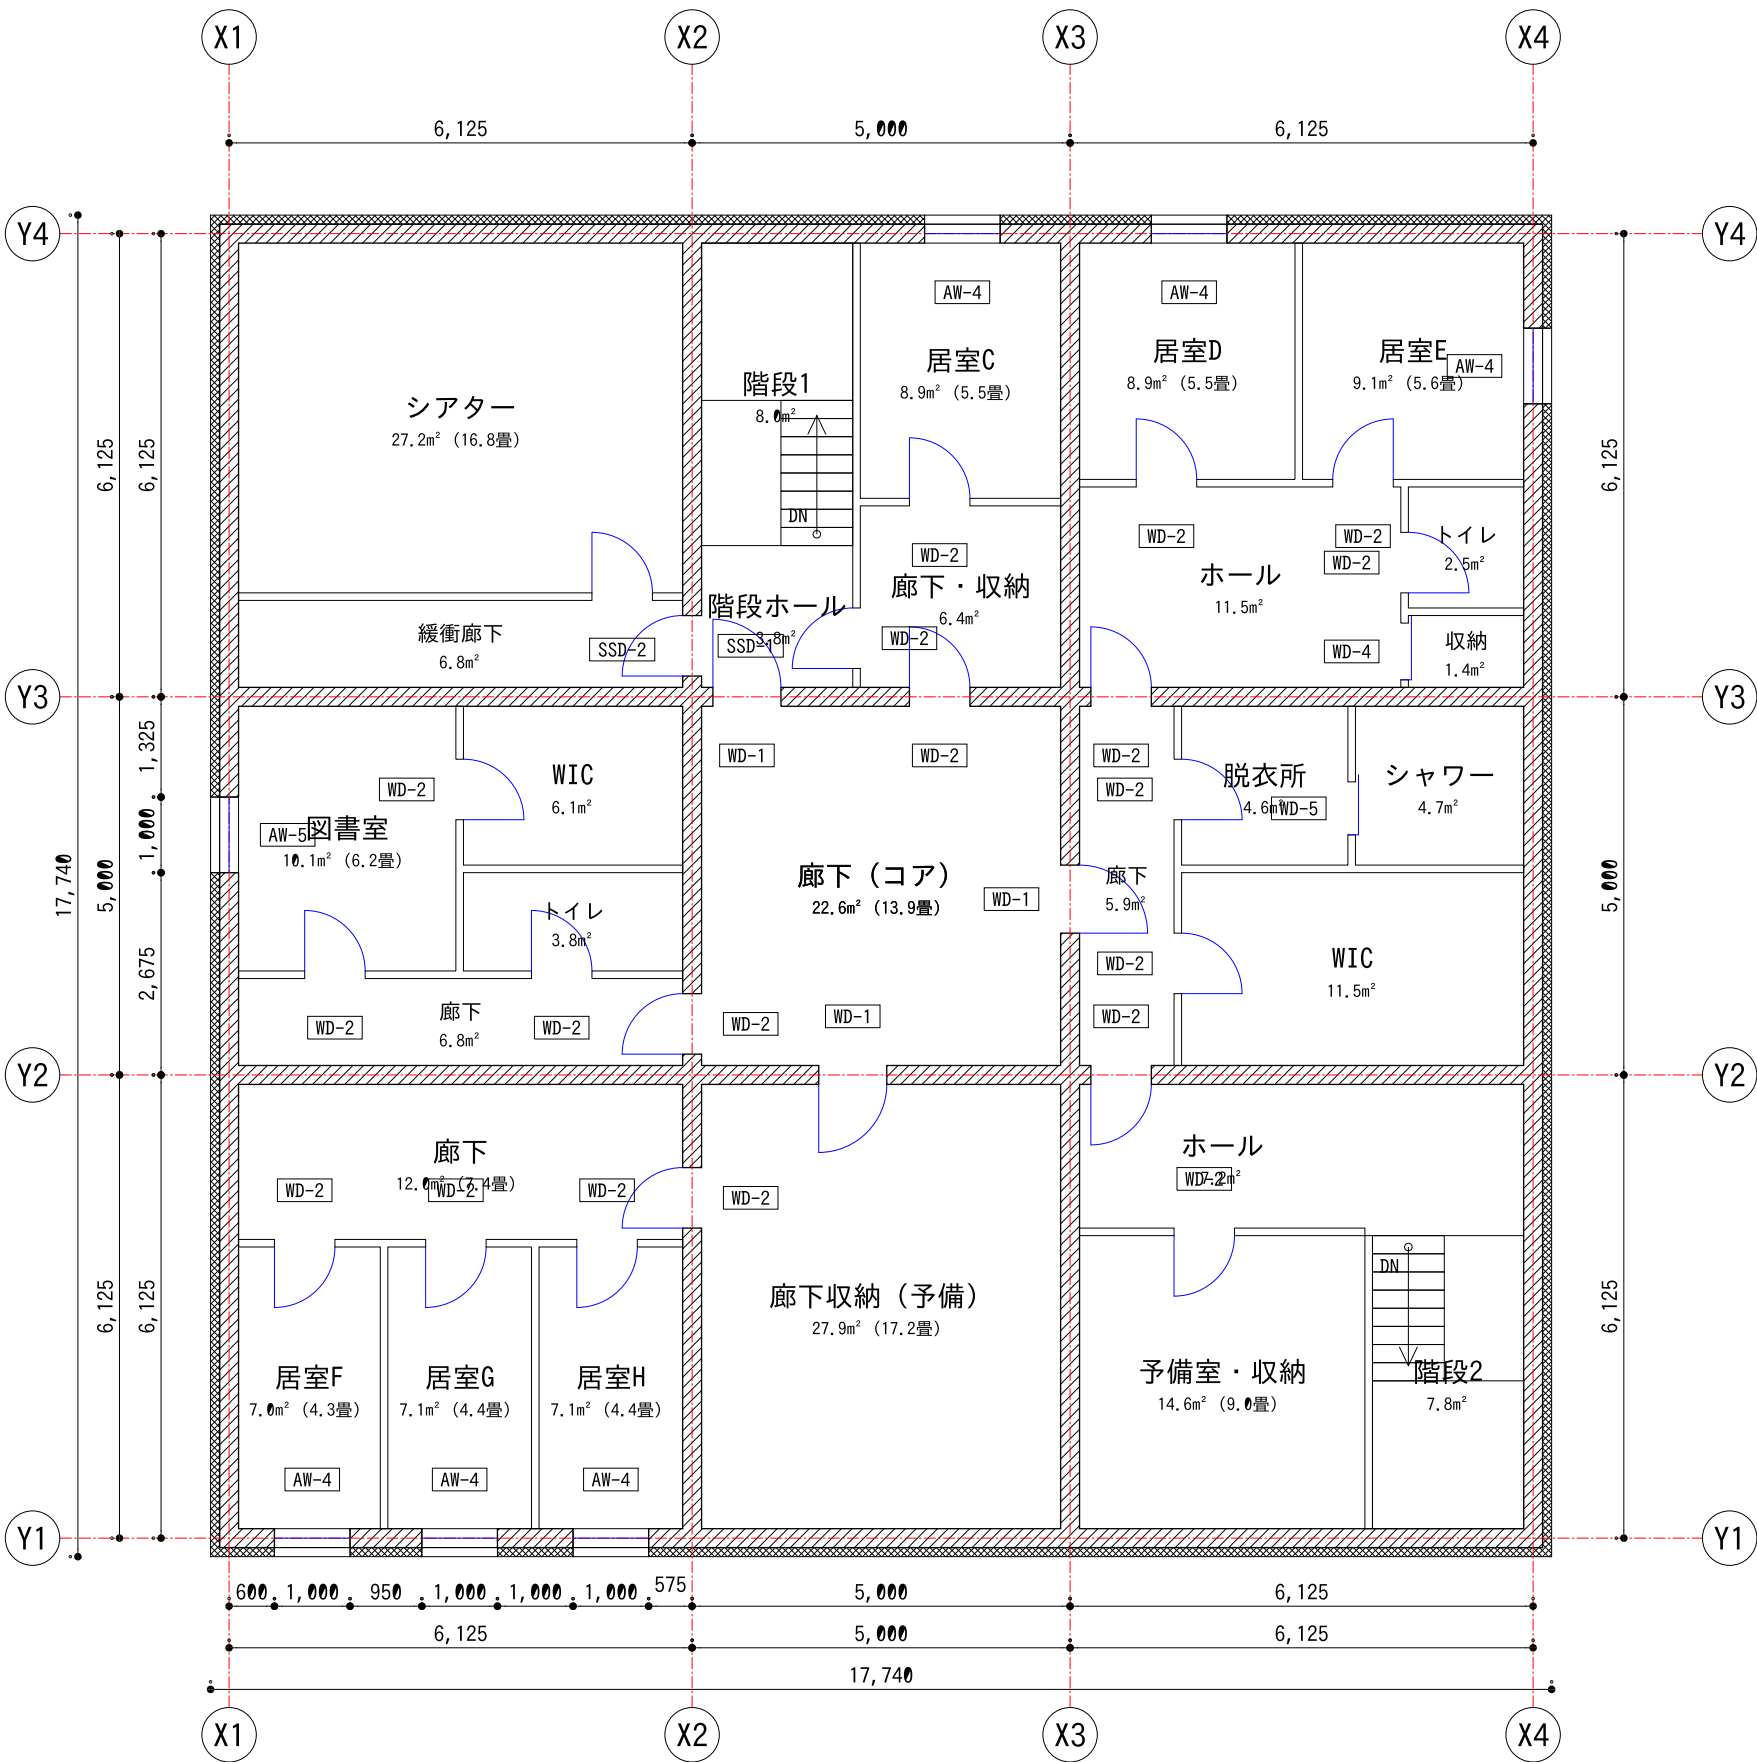

凡例

- RC壁 t=250 (耐力壁)
- 外断熱100+外装20
- 乾式間仕切 (LGS) t=100
- 通り芯 (壁芯)

特記


シアター: 浮き床+二重壁、前室 (緩衝廊下) で二重扉
2階の窓は提案値 (各 1.0×0.7m FIX)。無窓居室の排煙は要検討
間仕切: 乾式 (LGS+ボード)、耐震壁は1階と同位置
寸法: mm、面積: 壁芯内法の概算



2階平面図 S=1:100

2FL = 設計GL+4,700 (TP+113.70) /天井高 CH=2,600


工事名称	河沿要 (仮称) 新築計画			
図面名称	2階平面図			図番 A-04
縮尺	A3 1:100	日付 2026-10-03	設計 設計検討 (仮)	
段階	基本計画 / 本図は建築基準法令に基づく計画段階の検討図であり、確認申請・構造計算・関係機関協議により確定する			

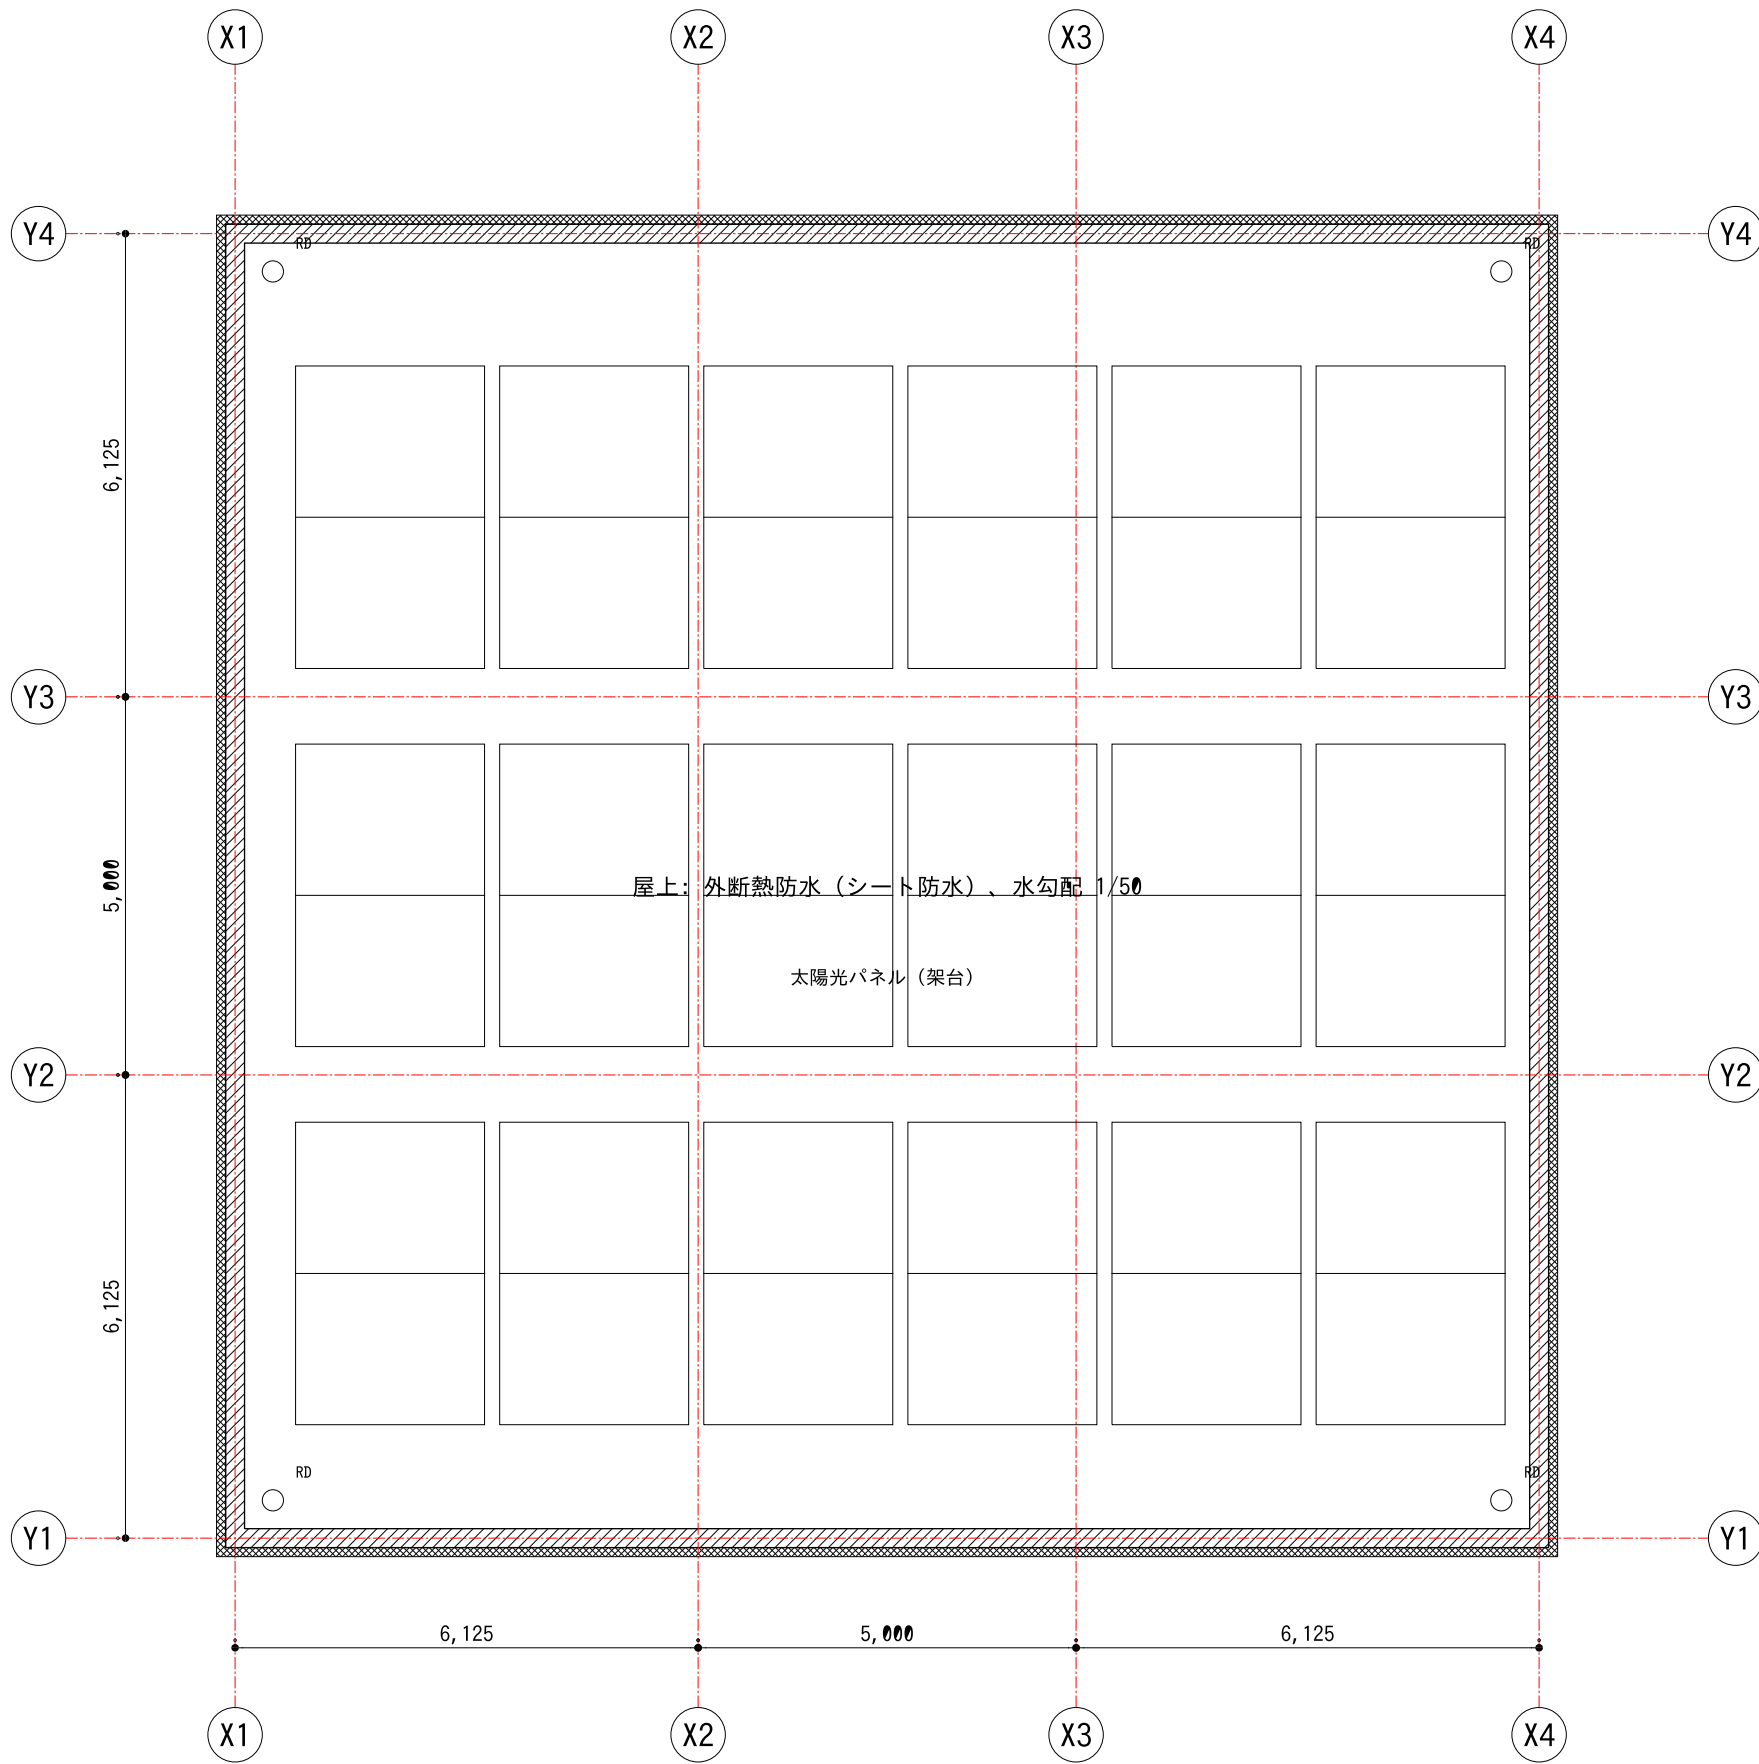


屋根伏図 S=1:100

RFL = 設計GL+7,900 / パラペット天端 GL+8,500


工事名称	河沿要（仮称）新築計画			
図面名称	屋根伏図			図番 A-05
縮尺	A3 1:100	日付 2026-10-03	設計 設計検討（仮）	
段階	基本計画 / 本図は建築基準法令に基づく計画段階の検討図であり、確認申請・構造計算・関係機関協議により確定する			

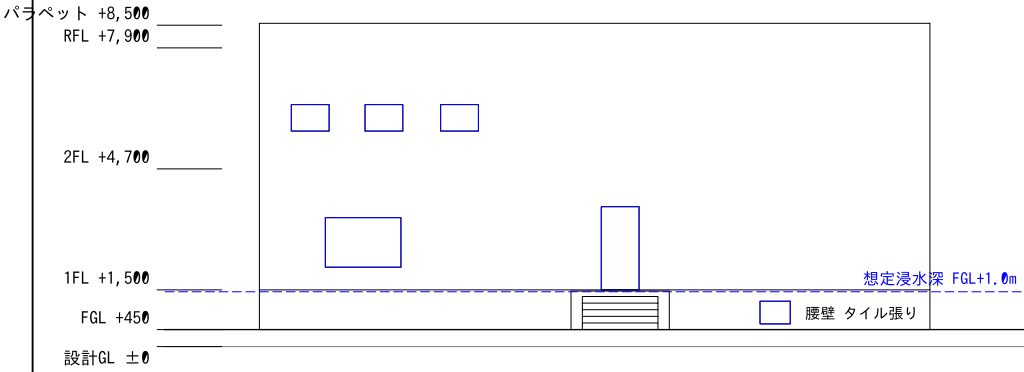


南立面図

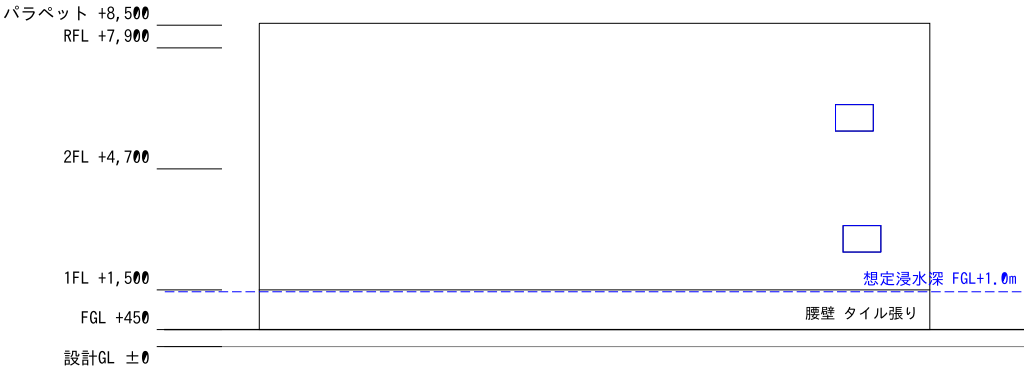

東立面図

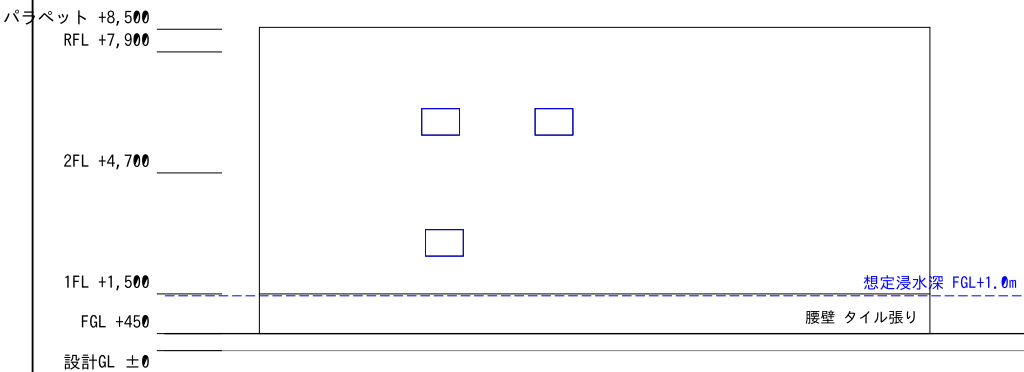

北立面図

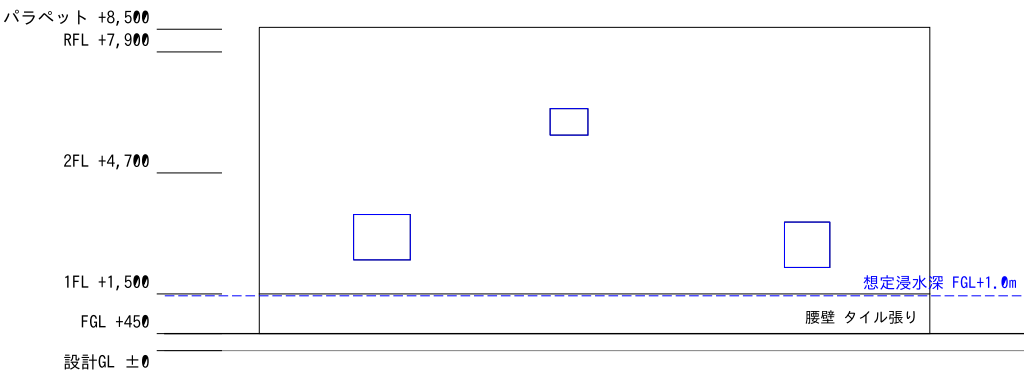


西立面図


外壁：外断熱100 + 外装仕上げ（腰壁 GL～+1,500 はタイル張り） 窓：FIX（トリプルガラス）

工事名称	河沿要（仮称）新築計画			
図面名称	立面図			図番 A-06
縮尺	A3 1:200	日付 2026-10-03	設計 設計検討（仮）	
段階	基本計画 / 本図は建築基準法令に基づく計画段階の検討図であり、確認申請・構造計算・関係機関協議により確定する			

断面図 A-A（X2-X3間、階段1を通る南北断面）

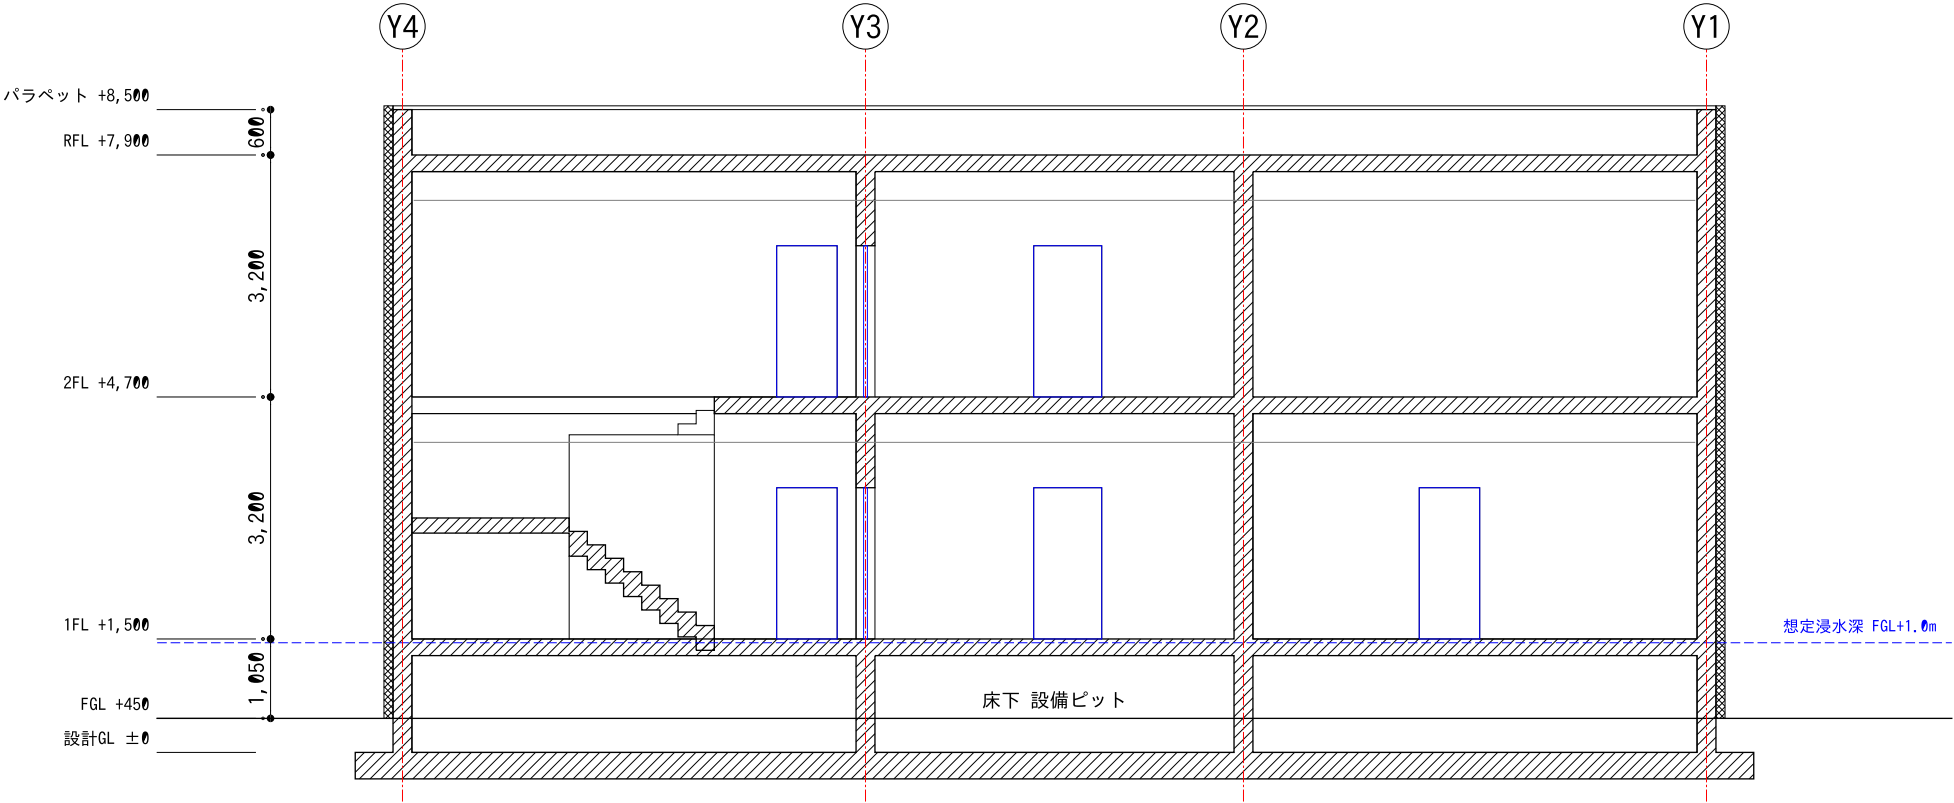

断面図 B-B（Y1-Y2間、LDK・階段2を通る東西断面）

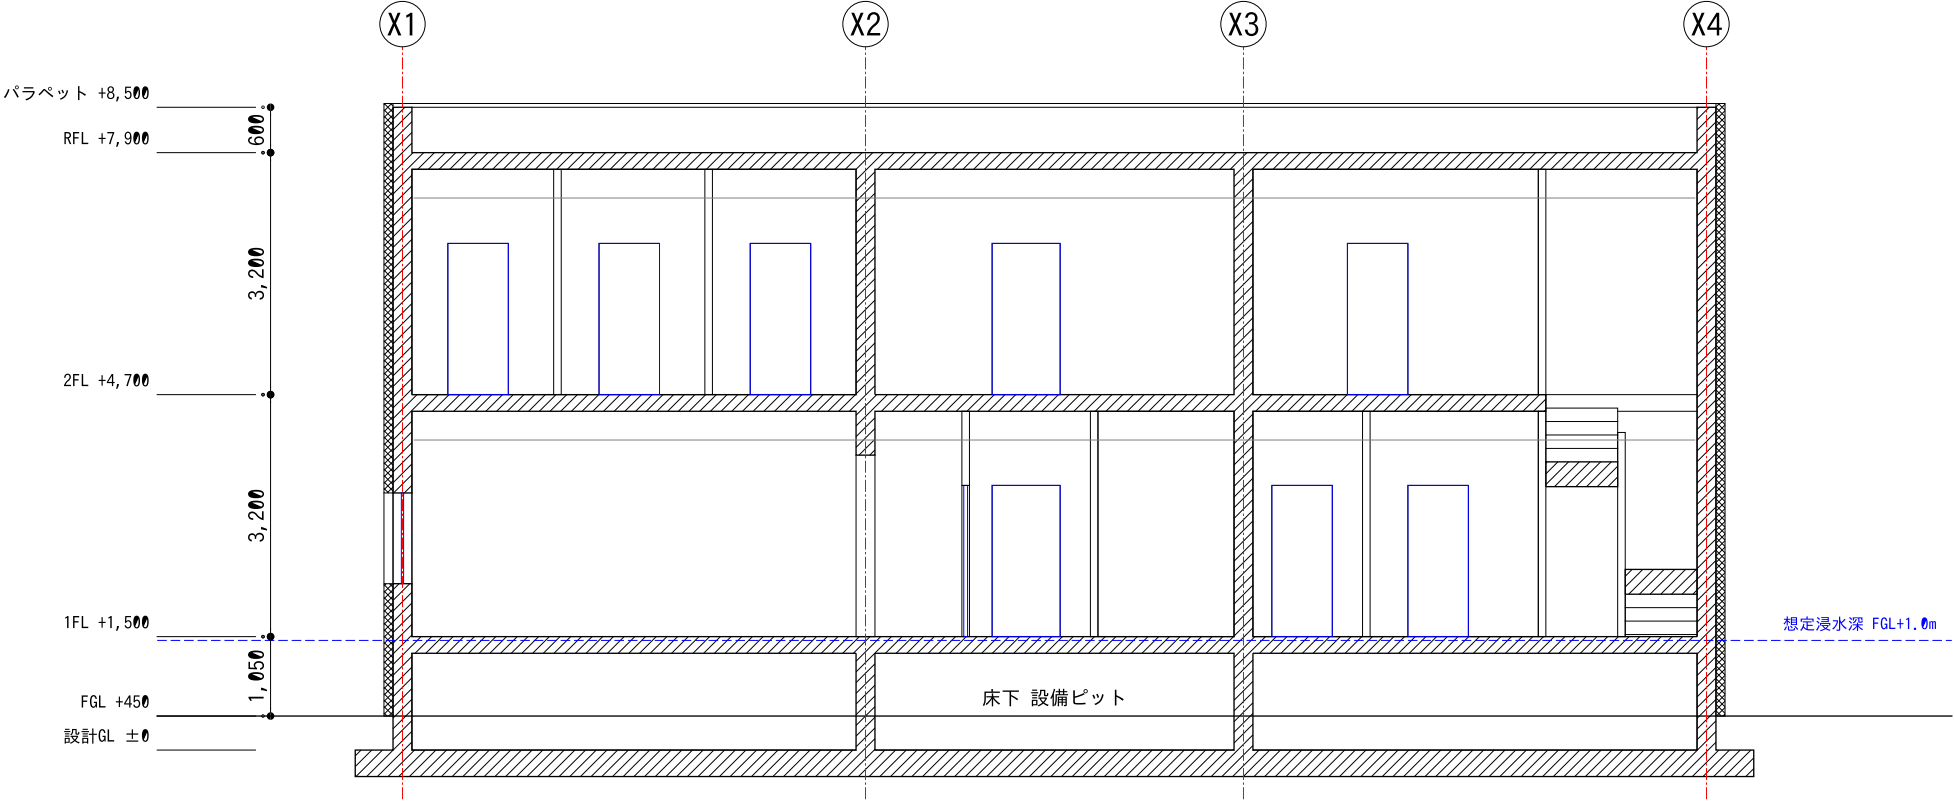

特記


階高 3,200×2／スラブ t=220／壁 RC t=250
天井高 CH=2,600（破線）。天井懐にダクト・浮き床
1FL=GL+1,500：想定浸水深(FGL+1.0m)より上
基礎：べた基礎 t=350＋地中梁（RC壁を基礎まで連続）
階段：蹴上 177.8 × 18段、踏面 240、有効幅 950（令23条 住宅）

工事名称	河沿要（仮称）新築計画			
図面名称	断面図（建物）			図番 A-07
縮尺	A3 1:100	日付 2026-10-03	設計 設計検討（仮）	
段階	基本計画 / 本図は建築基準法令に基づく計画段階の検討図であり、確認申請・構造計算・関係機関協議により確定する			


地形（DEM5A）

敷地 TP+109.3～109.6（ほぼ平坦）
北側道路 TP+112.5～113.0（敷地より約3.2m高い）
東側道路 TP+109.0→112.9（北へ上り）
→ 敷地は北・東からの表流水が集まる低い側。RC塀下部の止水と排水で対応
がけ（高さ2m超）からの離れ：北 約11.1m ≧ 2H=6.4m、東 約9.4m ≧ 2H=6.6m（東京都建築安全条例6条）















南北断面（建物中央 X2-X3間）（縦横同縮尺）

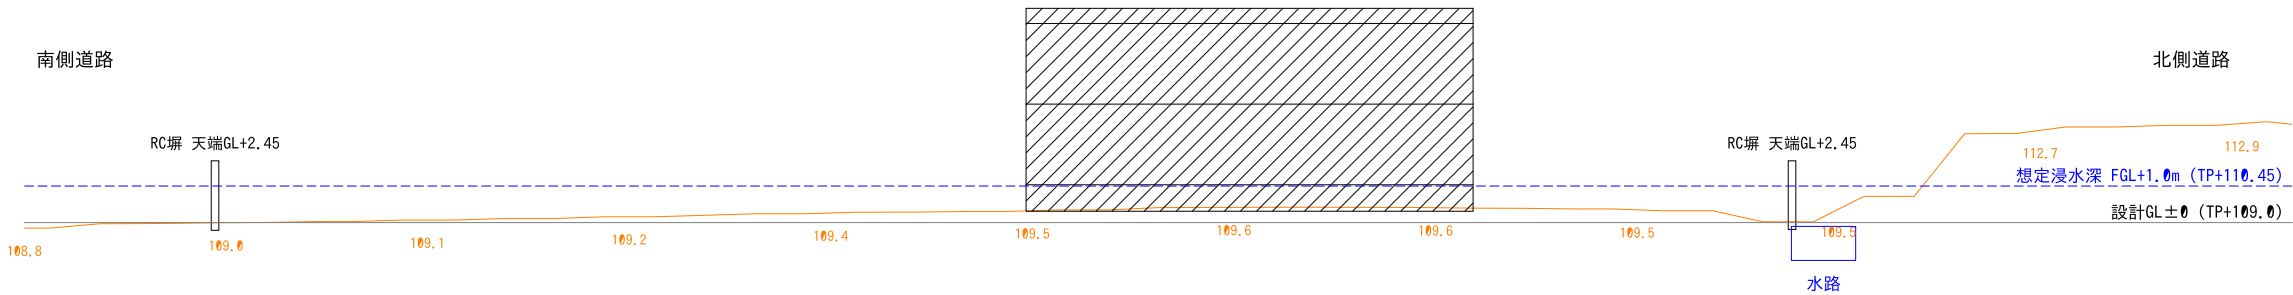

東西断面（建物中央 Y2-Y3間）（縦横同縮尺）

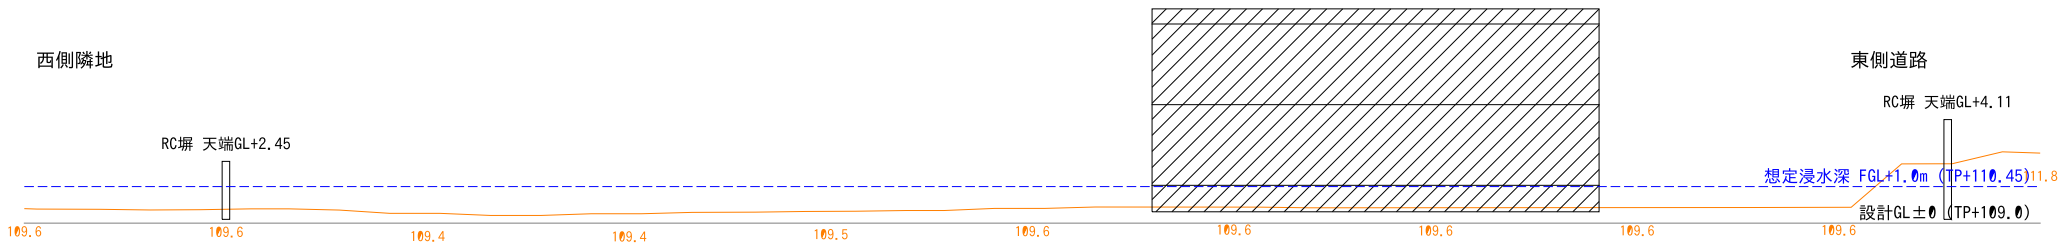

工事名称	河沿要（仮称）新築計画			
図面名称	敷地断面図（地形・浸水）			図番 A-08
縮尺	A3 1:300	日付 2026-10-03	設計 設計検討（仮）	
段階	基本計画 / 本図は建築基準法令に基づく計画段階の検討図であり、確認申請・構造計算・関係機関協議により確定する			

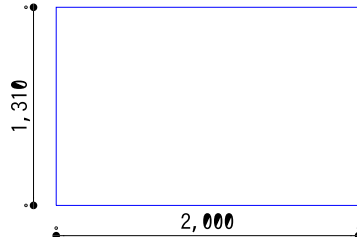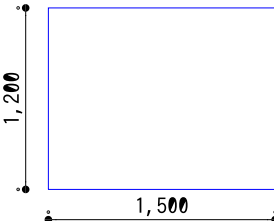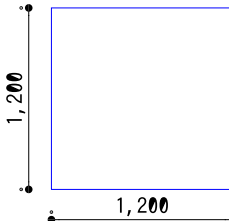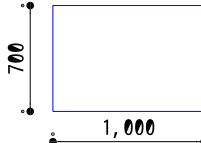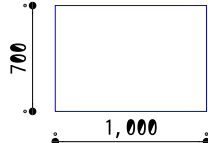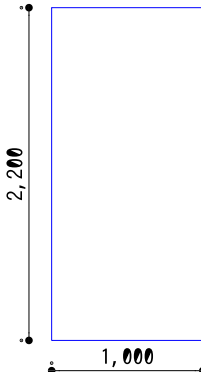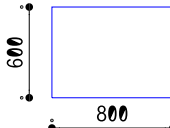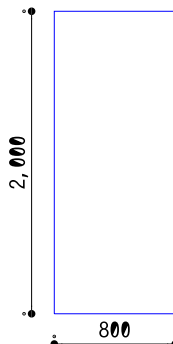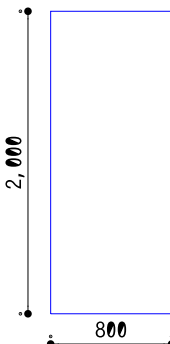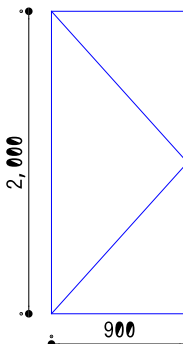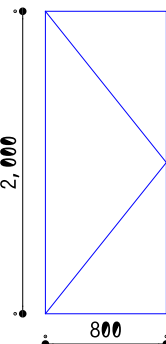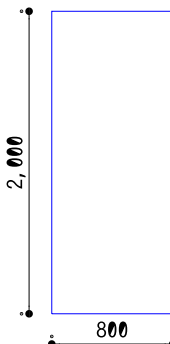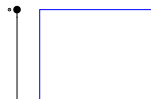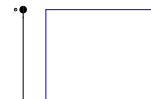AW-1		AW-2		AW-3		AW-4		AW-5		SD-1	
 名称: FIX窓 (LDK) 材質: 樹脂 (アルミ樹脂複合) W2,000×H1,310 数量: 1か所 (1F) ガラス: Low-E トリプルガラス (UVカット) ・FIX		 名称: FIX窓 (ジム) 材質: 樹脂 (アルミ樹脂複合) W1,500×H1,200 数量: 1か所 (1F) ガラス: Low-E トリプルガラス (UVカット) ・FIX		 名称: FIX窓 (LDK) 材質: 樹脂 (アルミ樹脂複合) W1,200×H1,200 数量: 1か所 (1F) ガラス: Low-E トリプルガラス (UVカット) ・FIX		 名称: FIX窓 (居室) 材質: 樹脂 (アルミ樹脂複合) W1,000×H700 数量: 8か所 (1F・2F) ガラス: Low-E トリプルガラス (UVカット) ・FIX		 名称: FIX窓 (図書室) 材質: 樹脂 (アルミ樹脂複合) W1,000×H700 数量: 1か所 (2F) ガラス: Low-E トリプルガラス (UVカット) ・FIX		 名称: 玄関ドア (断熱・防犯) 材質: 鋼製 (断熱) W1,000×H2,200 数量: 1か所 (1F)	
SD-2		SSD-1		SSD-2		WD-1		WD-2		WD-3	
 名称: 床下点検口 (防水扉) 材質: 鋼製 (断熱) W800×H600 数量: 1か所 (FDN)		 名称: 遮音ドア (Ts-35) 材質: 鋼製 遮音 W800×H2,000 数量: 2か所 (1F・2F)		 名称: 遮音ドア (両開き) 材質: 鋼製 遮音 W800×H2,000 数量: 1か所 (2F)		 名称: 木製片開き戸 材質: 木製 W900×H2,000 数量: 6か所 (1F・2F)		 名称: 木製片開き戸 材質: 木製 W800×H2,000 数量: 27か所 (1F・2F)		 名称: 木製引戸 材質: 木製 W800×H2,000 数量: 4か所 (1F)	
WD-4		WD-5				工事名称					
						河沿要 (仮称) 新築計画					
						図面名称					
						建具表					
				縮尺		A3 1:50・1:100		日付 2026-10-03		設計 設計検討 (仮)	
				段階		基本計画 / 本図は建築基準法令に基づく計画段階の検討図であり、確認申請・構造計算・関係機関協議により確定する					
						図番					
						A-09					

法規チェックリスト（建築基準法・同施行令・関連法令／設計仕様書）

区分	項目	根拠条文	規定・要求	計画	判定
ブリーフ	敷地面積	ブリーフv3 1章	地図・航空写真・DEMによる推定	3,154.17㎡（推定誤差 ±5%程度）	要確認
ブリーフ	建物外寸・グリッド	ブリーフv3 5章	内寸17.0m角、6.0/5.0/6.0、RC250＋外断熱120	壁芯 17.250m角、外寸 17.74m角	適合
ブリーフ	1階床高	ブリーフv3 3章	想定浸水深（FGL+1.0m）より上	1FL GL+1,500（FGL+1,050）	適合
ブリーフ	駐車台数	ブリーフv3 2章	3台	3台（ソーラーカーポート下）	適合
ブリーフ	RC塀	ブリーフv3 4章	H2,000（防犯）	全周 H2.0m 以上（東側坂道沿いは道路面+1.2m以上）	適合
ブリーフ	透水性舗装	ブリーフv3 3.1	駐車場に Dotcon+	約177㎡（一時貯留 約2.3㎡）	適合
集団規定	用途地域の制限	法48条・別表第2	準工業地域（推定・要確認）：住宅は建築可	一戸建ての住宅	要確認
集団規定	接道	法43条	道路に2m以上接する	南側道路 約13.9m・東側道路 約81.8m	適合
集団規定	建ぺい率	法53条	60%以下（角地緩和は不使用）	297.56/3,154.17 = 9.43%	適合
集団規定	容積率	法52条	min(指定200%，道路7.4m×0.6=444%)	595.12/3,154.17 = 18.87%	適合
集団規定	道路斜線（南）	法56条1項1号・2項	勾配1.5、後退距離 30.3m による緩和	建物南面で許容 102.0m ≥ 高さ 8.50m	適合
集団規定	道路斜線（東）	法56条1項1号・2項	後退距離 9.4m（道路高さが敷地より高い区間は緩和あり）	許容 36.4m ≥ 8.50m	適合
集団規定	隣地斜線	法56条1項2号	31m+2.5×L	最高高さ 8.50m < 31m	適合
集団規定	北側斜線	法56条1項3号	低層・中高層住居専用地域等	準工業地域（推定）	対象外
集団規定	日影規制	法56条の2・都条例	準工業：高さ10m超が対象（指定時）	高さ 8.50m ≤ 10m	適合
集団規定	防火地域等	法61条	指定未確認（耐火建築物で計画）	壁式RC造（耐火構造）で計画	要確認
都条例	がけ（北側）	東京都建築安全条例6条	高さ2m超のがけ：下端から2H=6.4m 以上離す	水路（がけ下端）まで 11.1m	適合
都条例	がけ（東側）	東京都建築安全条例6条	道路との高低差 最大3.3m：2H=6.6m	東側道路境界まで 9.4m	適合
都条例	角敷地の隅切り	東京都建築安全条例2条	幅員がいずれも6m未満の道路の角敷地	南側道路 約7.4m（6m以上）	対象外
都条例	敷地と道路（大規模建築物）	東京都建築安全条例4条	延べ1,000㎡超は接道長さの割増し	延べ 595㎡	対象外
単体規定	採光 1F ジム	法28条1項・令19条・20条	床面積 34.5㎡ × 15.29% = 5.28㎡（法定 1/7 = 4.93）	ガラス 1.80㎡ × K3.0 = 5.40㎡	適合
単体規定	採光 1F 居室A	法28条1項・令19条・20条	床面積 7.8㎡ × 15.29% = 1.19㎡（法定 1/7 = 1.11）	ガラス 0.70㎡ × K3.0 = 2.10㎡	適合
単体規定	採光 1F 居室B	法28条1項・令19条・20条	床面積 8.0㎡ × 15.29% = 1.22㎡（法定 1/7 = 1.14）	ガラス 0.70㎡ × K3.0 = 2.10㎡	適合
単体規定	採光 1F LDK	法28条1項・令19条・20条	床面積 41.3㎡ × 15.29% = 6.31㎡（法定 1/7 = 5.90）	ガラス 4.06㎡ × K3.0 = 12.18㎡	適合
単体規定	採光 2F 居室C	法28条1項・令19条・20条	床面積 8.9㎡ × 15.29% = 1.37㎡（法定 1/7 = 1.28）	ガラス 0.70㎡ × K3.0 = 2.10㎡	適合
単体規定	採光 2F 居室D	法28条1項・令19条・20条	床面積 8.9㎡ × 15.29% = 1.36㎡（法定 1/7 = 1.27）	ガラス 0.70㎡ × K3.0 = 2.10㎡	適合
単体規定	採光 2F 居室E	法28条1項・令19条・20条	床面積 9.1㎡ × 15.29% = 1.40㎡（法定 1/7 = 1.31）	ガラス 0.70㎡ × K3.0 = 2.10㎡	適合
単体規定	採光 2F 図書室	法28条1項・令19条・20条	床面積 10.1㎡ × 15.29% = 1.54㎡（法定 1/7 = 1.44）	ガラス 0.70㎡ × K3.0 = 2.10㎡	適合
単体規定	採光 2F 居室F	法28条1項・令19条・20条	床面積 7.0㎡ × 15.29% = 1.07㎡（法定 1/7 = 1.00）	ガラス 0.70㎡ × K3.0 = 2.10㎡	適合
単体規定	採光 2F 居室G	法28条1項・令19条・20条	床面積 7.1㎡ × 15.29% = 1.08㎡（法定 1/7 = 1.01）	ガラス 0.70㎡ × K3.0 = 2.10㎡	適合
単体規定	採光 2F 居室H	法28条1項・令19条・20条	床面積 7.1㎡ × 15.29% = 1.08㎡（法定 1/7 = 1.01）	ガラス 0.70㎡ × K3.0 = 2.10㎡	適合
単体規定	採光補正係数	令20条	準工業：K = 8d/h - 1（上限3.0）	隣地・道路まで十分な距離 → 3.0（要確認）	要確認
単体規定	換気	法28条2項・令20条の2	窓（1/20）または機械換気設備	全館空調・全熱交換換気（FIX窓に依存しない）	適合
単体規定	シックハウス（24時間換気）	法28条の2・令20条の8	0.5回/h 以上	全熱交換換気で常時換気	適合
単体規定	居室の天井高	令21条	2.1m以上	CH 2,600mm	適合
単体規定	階段（住宅）	令23条1項ただし書	幅750以上・蹴上230以下・踏面150以上	幅950・蹴上177.8・踏面240（2か所）	適合
単体規定	踊場・手すり	令24条・25条	高さ4m以内ごとに踊場、手すり設置	中間踊場（高さ 1.6m）・手すり設置	適合

判定：適合／要確認（条例・関係機関協議・別途計算による）／対象外。数値はすべて建物モデルから自動算定。

工事名称	河沿要（仮称）新築計画			
図面名称	法規チェックリスト（1/2）			図番 A-10
縮尺	A3 ー	日付 2026-10-03	設計 設計検討（仮）	
段階	基本計画 ／ 本図は建築基準法令に基づく計画段階の検討図であり、確認申請・構造計算・関係機関協議により確定する			

法規チェックリスト（建築基準法・同施行令・関連法令／設計仕様書）


区分	項目	根拠条文	規定・要求	計画	判定
単体規定	排煙（1階）	令126条の2・3	FIX窓の居室は「排煙上の無窓居室」→ 排煙設備	LDK・居室A・居室B・ジム：機械排煙（ブリーフv2確定）	適合
単体規定	排煙（2階）	令126条の2・平12建告1436号	2階居室も FIX 窓なら無窓居室	2階の窓仕様は未確定 → 機械排煙の追加または排煙窓を検討	要確認
単体規定	内装制限（火気使用室）	法35条の2・令128条の4第4項	2階建て住宅の1階で火気を使う室	IHクッキングヒーターなら対象外。ガス採用時は準不燃	要確認
単体規定	非常用の照明	令126条の4	一戸建ての住宅は除外	－	対象外
構造	壁量 1F X方向	平13国交告1026号 第5	12cm/m² 以上（地上2階建て）	耐力壁 61.6m / 床 297.6m² = 20.7cm/m²	適合
構造	壁量 1F Y方向	平13国交告1026号 第5	12cm/m² 以上（地上2階建て）	耐力壁 57.9m / 床 297.6m² = 19.5cm/m²	適合
構造	壁量 2F X方向	平13国交告1026号 第5	12cm/m² 以上（地上2階建て）	耐力壁 59.8m / 床 297.6m² = 20.1cm/m²	適合
構造	壁量 2F Y方向	平13国交告1026号 第5	12cm/m² 以上（地上2階建て）	耐力壁 62.7m / 床 297.6m² = 21.1cm/m²	適合
構造	耐力壁の厚さ	平13国交告1026号 第5	2階建て 15cm以上	25cm	適合
構造	耐力壁で囲まれた面積	平13国交告1026号 第5	60m² 以下	最大 37.5m²	適合
構造	階高・軒高・階数	平13国交告1026号 第1	階高3.5m以下・軒高20m以下・階数5以下	階高3.2m・軒高7.9m・2階	適合
構造	コンクリート強度	平13国交告1026号 第2・令74条	Fc18以上	Fc24	適合
構造	床版の厚さ	令77条の2・告示1026号	8cm以上かつ短辺/40	t=220（短辺 内法 5.88m /40 = 147）	適合
構造	かぶり厚さ	令79条	壁・床20（耐力壁30）／土に接する40／基礎60	設計かぶり 壁40・床30・土に接する50・基礎70	適合
構造	構造計算	法20条1項3号	壁式RC 2階建て（延べ200m²超）→ 構造計算（許容応力度等）	別途 構造計算書	要確認
構造	地盤・基礎	令38条	地盤調査に基づく基礎	べた基礎（杭の要否は調査後）	要確認
外構	RC塀	令62条の8（補強CB造）	RC塀は対象外 → 構造計算で同等以上の安全確認	H2.0m t=150 基礎1,200×400	要確認
外構	擁壁を兼ねる塀	法88条・令138条	高さ2m超の擁壁は工作物確認申請	東側坂道沿いで道路との段差を受ける区間が該当する可能性	要確認
外構	水路の占用・境界	法定外公共物管理条例（八王子市）	境界確定・占用協議	北側の塀・排水口の位置を協議	要確認
関連法令	建築物省エネ法	建築物省エネ法 10条（住宅の適合義務）	地域区分6：外皮 UA 0.87以下 ほか	UA 0.25～0.29（ブリーフ）	適合
関連法令	宅地造成・盛土等規制法	同法	規制区域内の切土・盛土	切土・盛土なし（現況地盤を維持）	適合
関連法令	雨水浸透	八王子市 雨水浸透施設の指導・助成	設置基準・補助の確認	貯留槽25m³・浸透トレンチ・浸透枳	要確認

判定：適合／要確認（条例・関係機関協議・別途計算による）／対象外。数値はすべて建物モデルから自動算定。

工事名称	河沿要（仮称）新築計画			
図面名称	法規チェックリスト（2/2）			図番 A-11
縮尺	A3 ー	日付 2026-10-03	設計 設計検討（仮）	
段階	基本計画 ／ 本図は建築基準法令に基づく計画段階の検討図であり、確認申請・構造計算・関係機関協議により確定する			

壁量・壁式構造の規定（平13国交告1026号）

階	方向	耐力壁長さ	壁量	判定
1F	X方向	61.6 m	20.7 cm/m ²	≧12 適合
1F	Y方向	57.9 m	19.5 cm/m ²	≧12 適合
2F	X方向	59.8 m	20.1 cm/m ²	≧12 適合
2F	Y方向	62.7 m	21.1 cm/m ²	≧12 適合
		壁厚	25 cm	≧15 適合

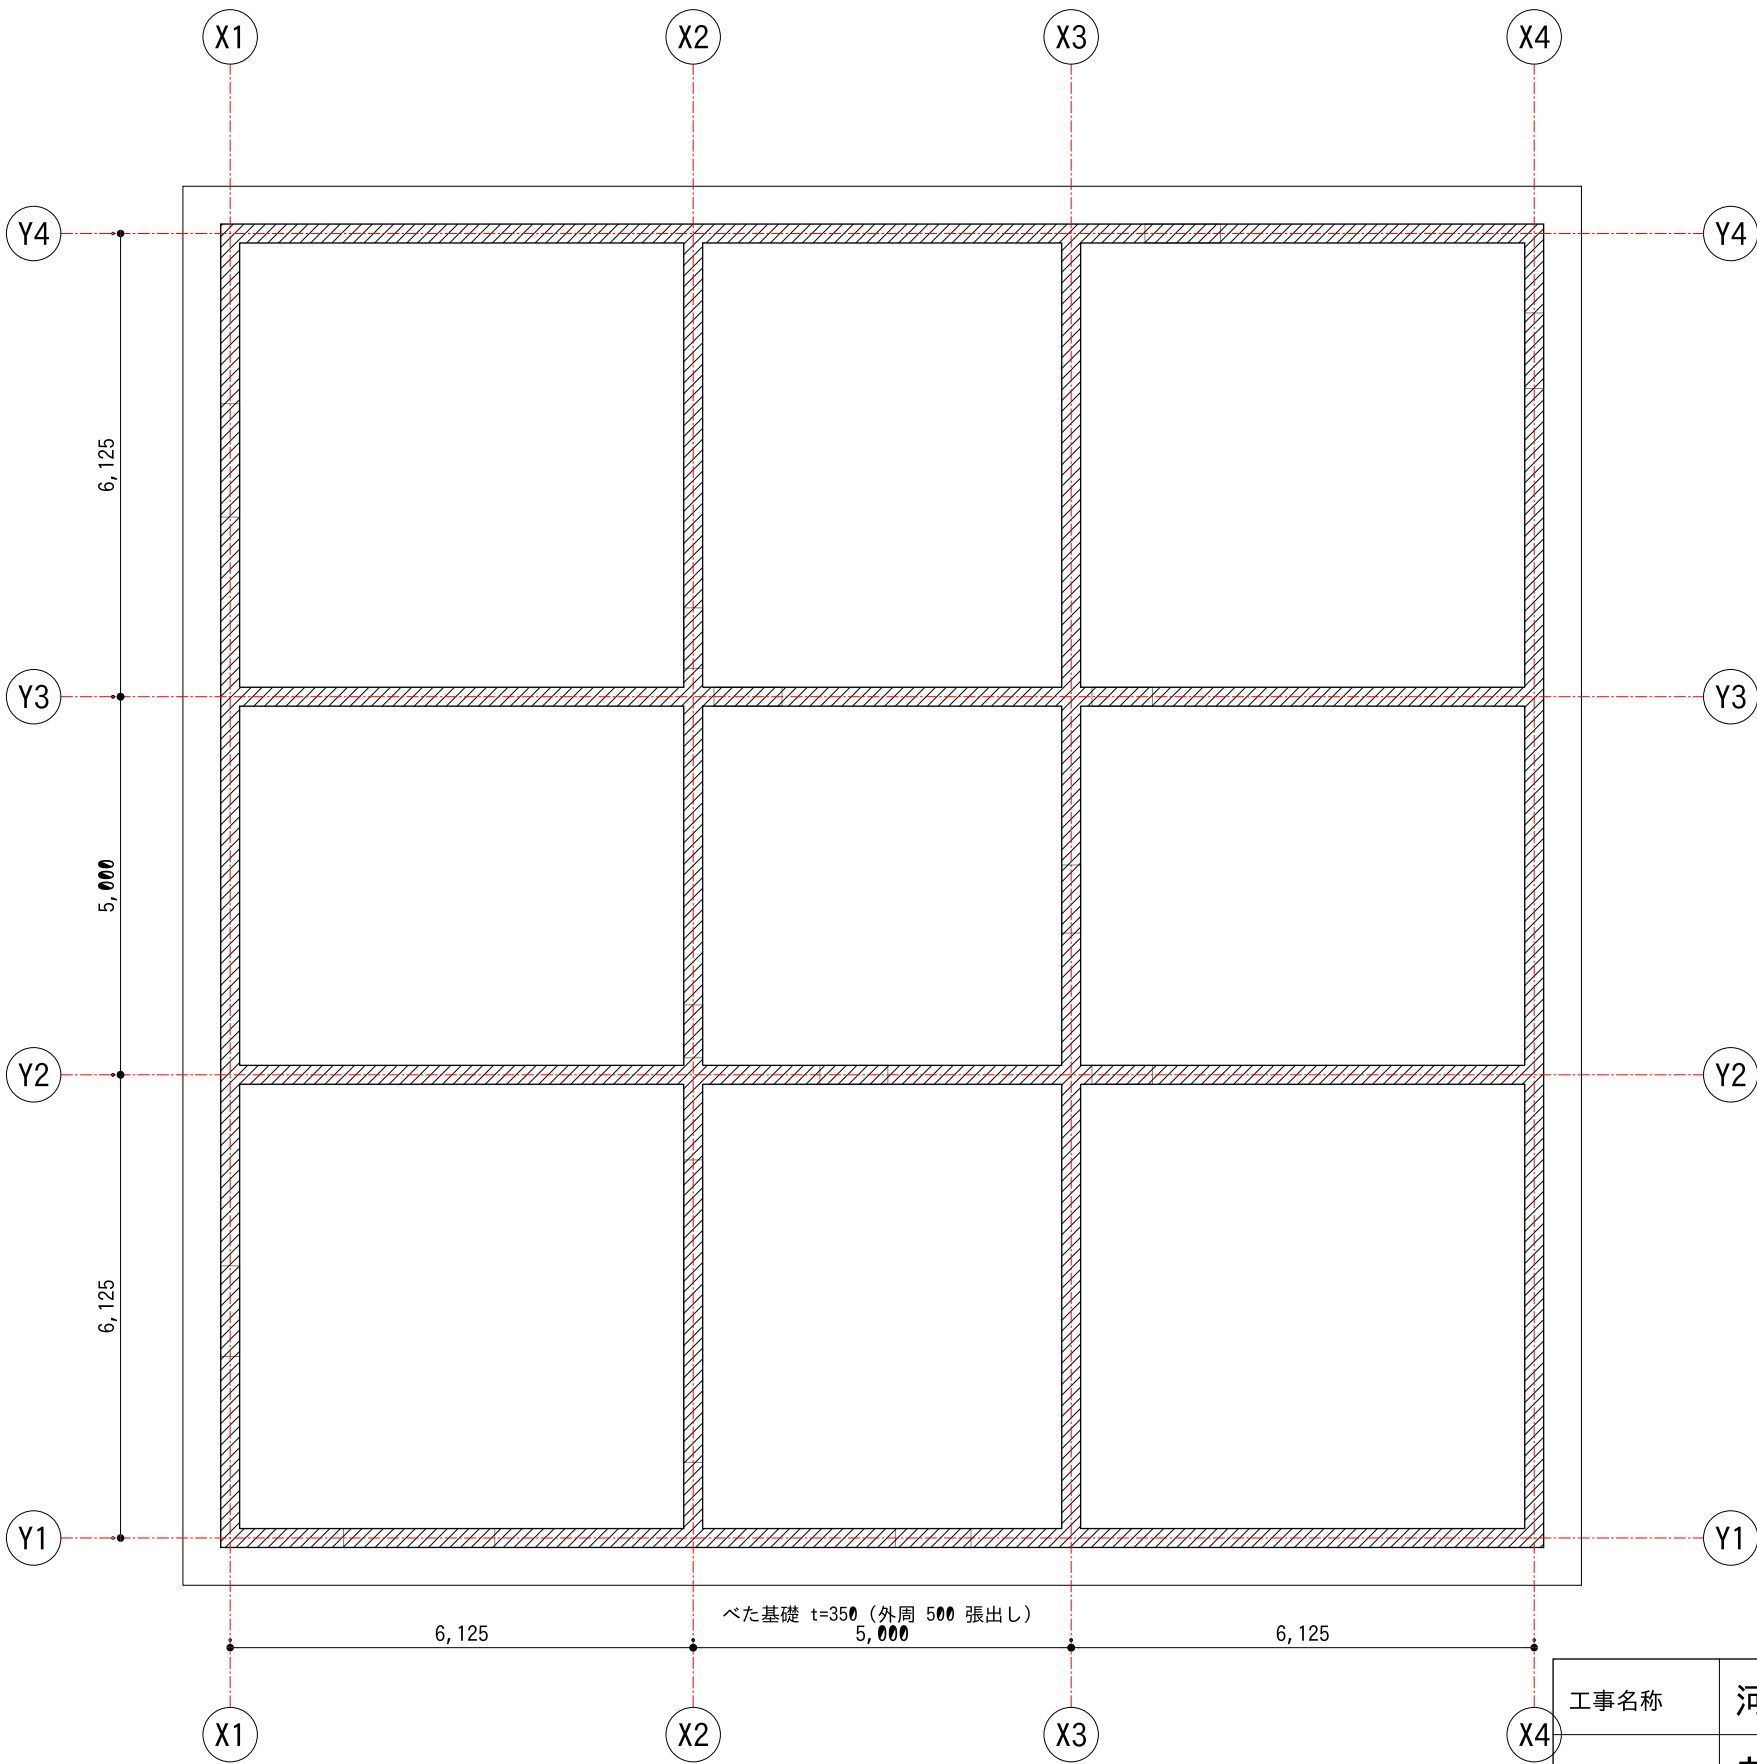

基礎伏図・耐力壁配置図（1階） S=1:100

網掛け=RC耐力壁 t=250（1・2階 同位置）、破線=開口

工事名称	河沿要（仮称）新築計画			
図面名称	基礎伏図・耐力壁配置図			図番 S-01
縮尺	A3 1:100	日付 2026-10-03	設計 設計検討（仮）	
段階	基本計画 / 本図は建築基準法令に基づく計画段階の検討図であり、確認申請・構造計算・関係機関協議により確定する			

(4) 車両門扉部 着脱式止水板 H600（立面）S=1:30

車両門扉 W5,000・人用 W1,200・勝手口 W1,000。止水板は門扉の近くに保管



特記

RC塀は令62条の8（補強コンクリートブロック造の塀）の対象外。風圧力・地震力に対する構造計算で安全を確認する
東側の坂道沿いで塀が道路との高低差（2m超）を受ける区間は、擁壁として工作物確認申請の対象（令138条）
塀は境界の内側に設置。北側は水路の管理境界との協議に従う
雨水浸透施設は、地盤調査（透水係数・地下水位）と八王子市の指導・助成制度を確認して決定

(1) RC塀 断面 S=1:30



壁 t=150 縦横 D10@200 ダブル／基礎 1,200×400・根入れ 900
天端に笠木・侵入防止金物、打継ぎ部に止水板

(2) 排水口 □150+フラップ弁 S=1:30

外側からの逆流を防ぐ。点検・清掃が可能な位置に設置

(3) 透水舗装（駐車場）断面 S=1:30

一時貯留 約13L/m²。車両荷重に応じた製品仕様を確認

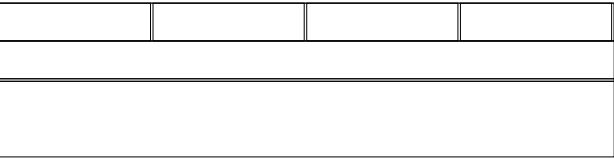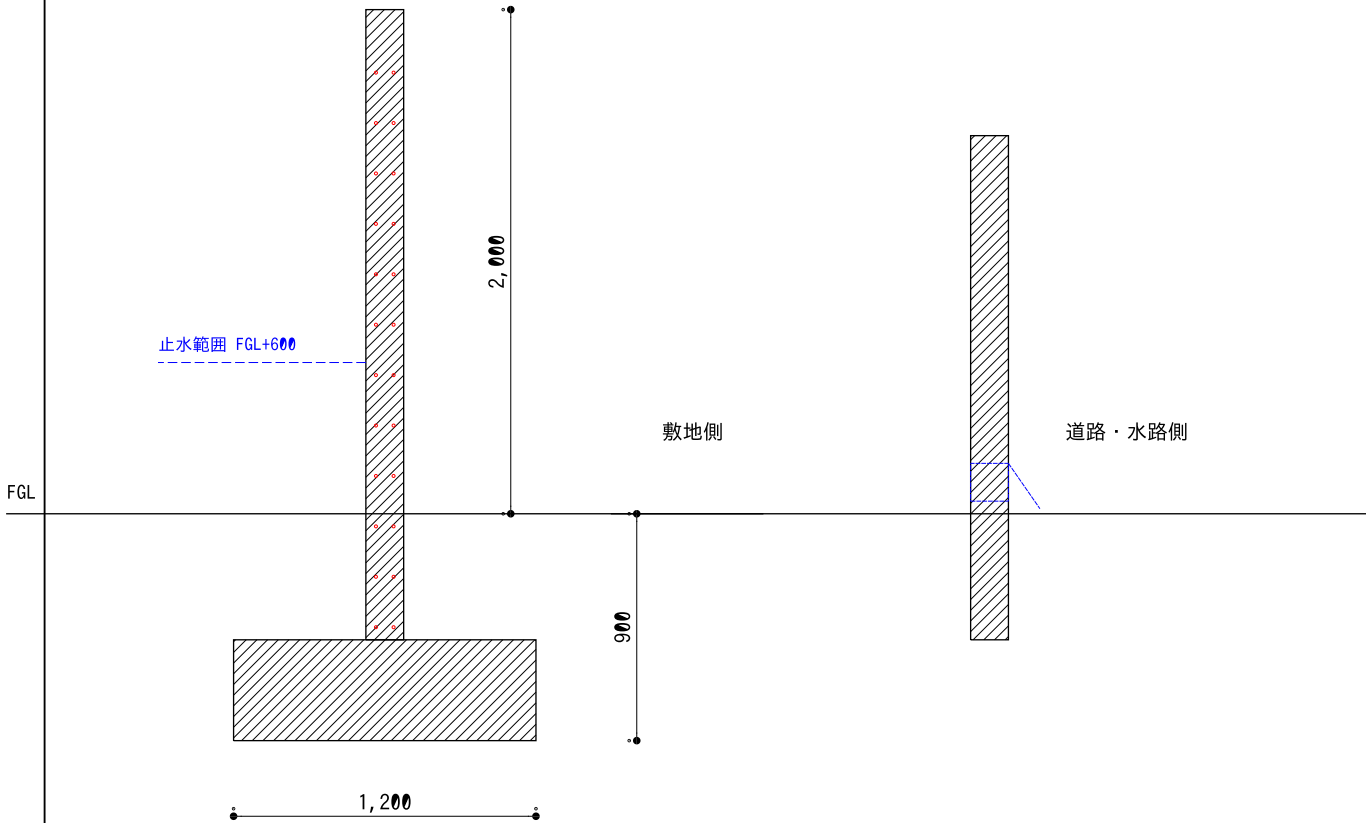

Dotcon+ 600角 t=150（目地10mm から浸透）
碎石路盤 t=150（単粒度碎石）
透水シート
路床（現況土・透水試験で確認）

工事名称	河沿要（仮称）新築計画			
図面名称	RC塀・止水・透水舗装 詳細図			図番 S-02
縮尺	A3 1:30	日付 2026-10-03	設計 設計検討（仮）	
段階	基本計画 / 本図は建築基準法令に基づく計画段階の検討図であり、確認申請・構造計算・関係機関協議により確定する			